


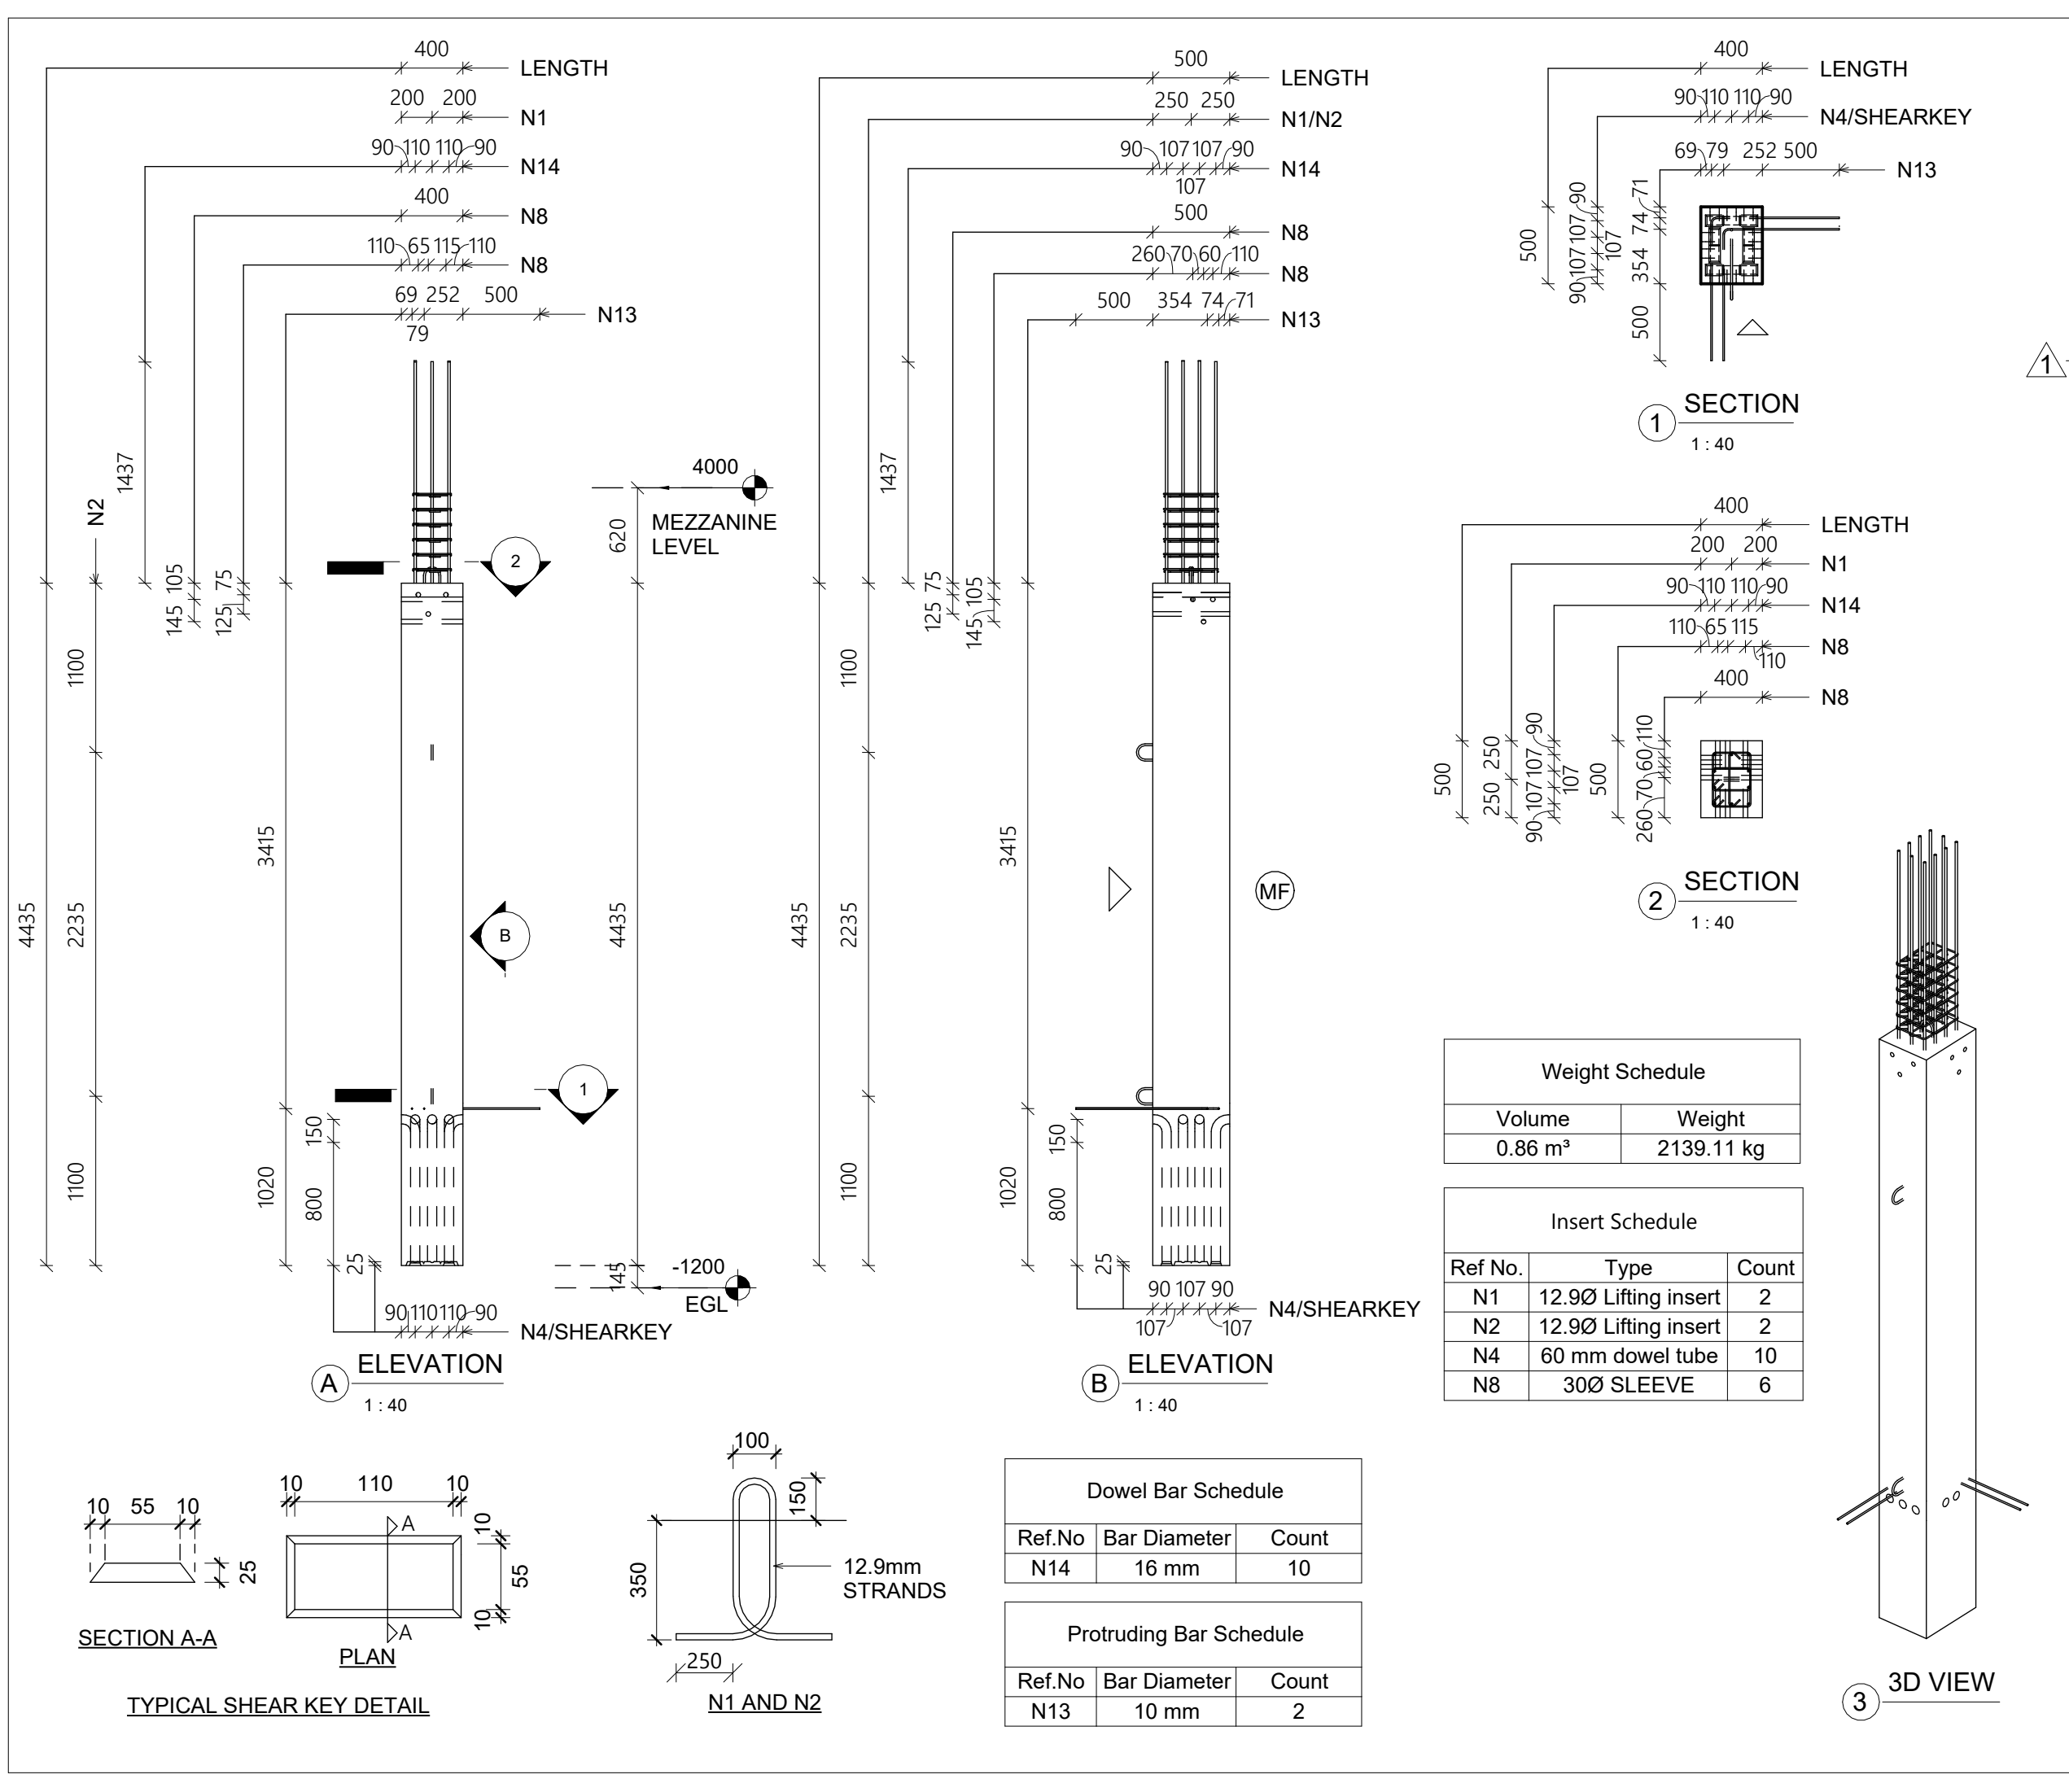

Weight Schedule	
Volume	Weight
0.86 m³	2139.11 kg

Insert Schedule		
Ref No.	Type	Count
N1	12.9Ø Lifting insert	2
N2	12.9Ø Lifting insert	2
N4	60 mm dowel tube	10
N8	30Ø SLEEVE	6

Dowel Bar Schedule		
Ref.No	Bar Diameter	Count
N14	16 mm	10

Protruding Bar Schedule		
Ref.No	Bar Diameter	Count
N13	10 mm	2

PROJECT -:
MF FACTORY

GENERAL NOTES:

GRADE OF CONCRETE	- M40
GRADE OF STEEL	- Fe500
STRIPPING STRENGTH	- M20
COLUMN COVER	- 40mm

ALL DIMENSIONS ARE IN MM

LEGENDS:

ERECTION MARK	-	
MOULD FACE	-	

CONTRACTOR -:

VME Precast Products

Arihant Esta, 2g2, 2nd floor,
No.370, Church Road, Mogappair East,
Chennai-600037.
Tel:+91- 98400 - 41400 / 90802 - 22066

STRUCTURAL CONSULTANT -:

ES STRUCTURAL CONSULTANT
B167, 12th cross street, Jawahar Nagar,
Palayamkottai, Tirunelveli-627007
Cell No: +91 9865803764

1	25-04-25	REVISED AS PER COULDED	PK	PRC
0	21-03-25	FOR APPROVAL	PK	PRC
Rev	Date	Description	Chkd	Appd.

REVISION SCHEDULE

DRAWING TITLE -:

PC-GF-01-MOULD DRAWING

JOB NO. : ESP24075	DRAWN BY:- AR
ELEMENT NO. : PC-GF-01	SHEET SIZE:- A3
DWG. NO. : PC-GF-01(M)	REV.NO:- 1
SCALE : 1 : 40	LEVEL. : GF