

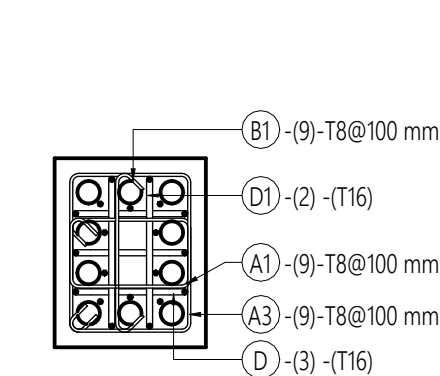


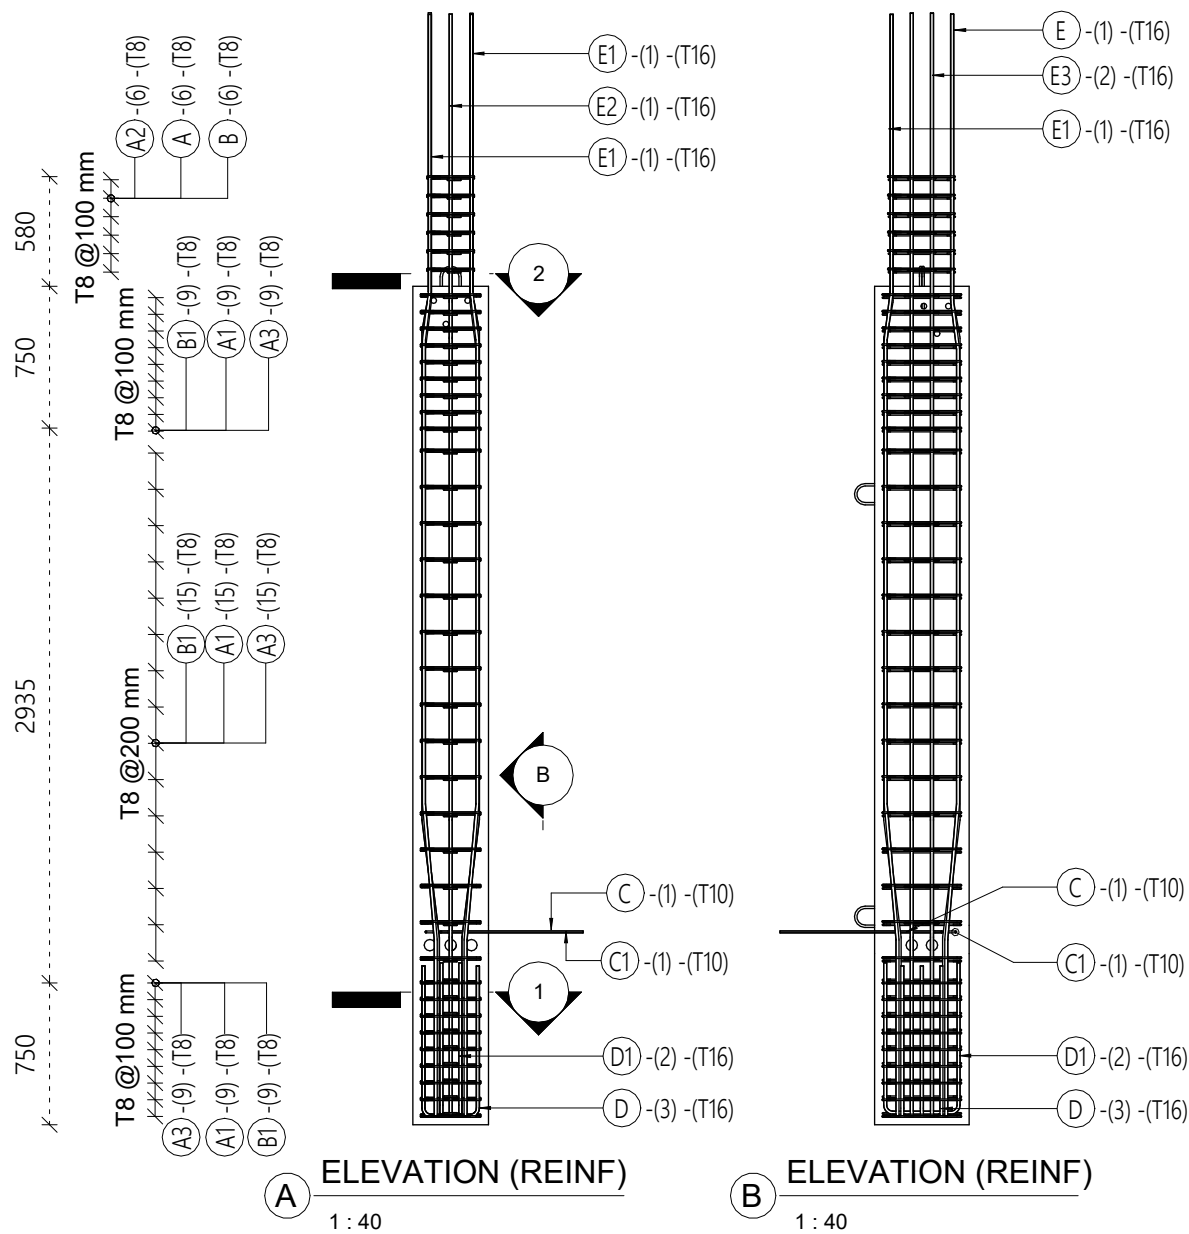

1 SECTION (REINF)
1 : 20

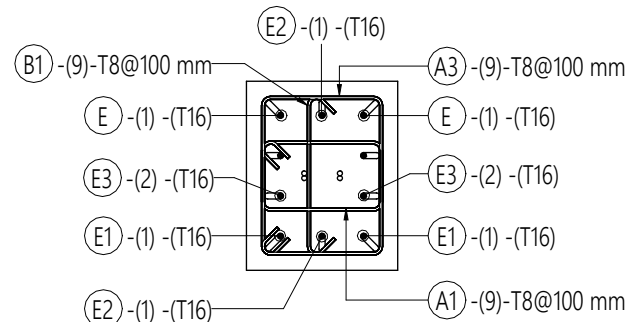

2 SECTION (REINF)
1 : 20

Summary Schedule			
Bar Diameter	Total Bar Length	Weight	
8 mm	124425 mm	49.16 kg	
10 mm	3350 mm	2.07 kg	
16 mm	67950 mm	107.38 kg	
		195725 mm	158.61 kg

Rebar schedule for PC-GF-01 (A)												
Schedule Mark	Bar Diameter	Shape	A	B	C	D	E	G	Bar Length	Total Bar Length	Quantity	Weight
A	8 mm	M_T1	70 mm	250 mm	150 mm	250 mm	150 mm	70 mm	900 mm	5400 mm	6	2.13 kg
A1	8 mm	M_T1	70 mm	185 mm	320 mm	180 mm	320 mm	70 mm	1125 mm	37125 mm	33	14.67 kg
A2	8 mm	M_T1	70 mm	250 mm	355 mm	250 mm	355 mm	70 mm	1325 mm	7950 mm	6	3.14 kg
A3	8 mm	M_T1	70 mm	320 mm	420 mm	320 mm	420 mm	70 mm	1575 mm	51975 mm	33	20.53 kg
B	8 mm	M_T10	70 mm	355 mm	0 mm	0 mm	0 mm	70 mm	500 mm	3000 mm	6	1.19 kg
B1	8 mm	M_T10	70 mm	420 mm	0 mm	0 mm	0 mm	70 mm	575 mm	18975 mm	33	7.50 kg
C	10 mm	M_17A	0 mm	855 mm	755 mm	0 mm	0 mm	0 mm	1600 mm	1600 mm	1	0.99 kg
C1	10 mm	M_17A	0 mm	930 mm	835 mm	0 mm	0 mm	0 mm	1750 mm	1750 mm	1	1.08 kg
D	16 mm	M_17	0 mm	800 mm	300 mm	800 mm	0 mm	0 mm	1850 mm	5550 mm	3	8.77 kg
D1	16 mm	M_17	0 mm	800 mm	400 mm	800 mm	0 mm	0 mm	1950 mm	3900 mm	2	6.16 kg
									137225 mm	124	66.16 kg	

Rebar schedule for PC-GF-01(B)												
Schedule Mark	Bar Diameter	Shape	A	B	C	D	E	Bar Length	Total Bar Length	Quantity	Weight	
E	16 mm	Rebar Shape 30	935 mm	720 mm	2405 mm	255 mm	1520 mm	5850 mm	11700 mm	2	18.49 kg	
E1	16 mm	Rebar Shape 30	935 mm	720 mm	2455 mm	255 mm	1470 mm	5850 mm	11700 mm	2	18.49 kg	
E2	16 mm	Rebar Shape 30	950 mm	625 mm	2550 mm	195 mm	1520 mm	5850 mm	11700 mm	2	18.49 kg	
E3	16 mm	Rebar Shape 30	950 mm	625 mm	2585 mm	195 mm	<varies>	5850 mm	23400 mm	4	36.98 kg	
									58500 mm	10	92.45 kg	

Rebar Shape	Shape Image
M_T1	
M_17	
M_T10	
M_17A	
REBAR SHAPE30	

PROJECT -: MF FACTORY

GENERAL NOTES:

GRADE OF CONCRETE - M40

GRADE OF STEEL - Fe500

STRIPPING STRENGTH - M20

COLUMN COVER - 40mm

ALL DIMENSIONS ARE IN MM

LEGENDS:

ERECTION MARK -

MOULD FACE -

CONTRACTOR -:

VME Precast Products

Arihant Esta, 2g2, 2nd floor,
No.370, Church Road, Mogappair East,
Chennai-600037.
Tel:+91- 98400 - 41400 / 90802 - 22066

STRUCTURAL CONSULTANT -:

ES STRUCTURAL CONSULTANT

B167, 12th cross street, Jawahar Nagar,
Palayamkottai, Tirunelveli-627007
Cell No: +91 9865803764

1	25-04-25	REVISED AS PER COULDED	PK	PRC
0	21-03-25	FOR APPROVAL	PK	PRC
Rev	Date	Description	Chkd	Appd.

REVISION SCHEDULE

DRAWING TITLE -:

PC-MZ-01-REINF DRAWING

JOB NO. : ESP24075	DRAWN BY:- AR
ELEMENT NO. : PC-GF-01	SHEET SIZE:- A3
DWG. NO. : PC-GF-01(R)	REV.NO:- 1
SCALE : As indicated	LEVEL. : GF