


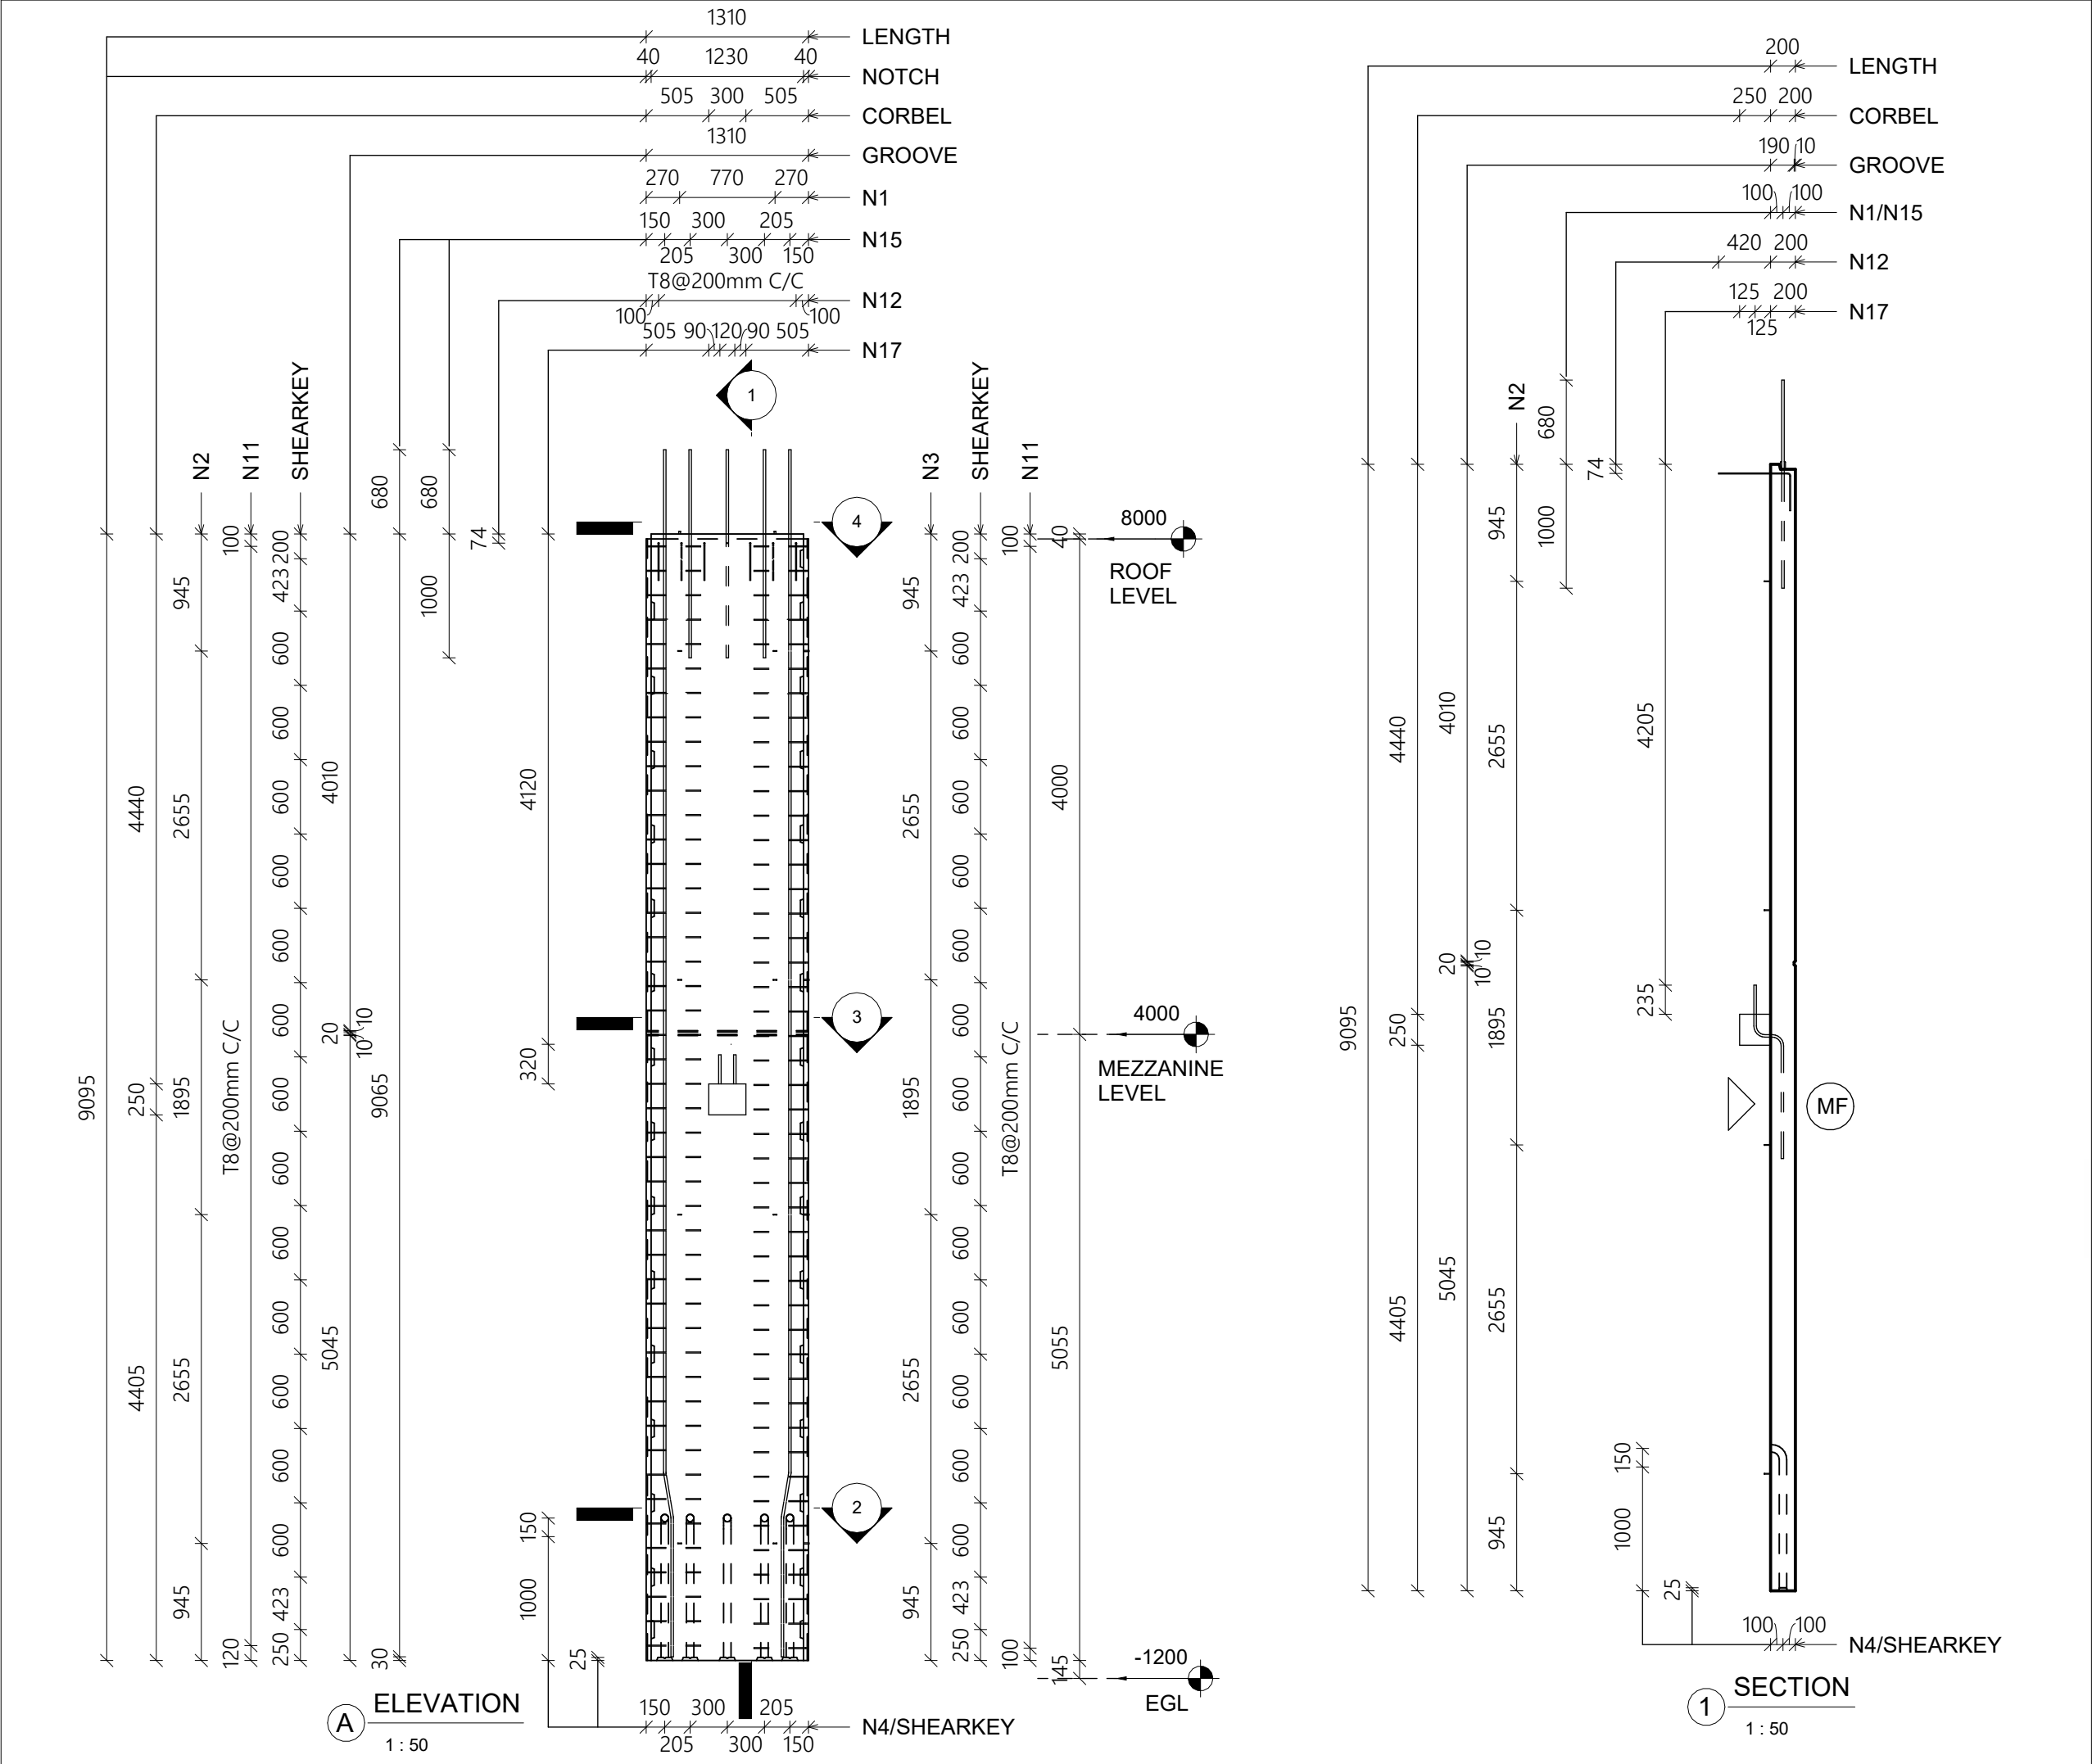

PROJECT :-
MF FACTORY

GENERAL NOTES:

GRADE OF CONCRETE - M40
GRADE OF STEEL - Fe500

COVER

WALL - 30mm
CORBEL - 25mm

ALL DIMENSIONS ARE IN MM

LEGENDS:

ERECTION MARK - 
MOULD FACE - 

CONTRACTOR :-

VME Precast Products
 Arihant Esta, 2g2, 2nd floor,
No.370, Church Road, Mogappair East,
Chennai-600037.
Tel:+91- 98400 - 41400 / 90802 - 22066

STRUCTURAL CONSULTANT :-

ES STRUCTURAL CONSULTANT
 B167, 12th cross street, Jawahar Nagar,
Palayamkottai, Tirunelveli-627007
Cell No: +91 9865803764

0	26-07-25	FOR APPROVAL	PK	PRC
Rev	Date	Description	Chkd	Appd.

REVISION SCHEDULE

DRAWING TITLE :-

PW-GF-01-MOULD DRAWING

JOB NO. : ESP24075	DRAWN BY:- IH
ELEMENT NO. : PW-GF-01	SHEET SIZE:- A3
DWG. NO. : PW-GF-01(M1)	REV.NO:- 0
SCALE : 1 : 50	LEVEL. : GF