




TYPICAL SHEAR KEY DETAIL

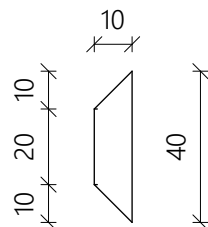

TYPICAL GROOVE DETAIL

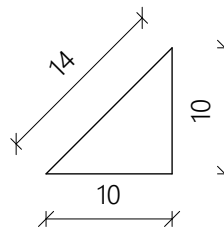

TYPICAL CHAMFER DETAIL

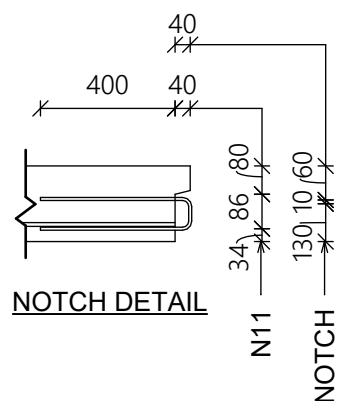


NOTCH DETAIL

Insert Schedule		
Ref No.	Type	Count
N1	RR-SA-5.0-240	2
N2	RR-SA-1.4-160	8
N3	RR-SA-2.5-200	4
N4	60 mm dowel tube	5


U-bar Schedule		
Ref.No	Bar Diameter	Quantity
N11	8 mm	92

Projecting Bar Schedule		
Ref.No	Bar Diameter	Quantity
N12	8 mm	7

Dowel Bar Schedule		
Ref.No	Bar Diameter	Quantity
N15	20 mm	5
N17	20 mm	2

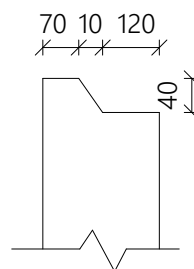

TOP NOTCH DETAIL

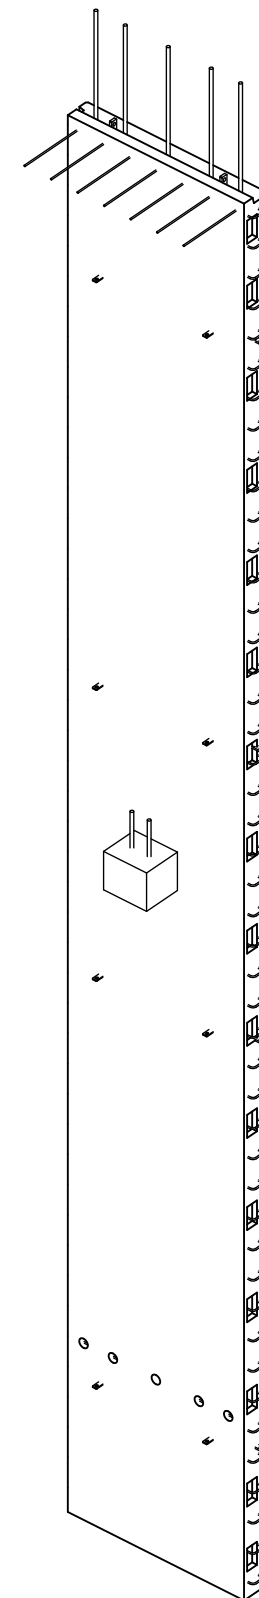

5 3D VIEW

PROJECT -:
MF FACTORY

GENERAL NOTES:

GRADE OF CONCRETE - M40

GRADE OF STEEL - Fe500

COVER

WALL - 30mm

CORBEL - 25mm

ALL DIMENSIONS ARE IN MM

LEGENDS:

ERECTION MARK -

MOULD FACE - MF

CONTRACTOR -:

VME Precast Products

 Arihant Esta, 2g2, 2nd floor,
No.370, Church Road, Mogappair East,
Chennai-600037.
Tel:+91- 98400 - 41400 / 90802 - 22066

STRUCTURAL CONSULTANT -:

ES STRUCTURAL CONSULTANT
 B167, 12th cross street, Jawahar Nagar,
 Palayamkottai, Tirunelveli-627007
 Cell No: +91 9865803764

0	26-07-25	FOR APPROVAL	PK	PRC
Rev	Date	Description	Chkd	Appd.

REVISION SCHEDULE

DRAWING TITLE:-

PW-GF-01-MOULD DRAWING

JOB NO. : ESP24075	DRAWN BY:- IH
ELEMENT NO. : PW-GF-01	SHEET SIZE:- A3
DWG. NO. : PW-GF-01(M2)	REV.NO:- 0
SCALE : As indicated	LEVEL. : GF