




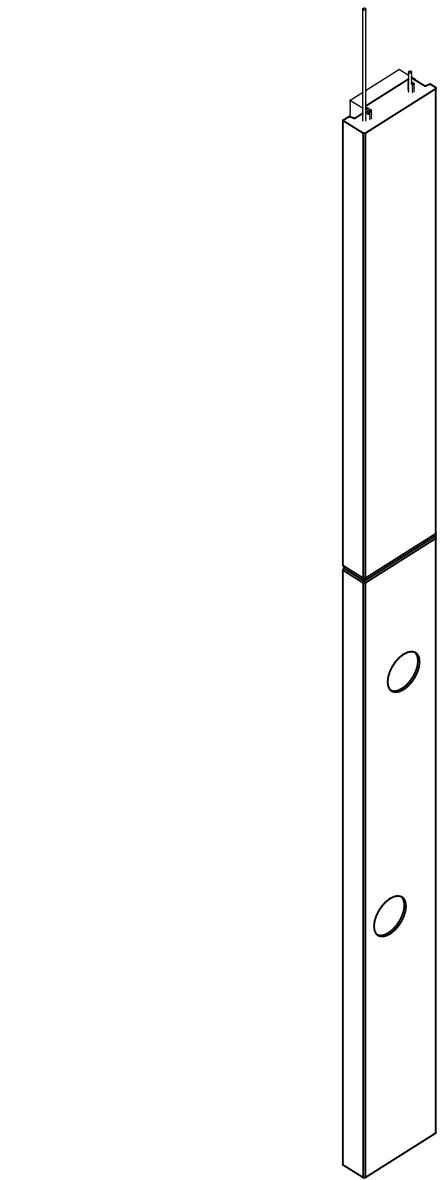


3 3D VIEW

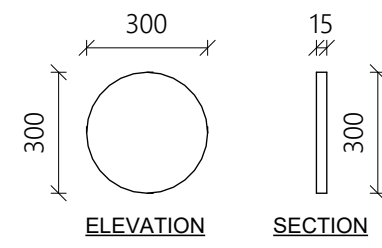


RECESS DETAIL

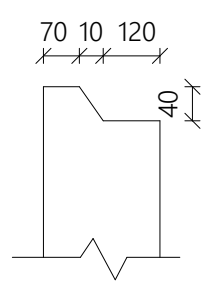


TOP NOTCH DETAIL

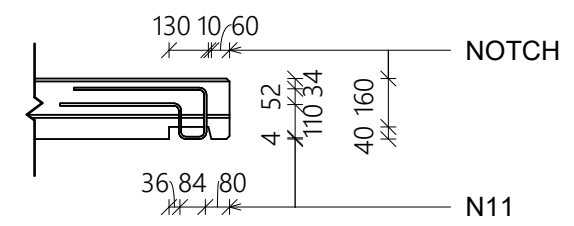


NOTCH DETAIL

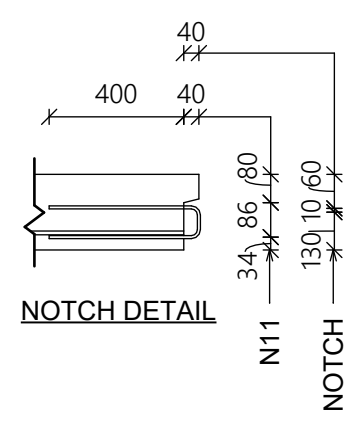

NOTCH DETAIL

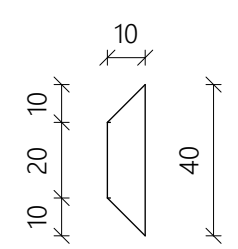

TYPICAL GROOVE DETAIL

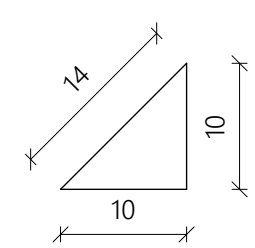

TYPICAL CHAMFER DETAIL

PROJECT -:
MF FACTORY

GENERAL NOTES:

GRADE OF CONCRETE

- M40

GRADE OF STEEL

- Fe500

STRIPPING STRENGTH

- M20

COVER

WALL

- 30mm

CORBEL

- 25mm

ALL DIMENSIONS ARE IN MM

LEGENDS:

ERECTION MARK

-

MOULD FACE

-

CONTRACTOR -:

VME Precast Products

Arihant Esta, 2g2, 2nd floor,
No.370, Church Road, Mogappair East,
Chennai-600037.
Tel:+91- 98400 - 41400 / 90802 - 22066

STRUCTURAL CONSULTANT -:

ES STRUCTURAL CONSULTANT
B167, 12th cross street, Jawahar Nagar,
Palayamkottai, Tirunelveli-627007
Cell No: +91 9865803764

0	26-07-25	FOR APPROVAL	PK	PRC
Rev	Date	Description	Chkd	Appd.
REVISION SCHEDULE				

DRAWING TITLE -:

PW-GF-02-MOULD DRAWING

JOB NO. : ESP24075	DRAWN BY:- IH
ELEMENT NO. : PW-GF-02	SHEET SIZE:- A3
DWG. NO. : PW-GF-02(M2)	REV.NO:- 0
SCALE : As indicated	LEVEL. : GF