

PROJECT -:
MF FACTORY

GENERAL NOTES:

GRADE OF CONCRETE	- M40
GRADE OF STEEL	- Fe500
STRIPPING STRENGTH	- M20

COVER

WALL	- 30mm
CORBEL	- 25mm

ALL DIMENSIONS ARE IN MM

LEGENDS:

ERECTION MARK	-	
MOULD FACE	-	

CONTRACTOR -:

VME Precast Products

 Arihant Esta, 2g2, 2nd floor,
No.370, Church Road, Mogappair East,
Chennai-600037.
Tel:+91- 98400 - 41400 / 90802 - 22066

STRUCTURAL CONSULTANT -:

 **ES STRUCTURAL CONSULTANT**
B167, 12th cross street, Jawahar Nagar,
Palayamkottai, Tirunelveli-627007
Cell No: +91 9865803764


0	23-07-25	FOR APPROVAL	PK	PRC
Rev	Date	Description	Chkd	Appd.

REVISION SCHEDULE


DRAWING TITLE -:

PW-GF-05-REINF DRAWING


JOB NO. : ESP24075	DRAWN BY:- IH
ELEMENT NO. : PW-GF-05	SHEET SIZE:- A3
DWG. NO. : PW-GF-05(R2)	REV.NO:- 0
SCALE : As indicated	LEVEL. :

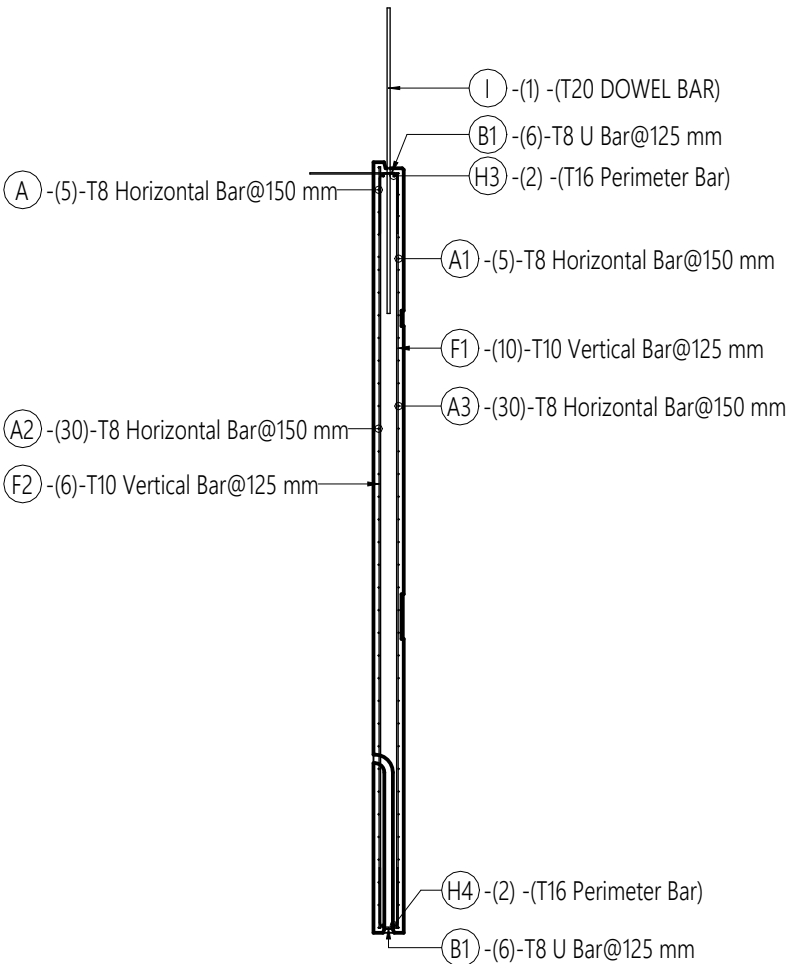


2 SECTION (REINF)
1 : 50

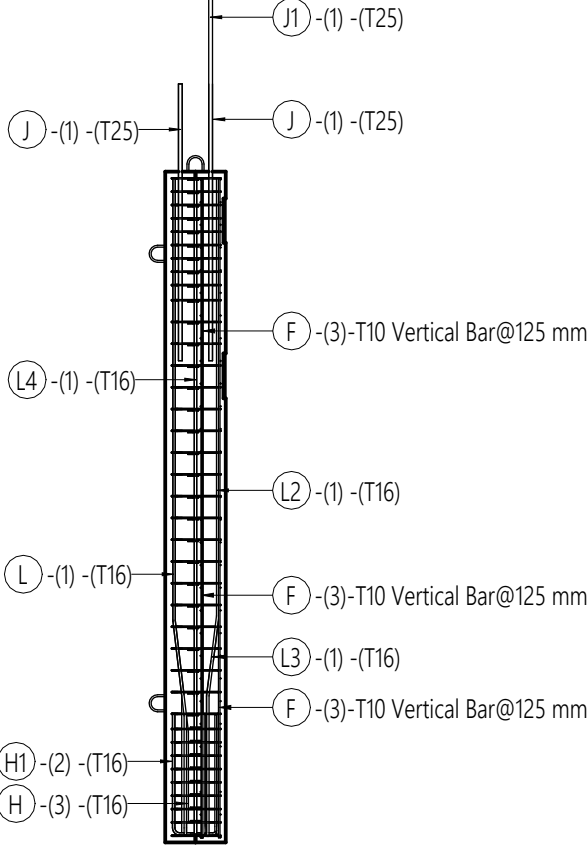


3 SECTION (REINF)
1 : 50

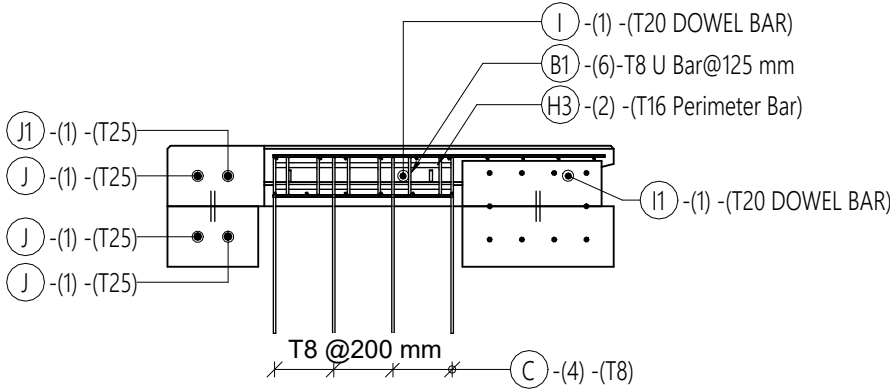

4 SECTION (REINF)
1 : 25

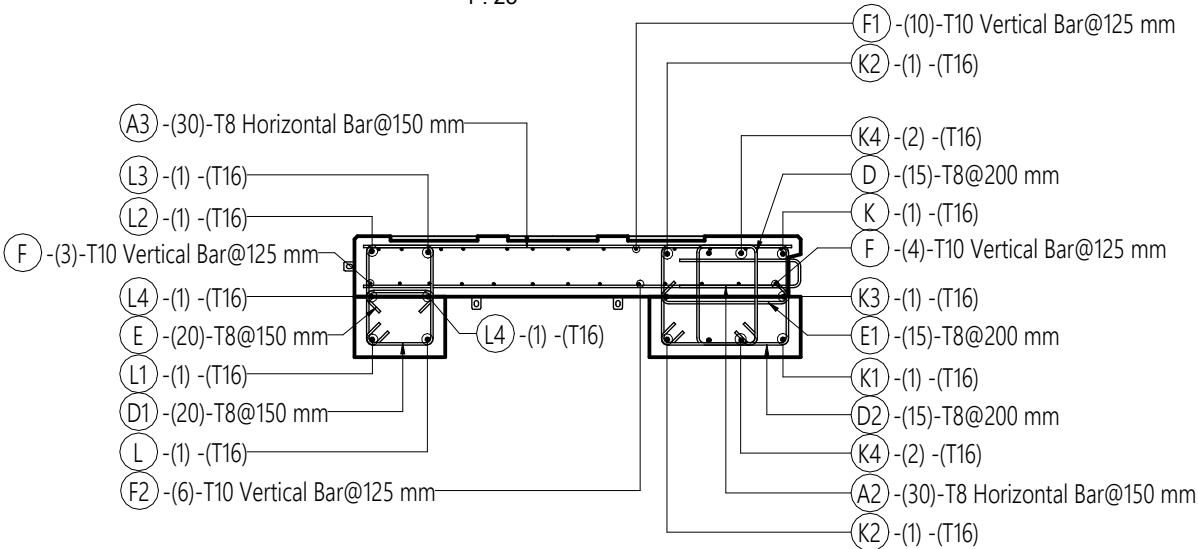

5 SECTION (REINF)
1 : 25

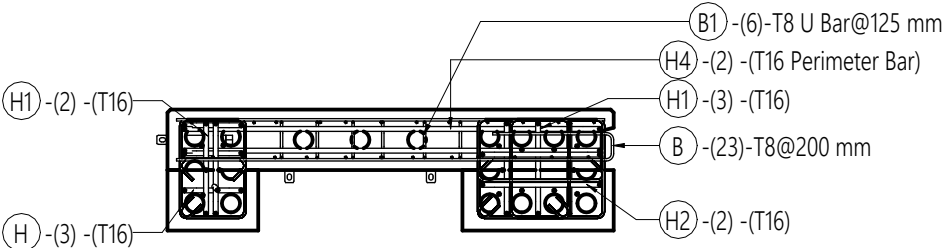

6 SECTION (REINF)
1 : 25