
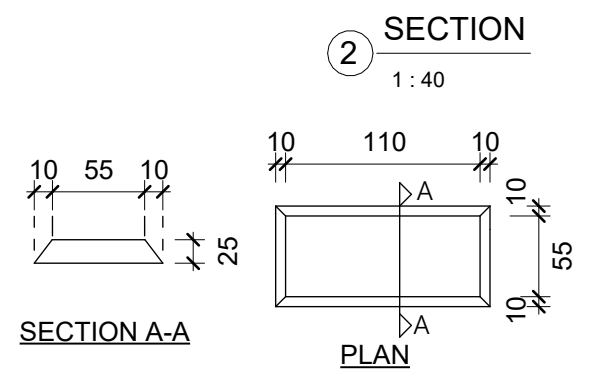
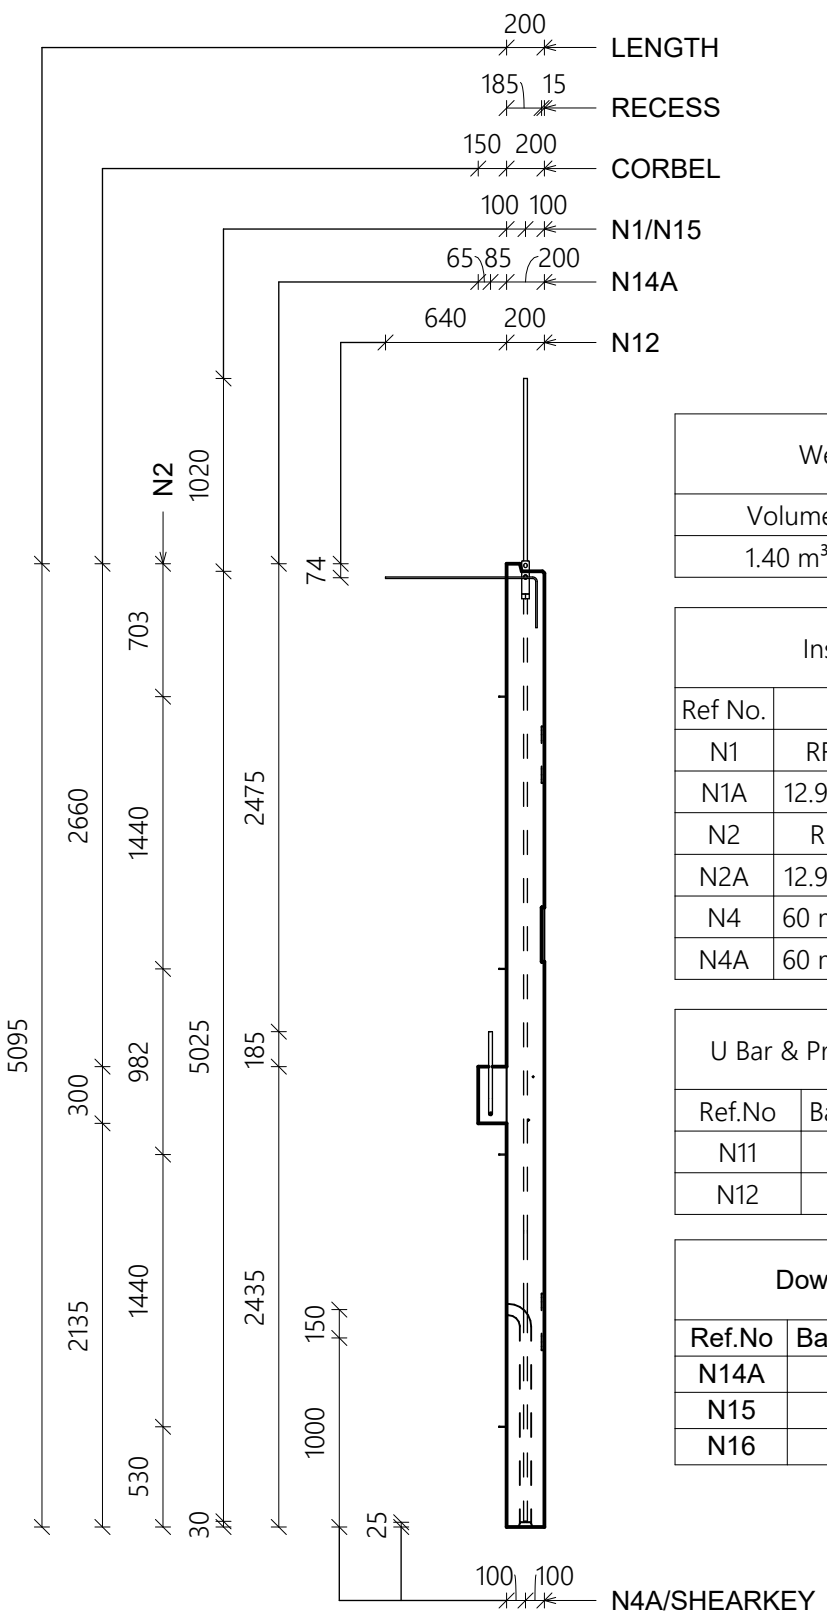
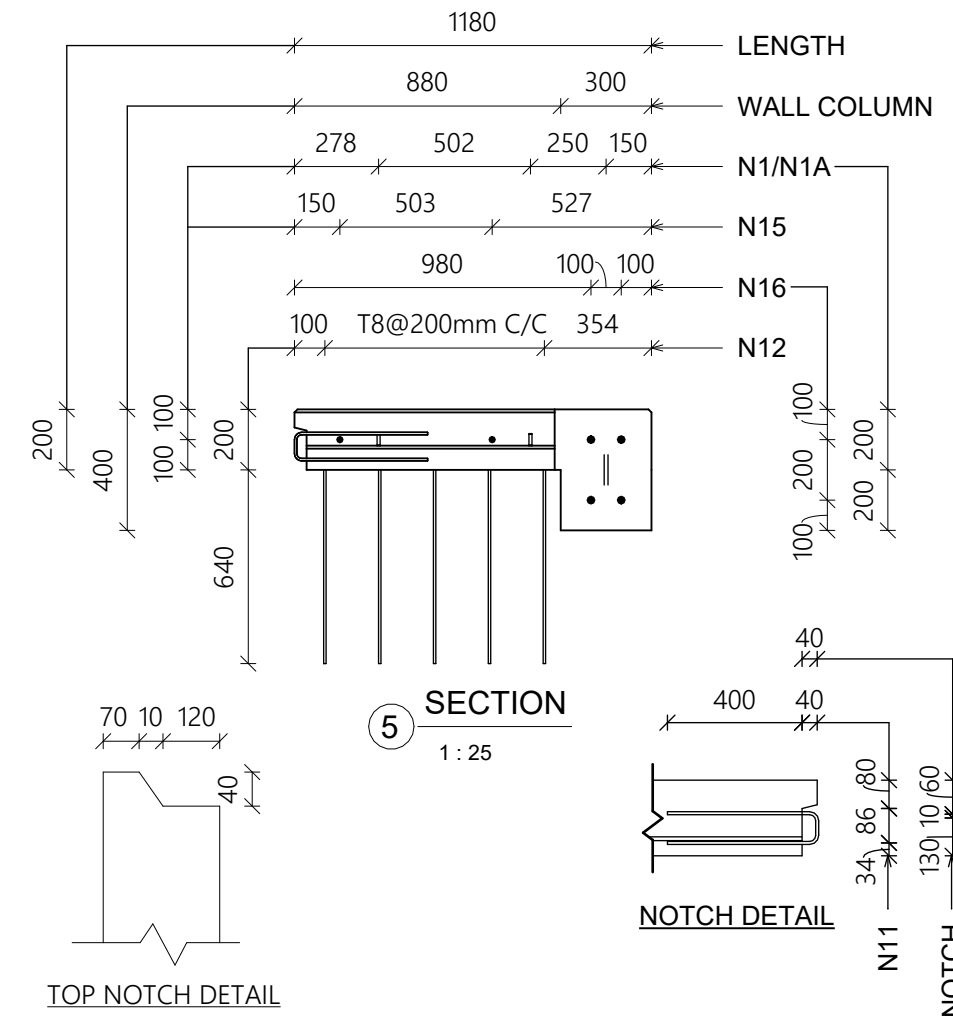
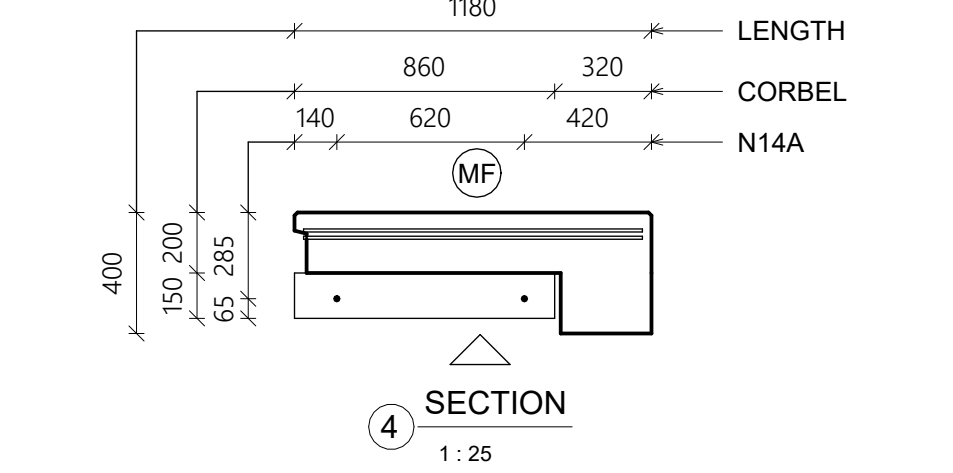
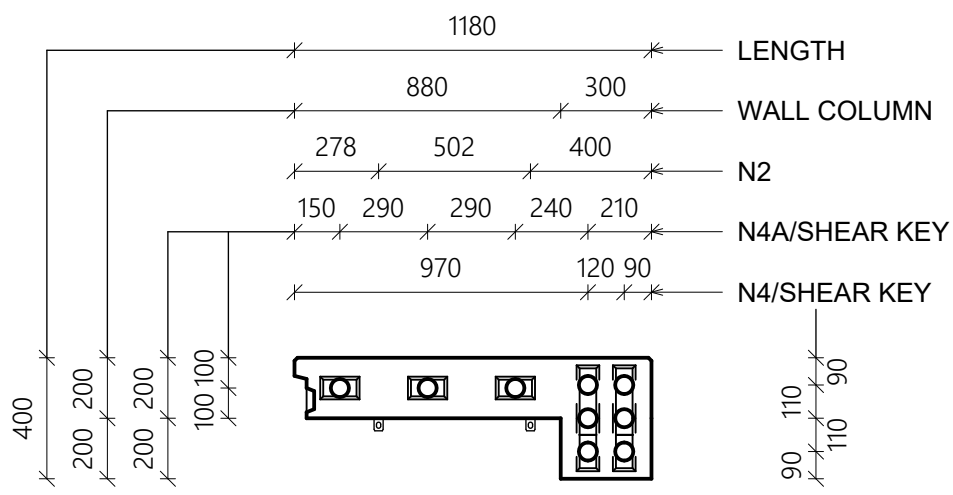


| Weight Schedule |            |
|-----------------|------------|
| Volume          | Weight     |
| 1.40 m³         | 3492.89 kg |

| Insert Schedule |                      |       |
|-----------------|----------------------|-------|
| Ref No.         | Type                 | Count |
| N1              | RR-SA-3.0-200        | 2     |
| N1A             | 12.9Ø Lifting insert | 1     |
| N2              | RR-SA-0.7-110        | 8     |
| N2A             | 12.9Ø Lifting insert | 2     |
| N4              | 60 mm dowel tube     | 5     |
| N4A             | 60 mm dowel tube     | 4     |

| U Bar & Projecting Bar Schedule |              |          |
|---------------------------------|--------------|----------|
| Ref.No                          | Bar Diameter | Quantity |
| N11                             | 8 mm         | 25       |
| N12                             | 8 mm         | 5        |

| Dowel Bar Schedule |              |       |
|--------------------|--------------|-------|
| Ref.No             | Bar Diameter | Count |
| N14A               | 20 mm        | 1     |
| N15                | 20 mm        | 2     |
| N16                | 25 mm        | 4     |

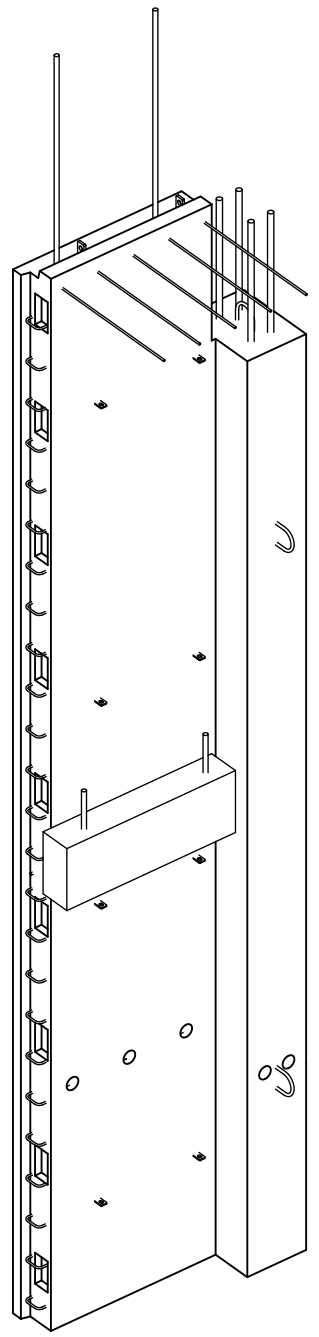

## PROJECT -: MF FACTORY

### GENERAL NOTES:

- GRADE OF CONCRETE - M40
- GRADE OF STEEL - Fe500
- STRIPPING STRENGTH - M20
- COVER**
  - WALL - 30mm
  - COLUMN - 40mm
  - CORBEL - 25mm
- ALL DIMENSIONS ARE IN MM

### LEGENDS:

- ERECTION MARK -
- MOULD FACE -

### CONTRACTOR -:

**VME Precast Products**  
Arihant Esta, 2g2, 2<sup>nd</sup> floor,  
No.370, Church Road, Mogappair East,  
Chennai-600037.  
Tel:+91- 98400 - 41400 / 90802 - 22066

### STRUCTURAL CONSULTANT -:

**ES STRUCTURAL CONSULTANT**  
B167, 12th cross street, Jawahar Nagar,  
Palayamkottai, Tirunelveli-627007  
Cell No: +91 9865803764

| 0   | 23-07-25 | FOR APPROVAL | PK   | PRC   |
|-----|----------|--------------|------|-------|
| Rev | Date     | Description  | Chkd | Appd. |

| REVISION SCHEDULE |  |  |  |  |
|-------------------|--|--|--|--|
|-------------------|--|--|--|--|

### DRAWING TITLE -:

PW-GF-06-MOULD DRAWING

|                         |                 |
|-------------------------|-----------------|
| JOB NO. : ESP24075      | DRAWN BY:- IH   |
| ELEMENT NO. : PW-GF-06  | SHEET SIZE:- A3 |
| DWG. NO. : PW-GF-06(M2) | REV.NO:- 0      |
| SCALE : As indicated    | LEVEL. : GF     |