
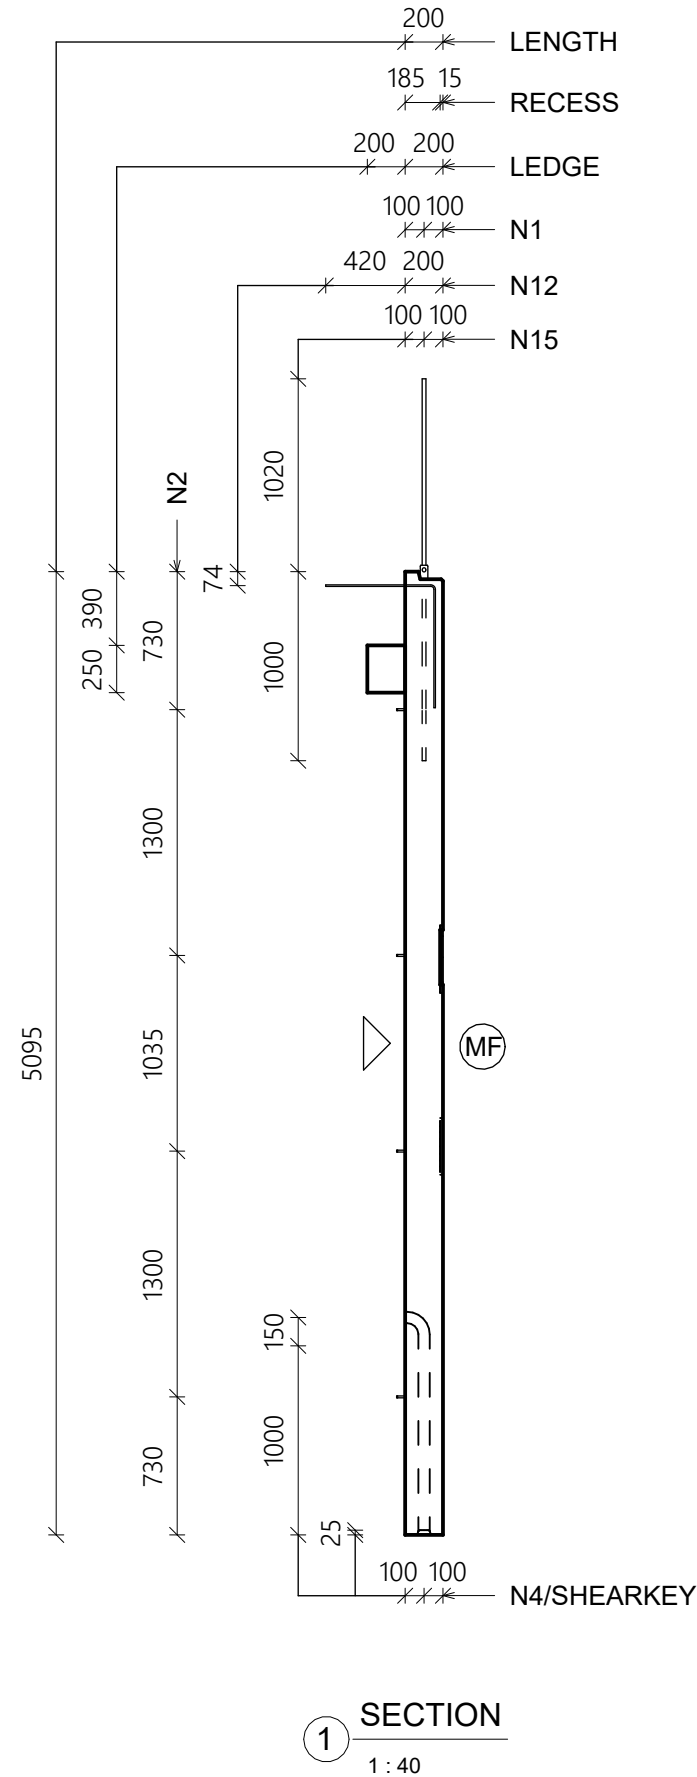


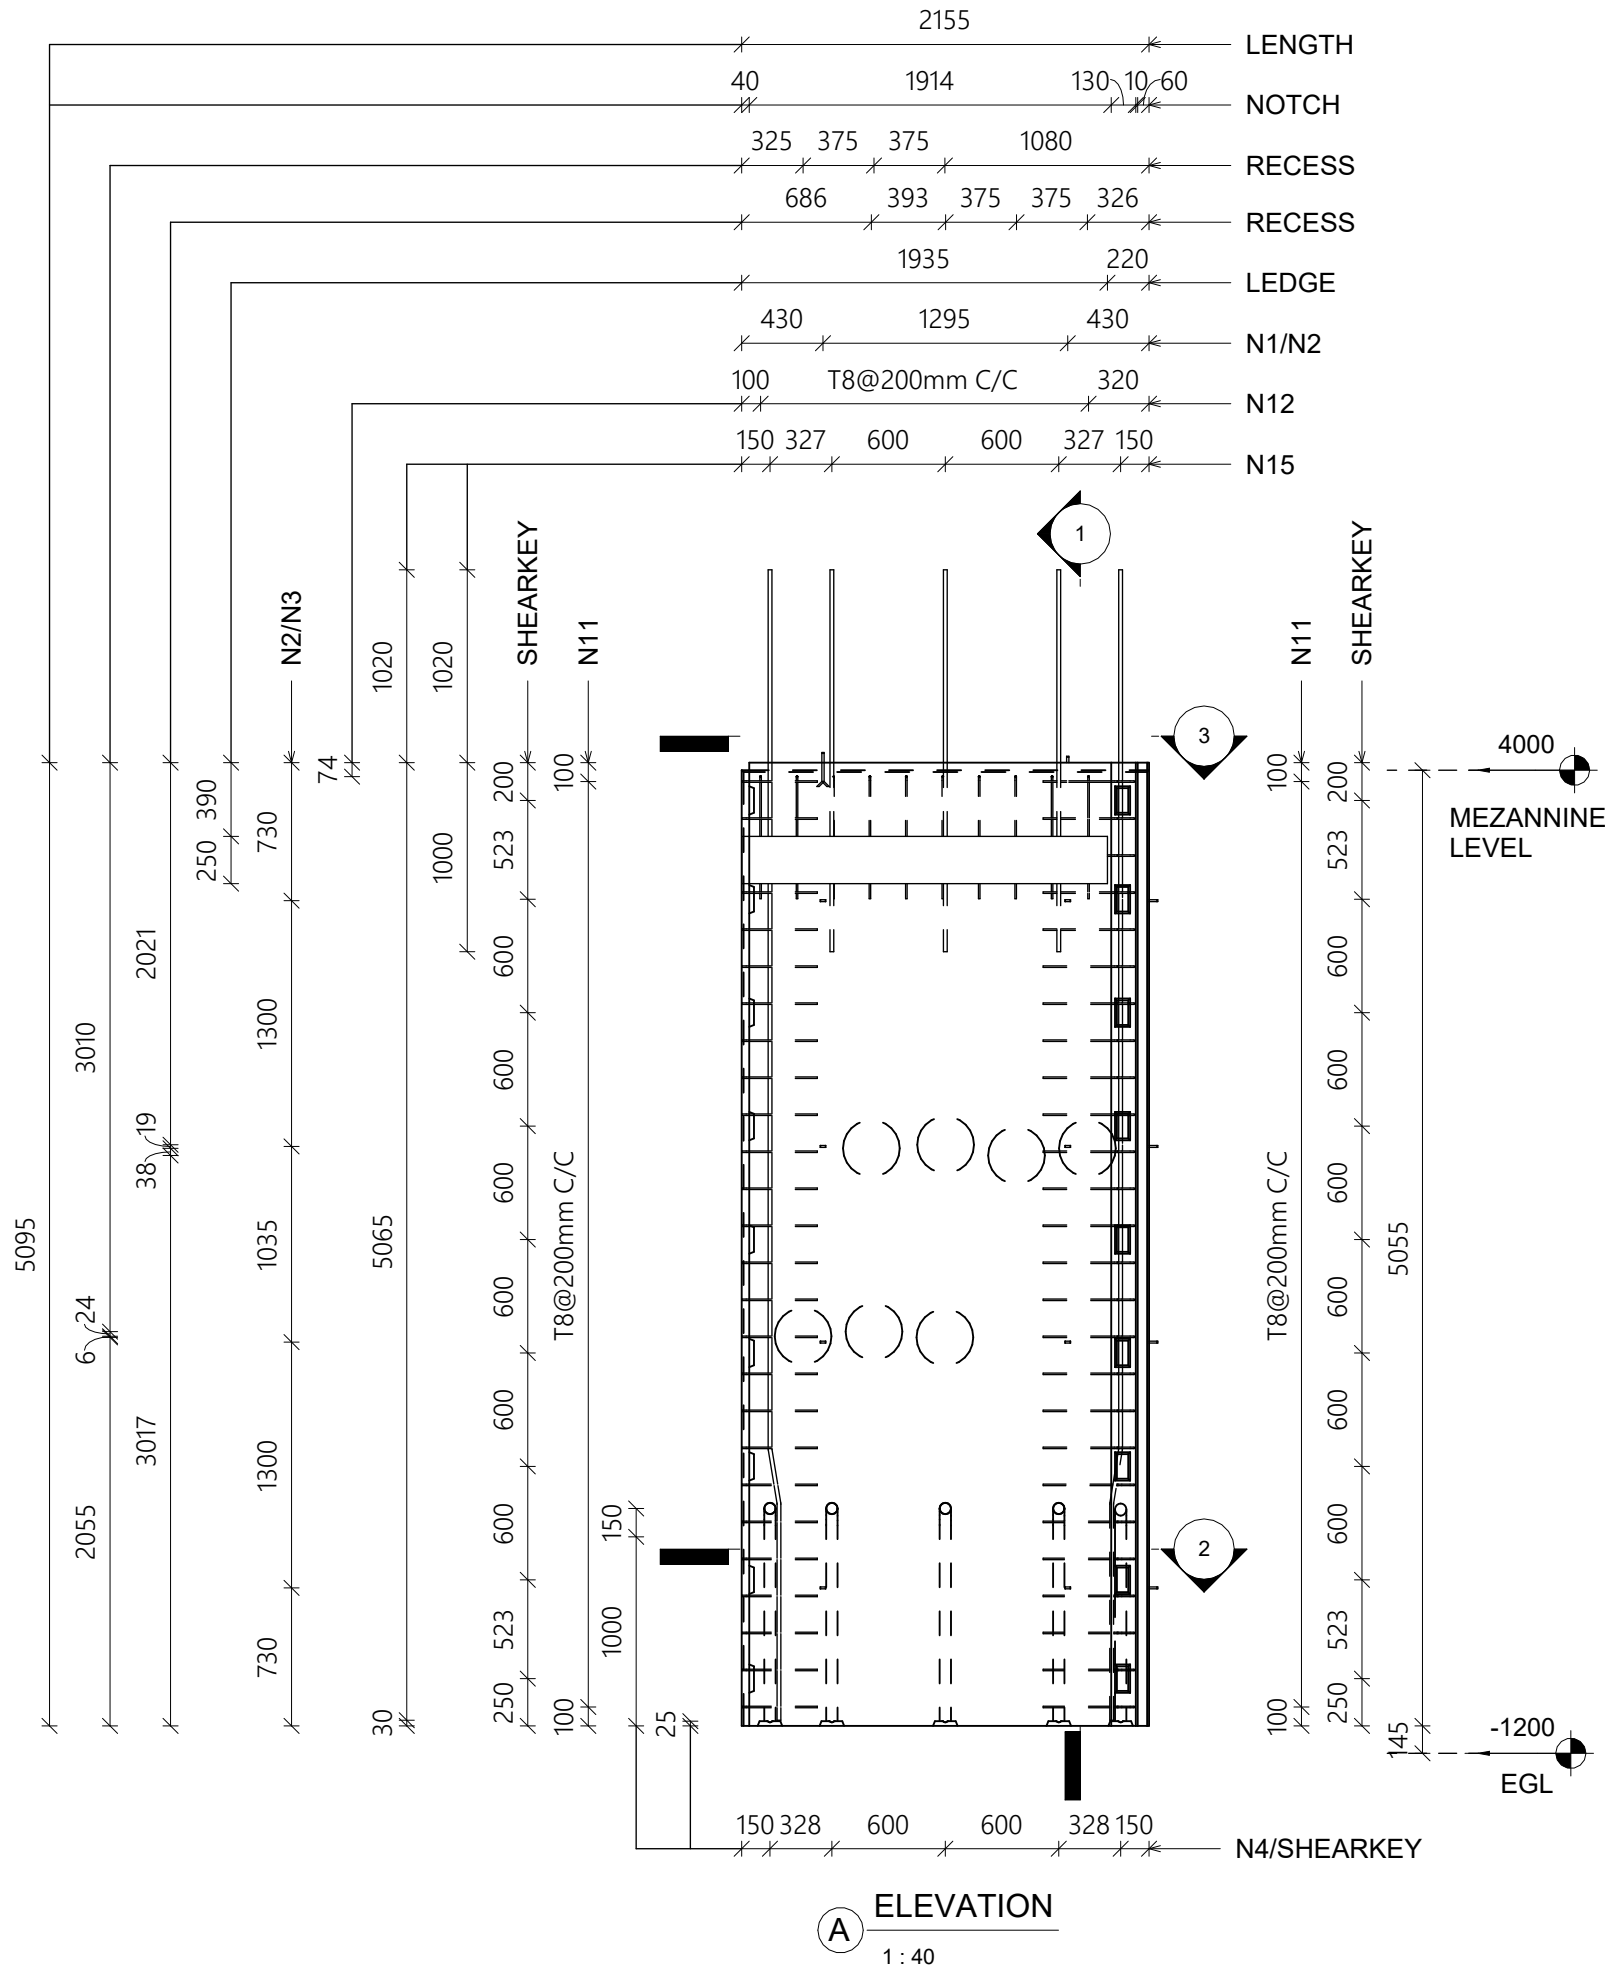

PROJECT :-  
MF FACTORY

GENERAL NOTES:

- GRADE OF CONCRETE - M40  
GRADE OF STEEL - Fe500  
STRIPPING STRENGTH - M20
- COVER**
- WALL - 30mm  
CORBEL - 25mm
- ALL DIMENSIONS ARE IN MM

LEGENDS:

- ERECTION MARK -
- MOULD FACE -

CONTRACTOR :-

**VME Precast Products**  
Arihant Esta, 2g2, 2<sup>nd</sup> floor,  
No.370, Church Road, Mogappair East,  
Chennai-600037.  
Tel:+91- 98400 - 41400 / 90802 - 22066

STRUCTURAL CONSULTANT :-

**ES STRUCTURAL CONSULTANT**  
B167, 12th cross street, Jawahar Nagar,  
Palayamkottai, Tirunelveli-627007  
Cell No: +91 9865803764

|     |          |              |      |       |
|-----|----------|--------------|------|-------|
| 1   | 26-05-25 | FOR APPROVAL | PK   | PRC   |
| 0   | 22-04-25 | FOR APPROVAL | PK   | PRC   |
| Rev | Date     | Description  | Chkd | Appd. |

|                   |
|-------------------|
| REVISION SCHEDULE |
|-------------------|

DRAWING TITLE :-

PW-GF-07-MOULD DRAWING

|                         |                 |
|-------------------------|-----------------|
| JOB NO. : ESP24075      | DRAWN BY:- AR   |
| ELEMENT NO. : PW-GF-07  | SHEET SIZE:- A3 |
| DWG. NO. : PW-GF-07(M1) | REV.NO:- 1      |
| SCALE : 1 : 40          | LEVEL. : GF     |