
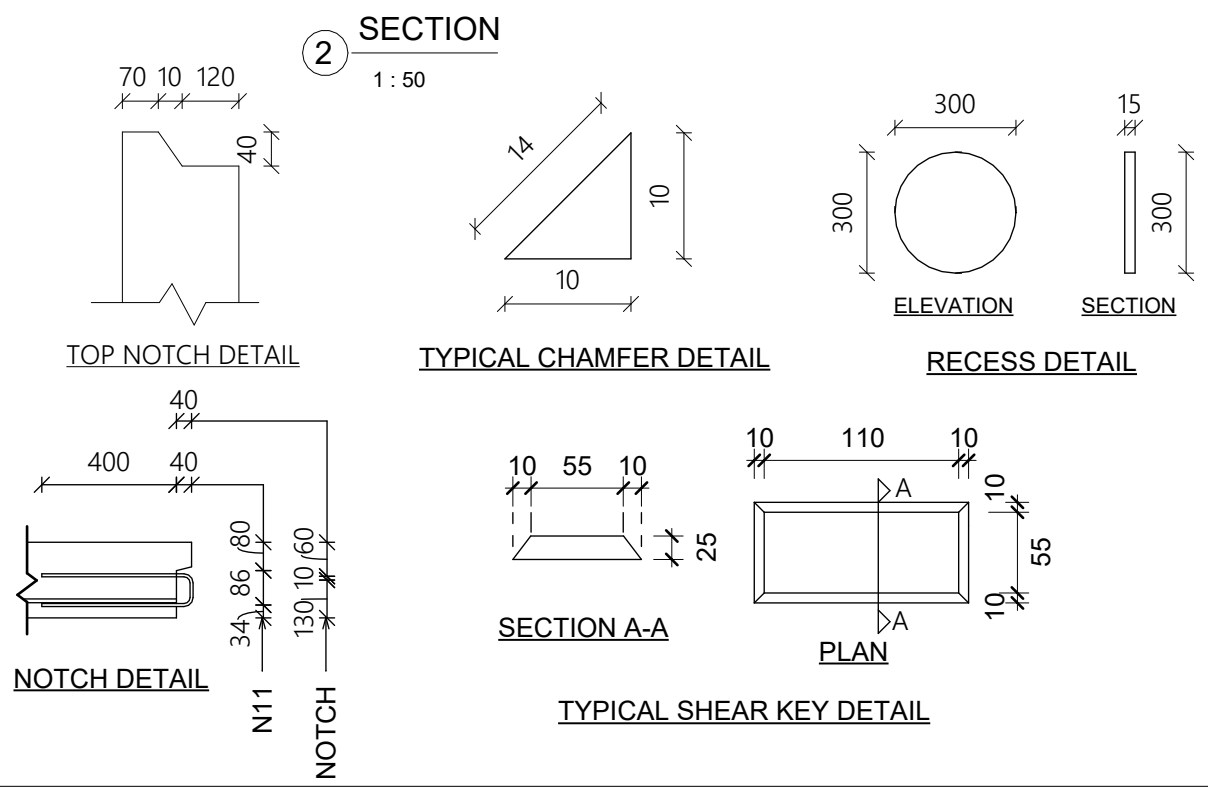
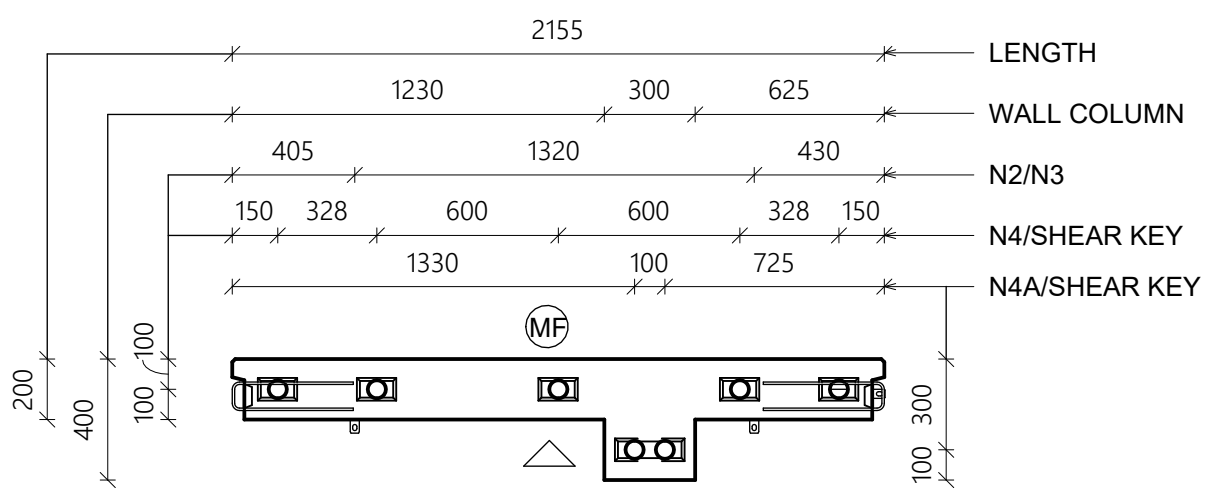
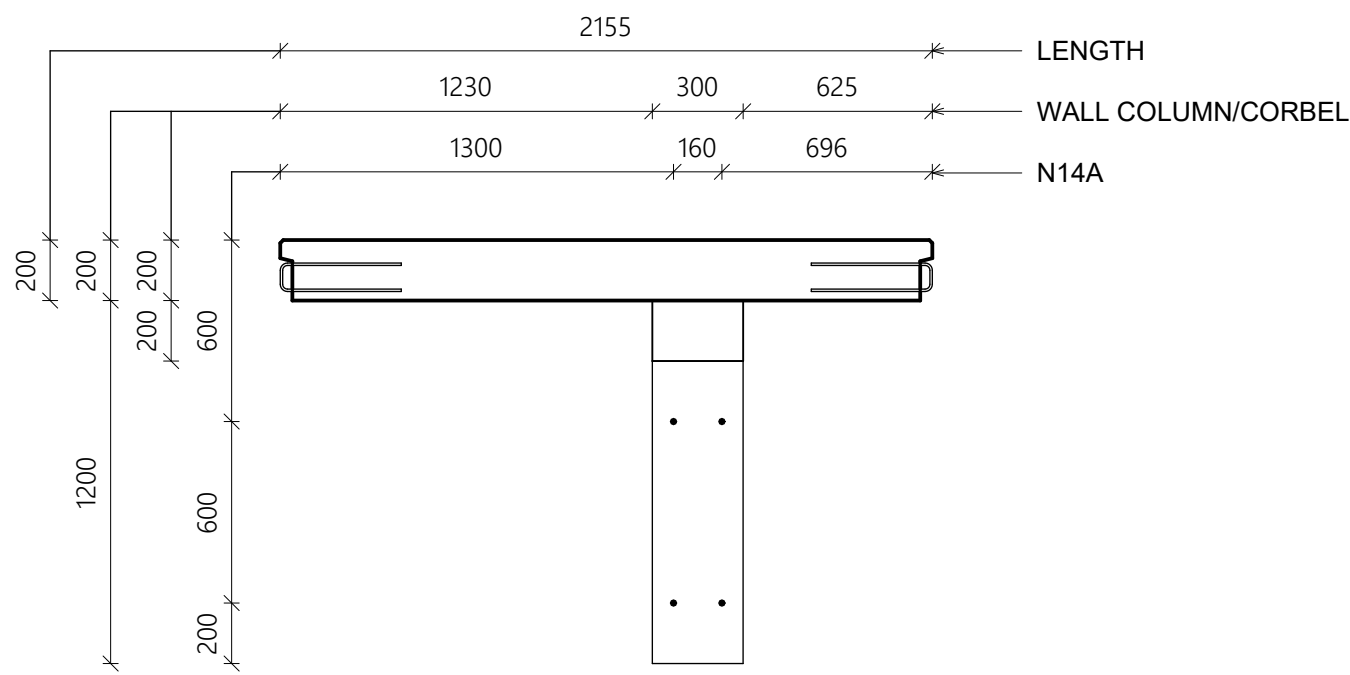
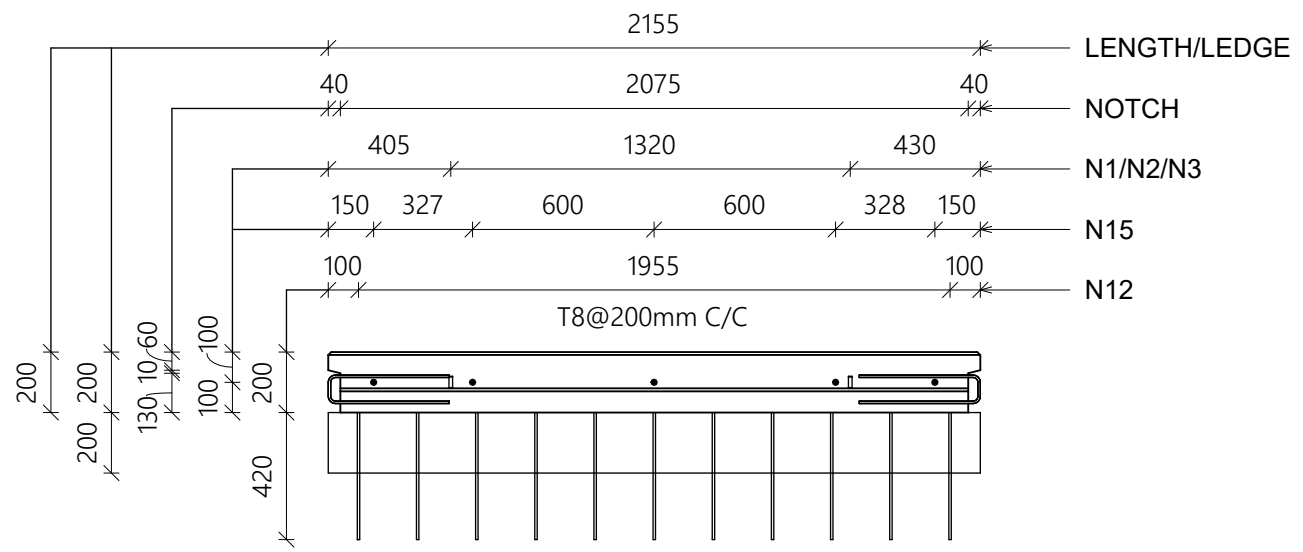
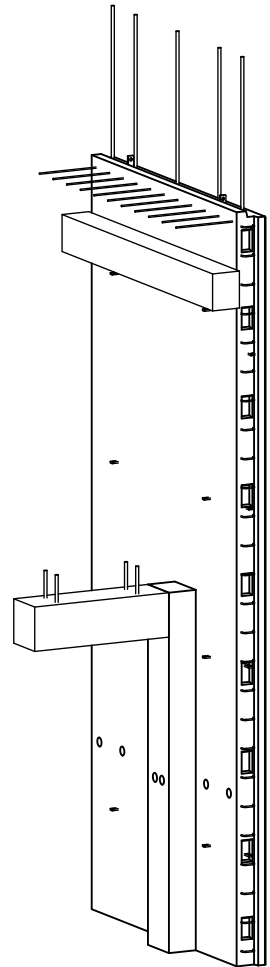


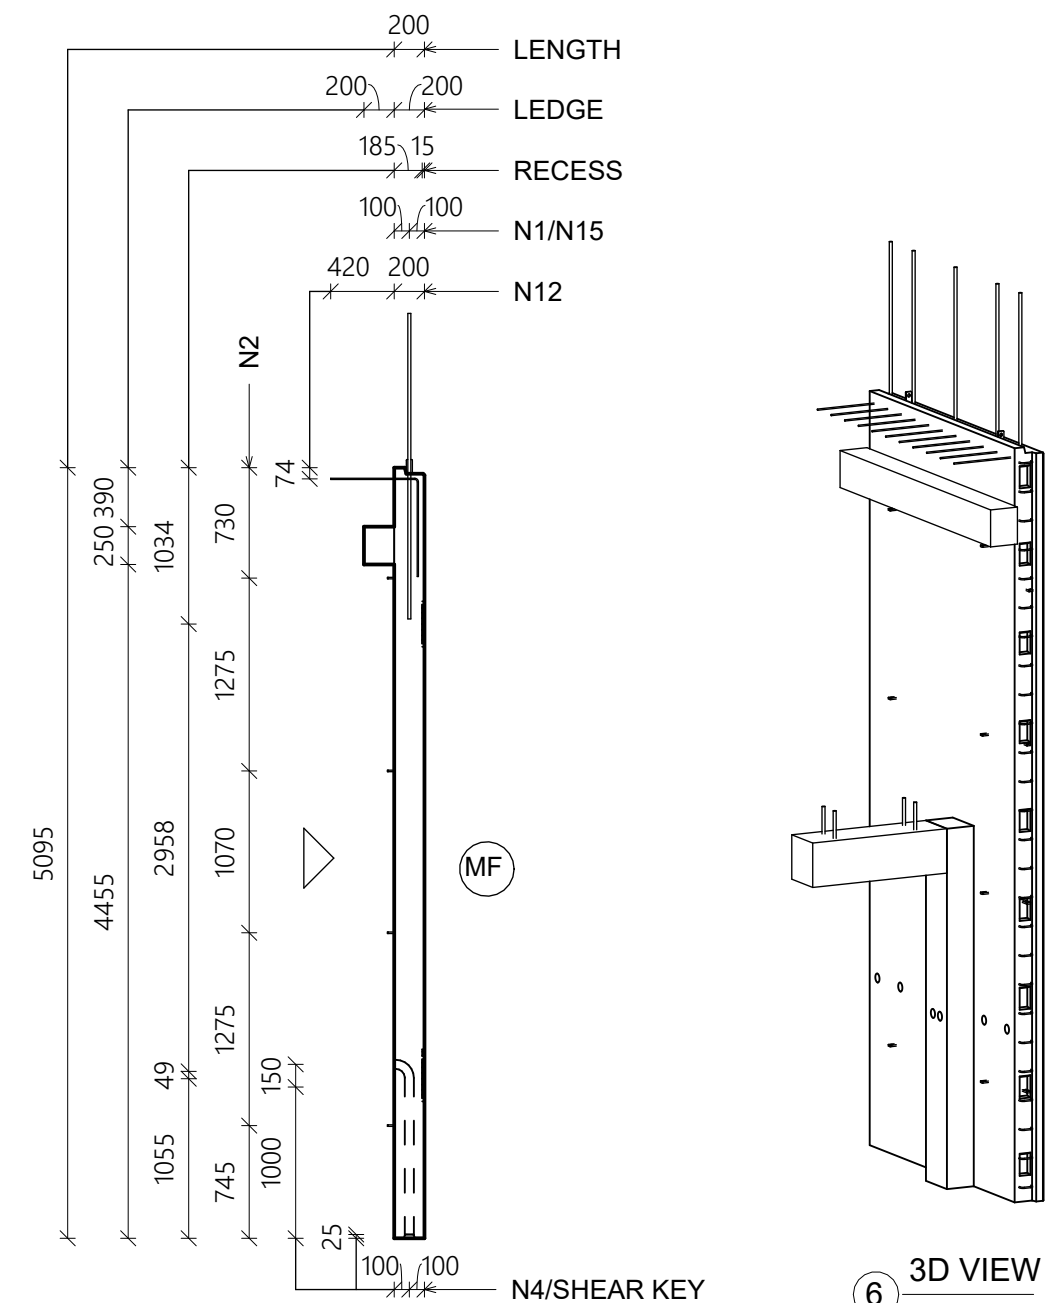

PROJECT :-
MF FACTORY

GENERAL NOTES:

GRADE OF CONCRETE - M40
GRADE OF STEEL - Fe500
STRIPPING STRENGTH - M20
COVER
WALL - 30mm
CORBEL - 25mm
ALL DIMENSIONS ARE IN MM

LEGENDS:
ERECTION MARK -
MOULD FACE -

CONTRACTOR :-
VME Precast Products
Arihant Esta, 2g2, 2nd floor,
No.370, Church Road, Mogappair East,
Chennai-600037.
Tel:+91- 98400 - 41400 / 90802 - 22066

STRUCTURAL CONSULTANT :-
ES STRUCTURAL CONSULTANT
B167, 12th cross street, Jawahar Nagar,
Palayamkottai, Tirunelveli-627007
Cell No: +91 9865803764

0	14-06-25	FOR APPROVAL	PK	PRC
Rev	Date	Description	Chkd	Appd.
REVISION SCHEDULE				

DRAWING TITLE :-
PW-GF-08-MOULD DRAWING

JOB NO. : ESP24075
ELEMENT NO. : PW-GF-08
DWG. NO. : PW-GF-08(M2)
SCALE : As indicated

DRAWN BY:- IH
SHEET SIZE:- A3
REV.NO:- 0
LEVEL. :