
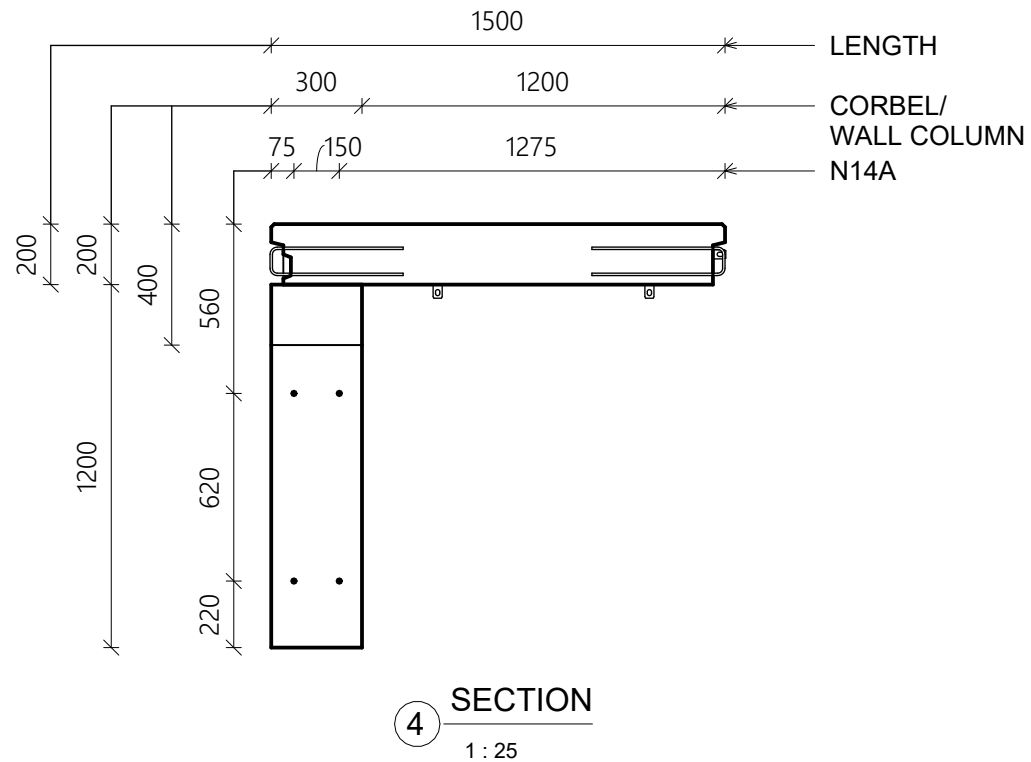
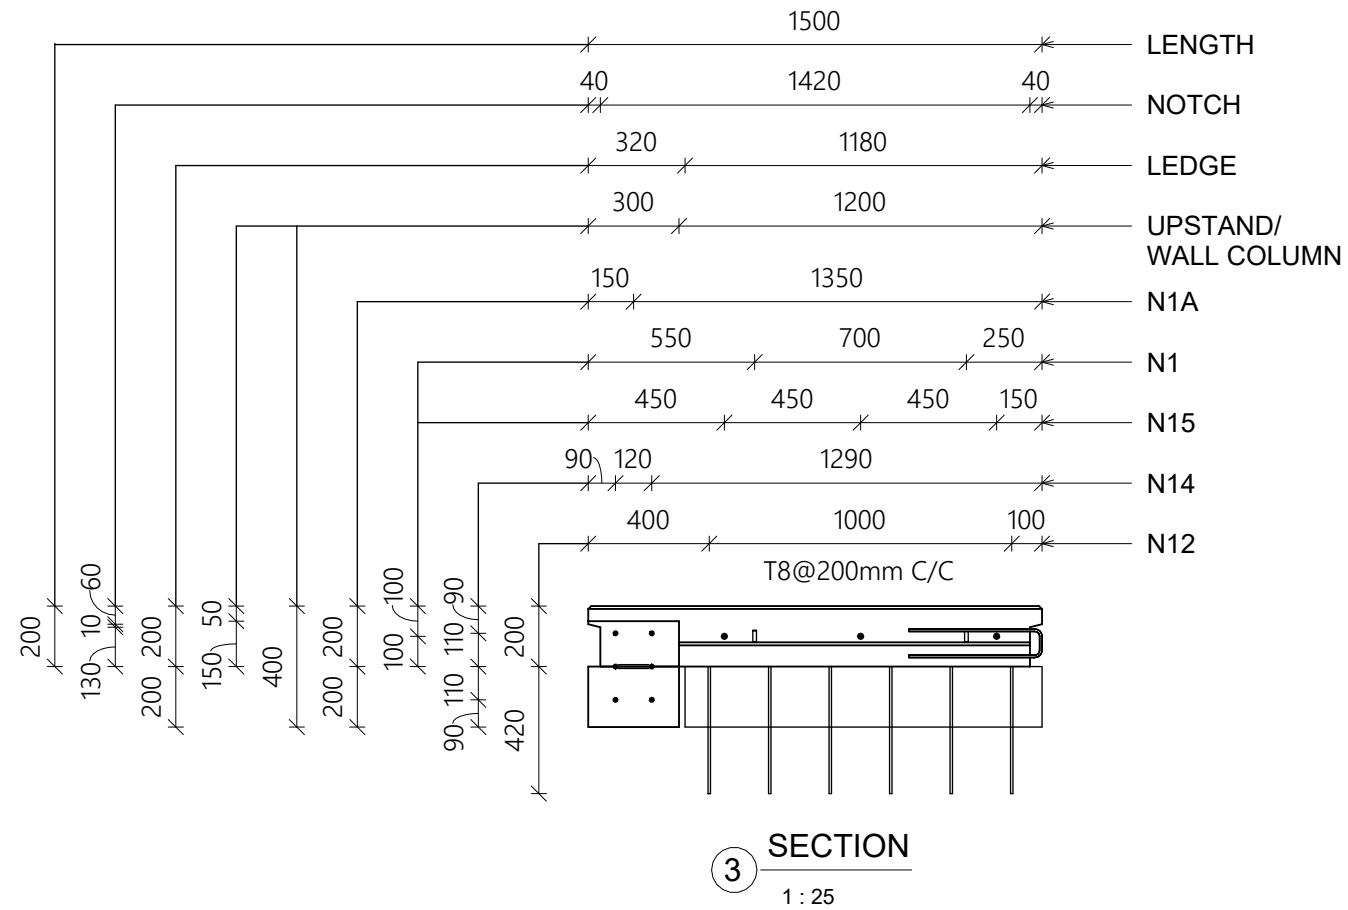


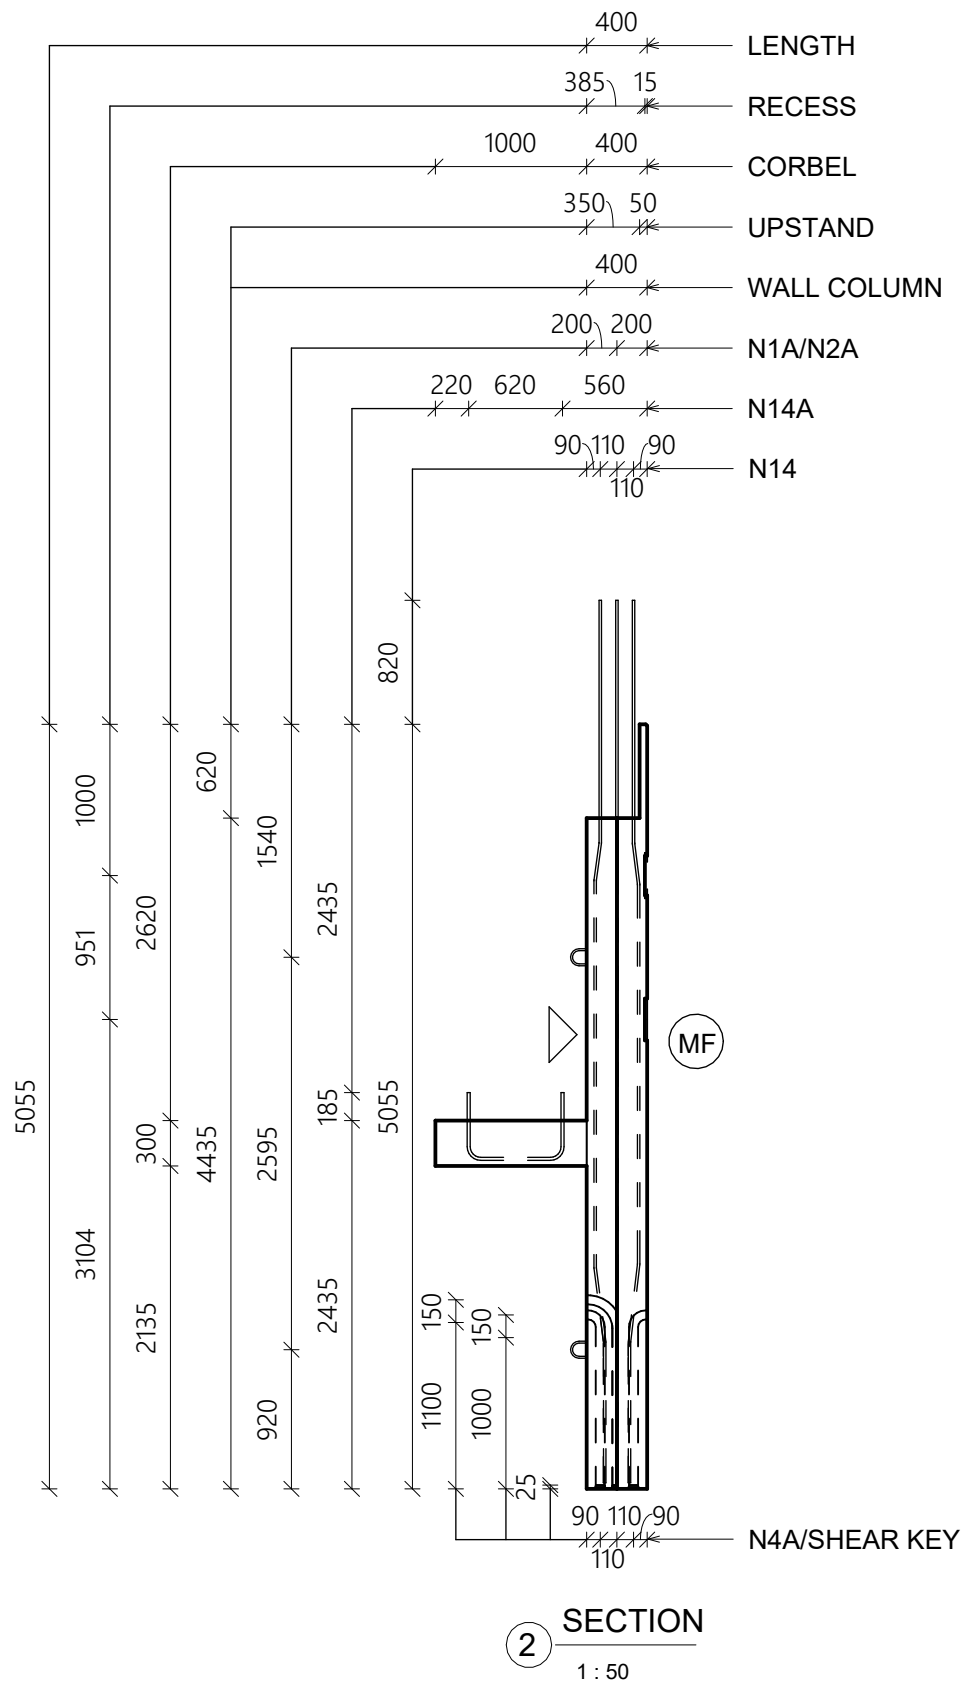

PROJECT -: MF FACTORY

GENERAL NOTES:

- GRADE OF CONCRETE - M40
- GRADE OF STEEL - Fe500
- STRIPPING STRENGTH - M20

COVER

- WALL - 30mm
- CORBEL - 25mm

ALL DIMENSIONS ARE IN MM

LEGENDS:

- ERECTION MARK -
- MOULD FACE -

CONTRACTOR -:

VME Precast Products

Arihant Esta, 2g2, 2nd floor,
No.370, Church Road, Mogappair East,
Chennai-600037.
Tel:+91- 98400 - 41400 / 90802 - 22066

STRUCTURAL CONSULTANT -:

ES STRUCTURAL CONSULTANT
B167, 12th cross street, Jawahar Nagar,
Palayamkottai, Tirunelveli-627007
Cell No: +91 9865803764

0	14-06-25	FOR APPROVAL	PK	PRC
Rev	Date	Description	Chkd	Appd.

REVISION SCHEDULE

DRAWING TITLE -:

PW-GF-09-MOULD DRAWING

JOB NO. : ESP24075	DRAWN BY:- IH
ELEMENT NO. : PW-GF-09	SHEET SIZE:- A3
DWG. NO. : PW-GF-09(M2)	REV.NO:- 0
SCALE : As indicated	LEVEL. :