




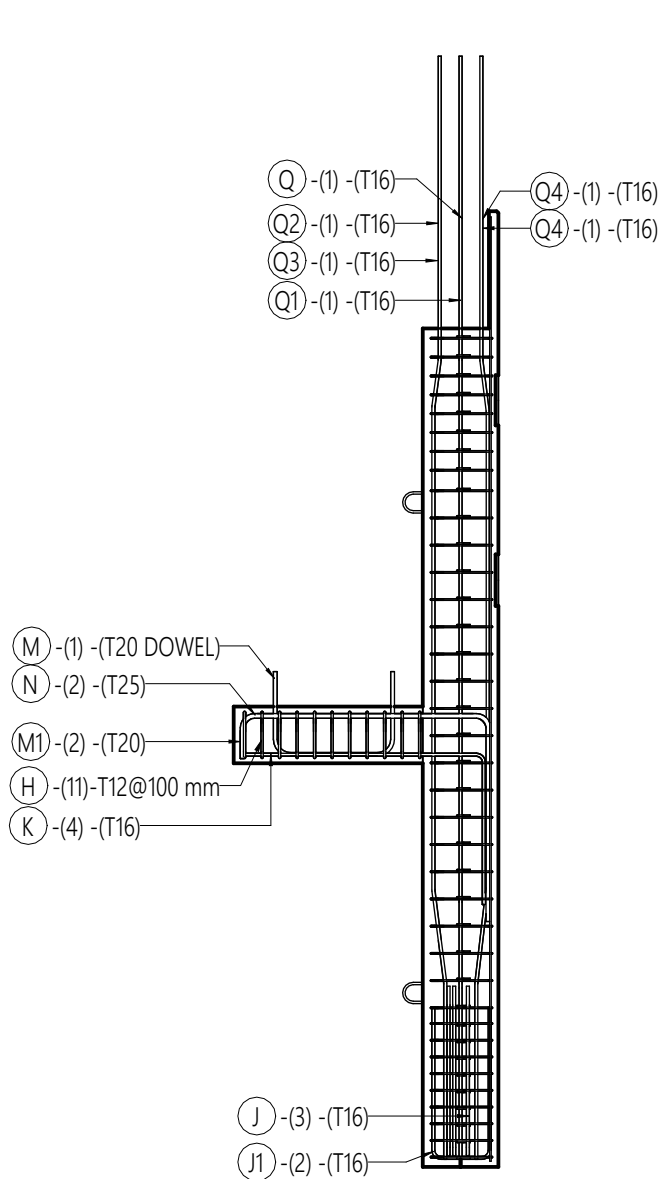


2 SECTION (REINF)
1 : 40

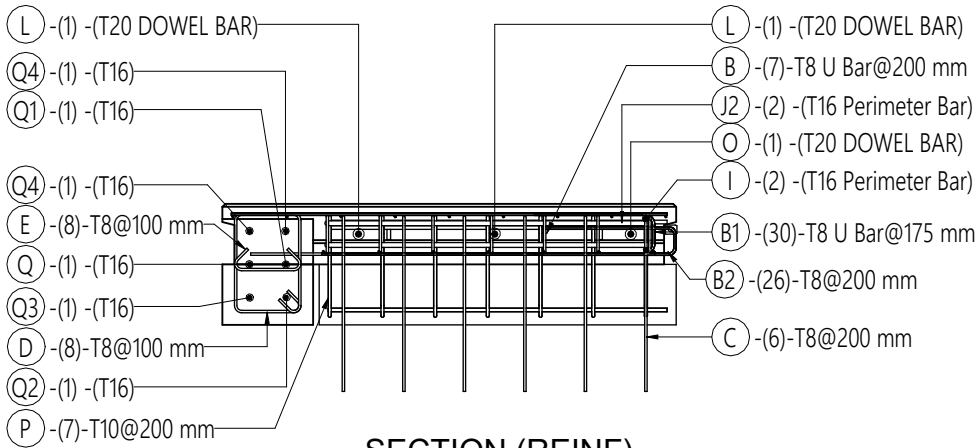

3 SECTION (REINF)
1 : 25

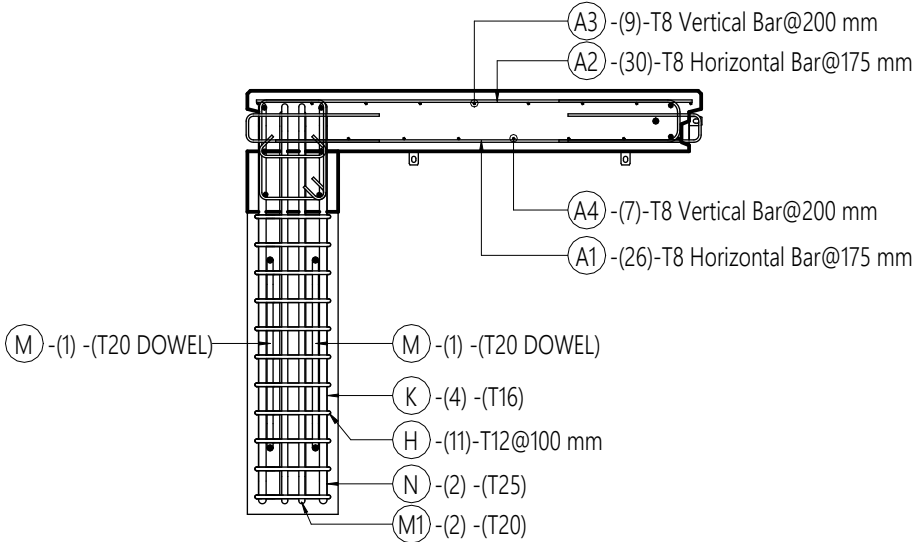

4 SECTION (REINF)
1 : 25

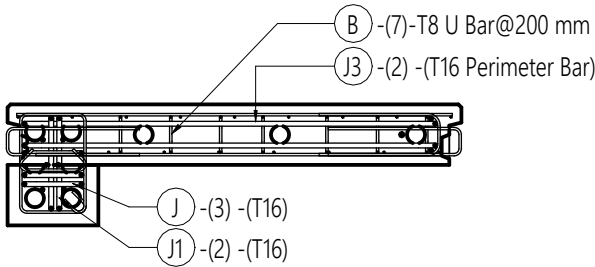

5 SECTION (REINF)
1 : 25

Rebar Shape	Shape Image
M_00	
M_17	
Rebar Shape 9	
M_17A	
26	
M_T1	
M_T10	
REBAR SHAPE 31	

PROJECT -:
MF FACTORY

GENERAL NOTES:

GRADE OF CONCRETE	- M40
GRADE OF STEEL	- Fe500
STRIPPING STRENGTH	- M20
COVER	
WALL	- 30mm
CORBEL	- 25mm
ALL DIMENSIONS ARE IN MM	

LEGENDS:

ERECTION MARK	-	
MOULD FACE	-	

CONTRACTOR -:

VME Precast Products
Arihant Esta, 2g2, 2nd floor,
No.370, Church Road, Mogappair East,
Chennai-600037.
Tel:+91- 98400 - 41400 / 90802 - 22066

STRUCTURAL CONSULTANT -:

ES STRUCTURAL CONSULTANT
B167, 12th cross street, Jawahar Nagar,
Palayamkottai, Tirunelveli-627007
Cell No: +91 9865803764

0	14-06-25	FOR APPROVAL	PK	PRC
Rev	Date	Description	Chkd	Appd.

REVISION SCHEDULE

DRAWING TITLE -:

PW-GF-09-REINF DRAWING

JOB NO. : ESP24075	DRAWN BY:- IH
ELEMENT NO. : PW-GF-09	SHEET SIZE:- A3
DWG. NO. : PW-GF-09(R2)	REV.NO:- 0
SCALE : As indicated	LEVEL. :