



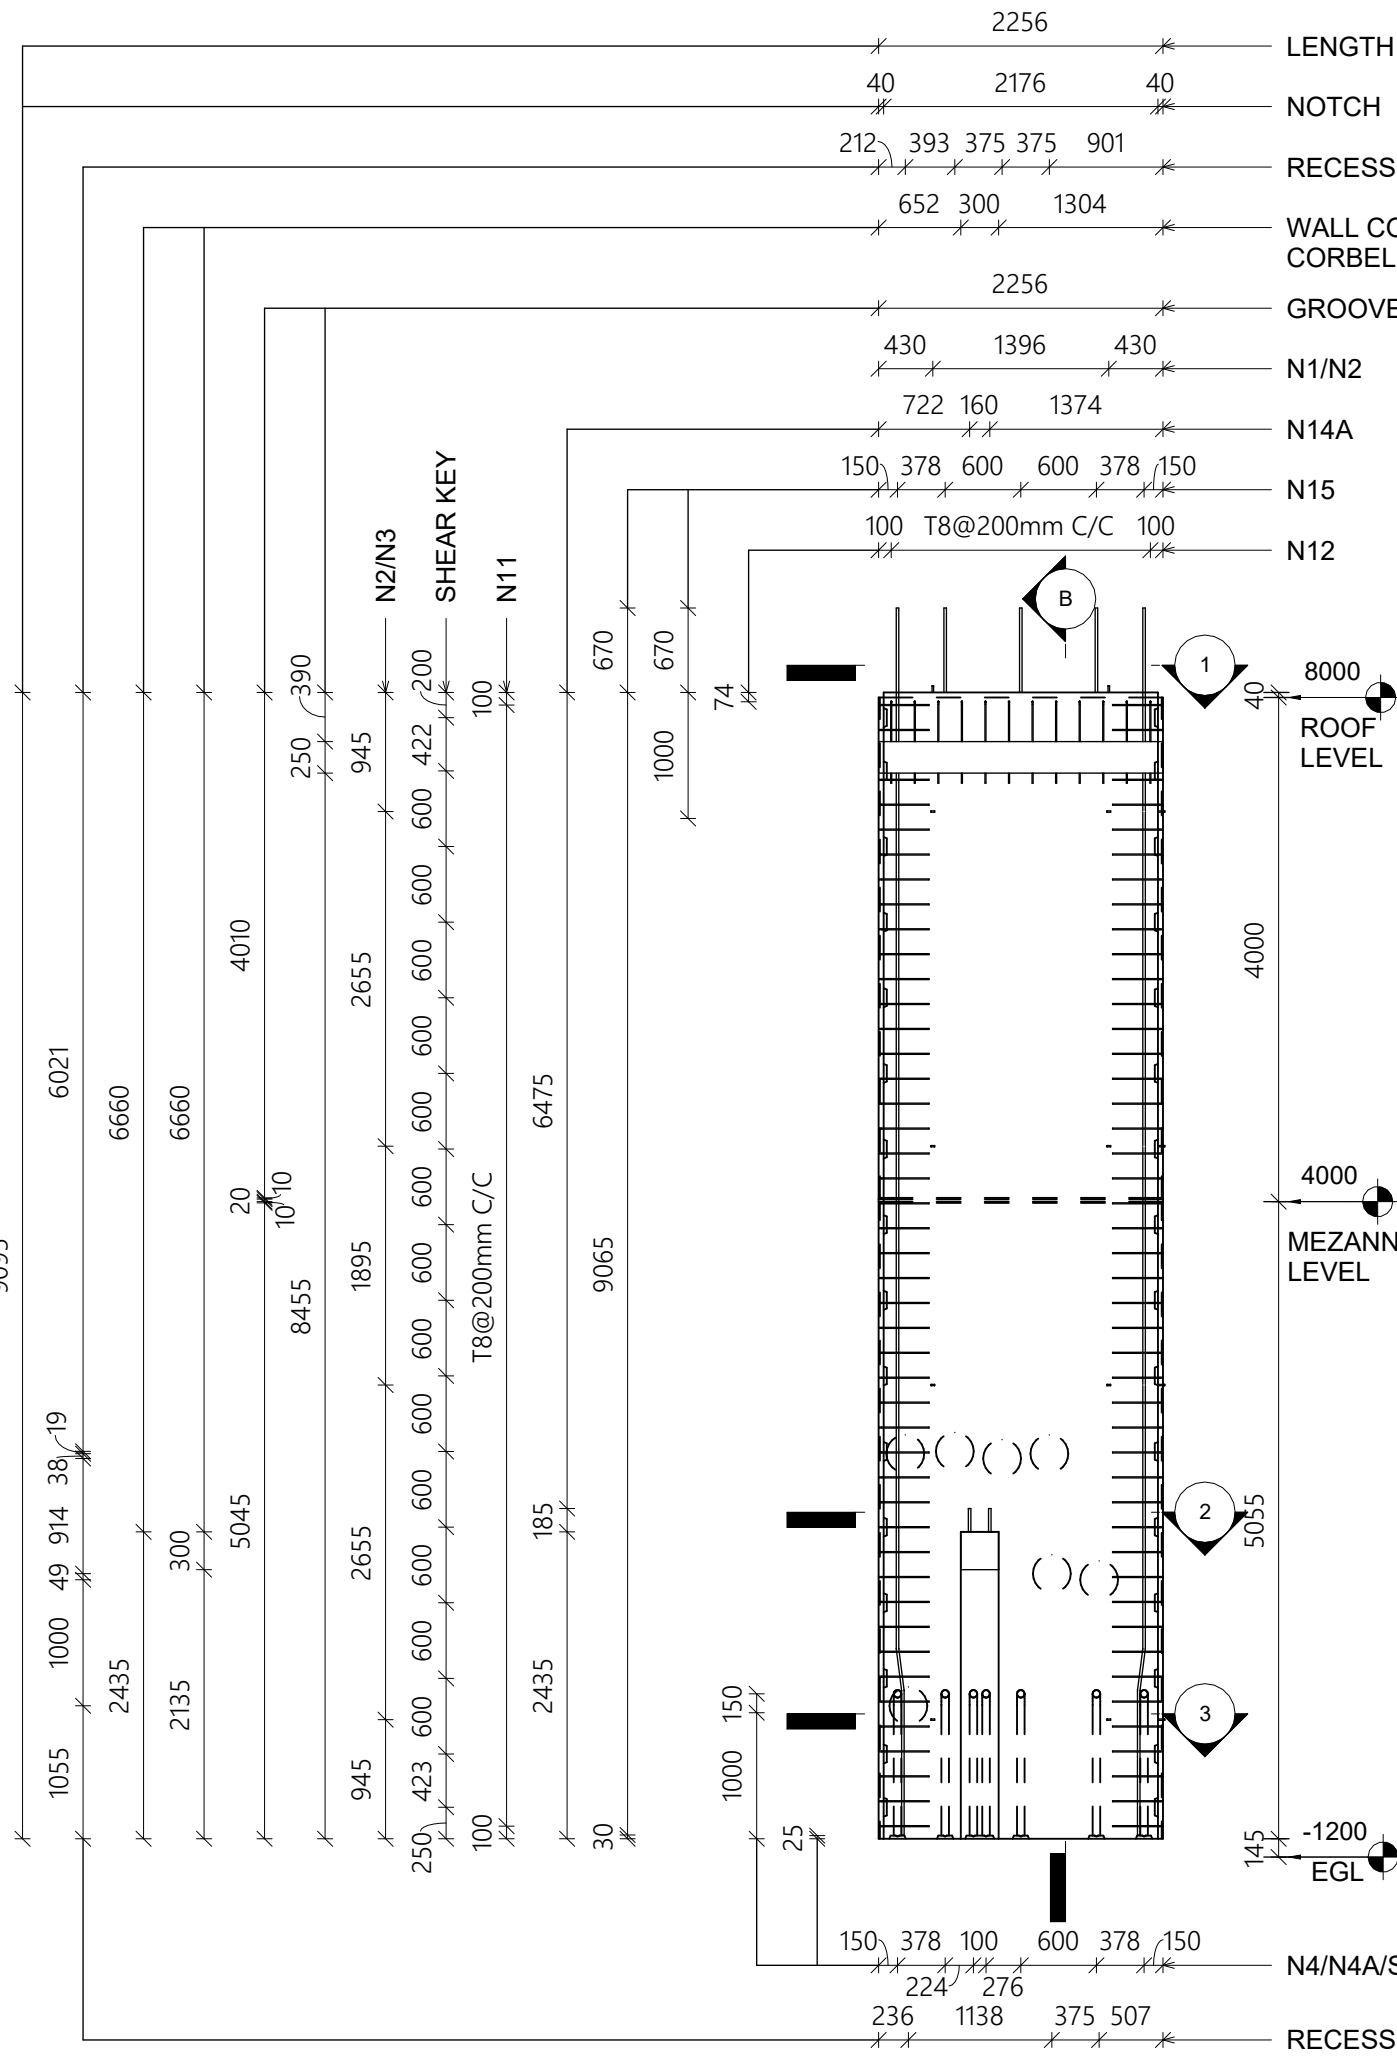

**A ELEVATION**  
1 : 60

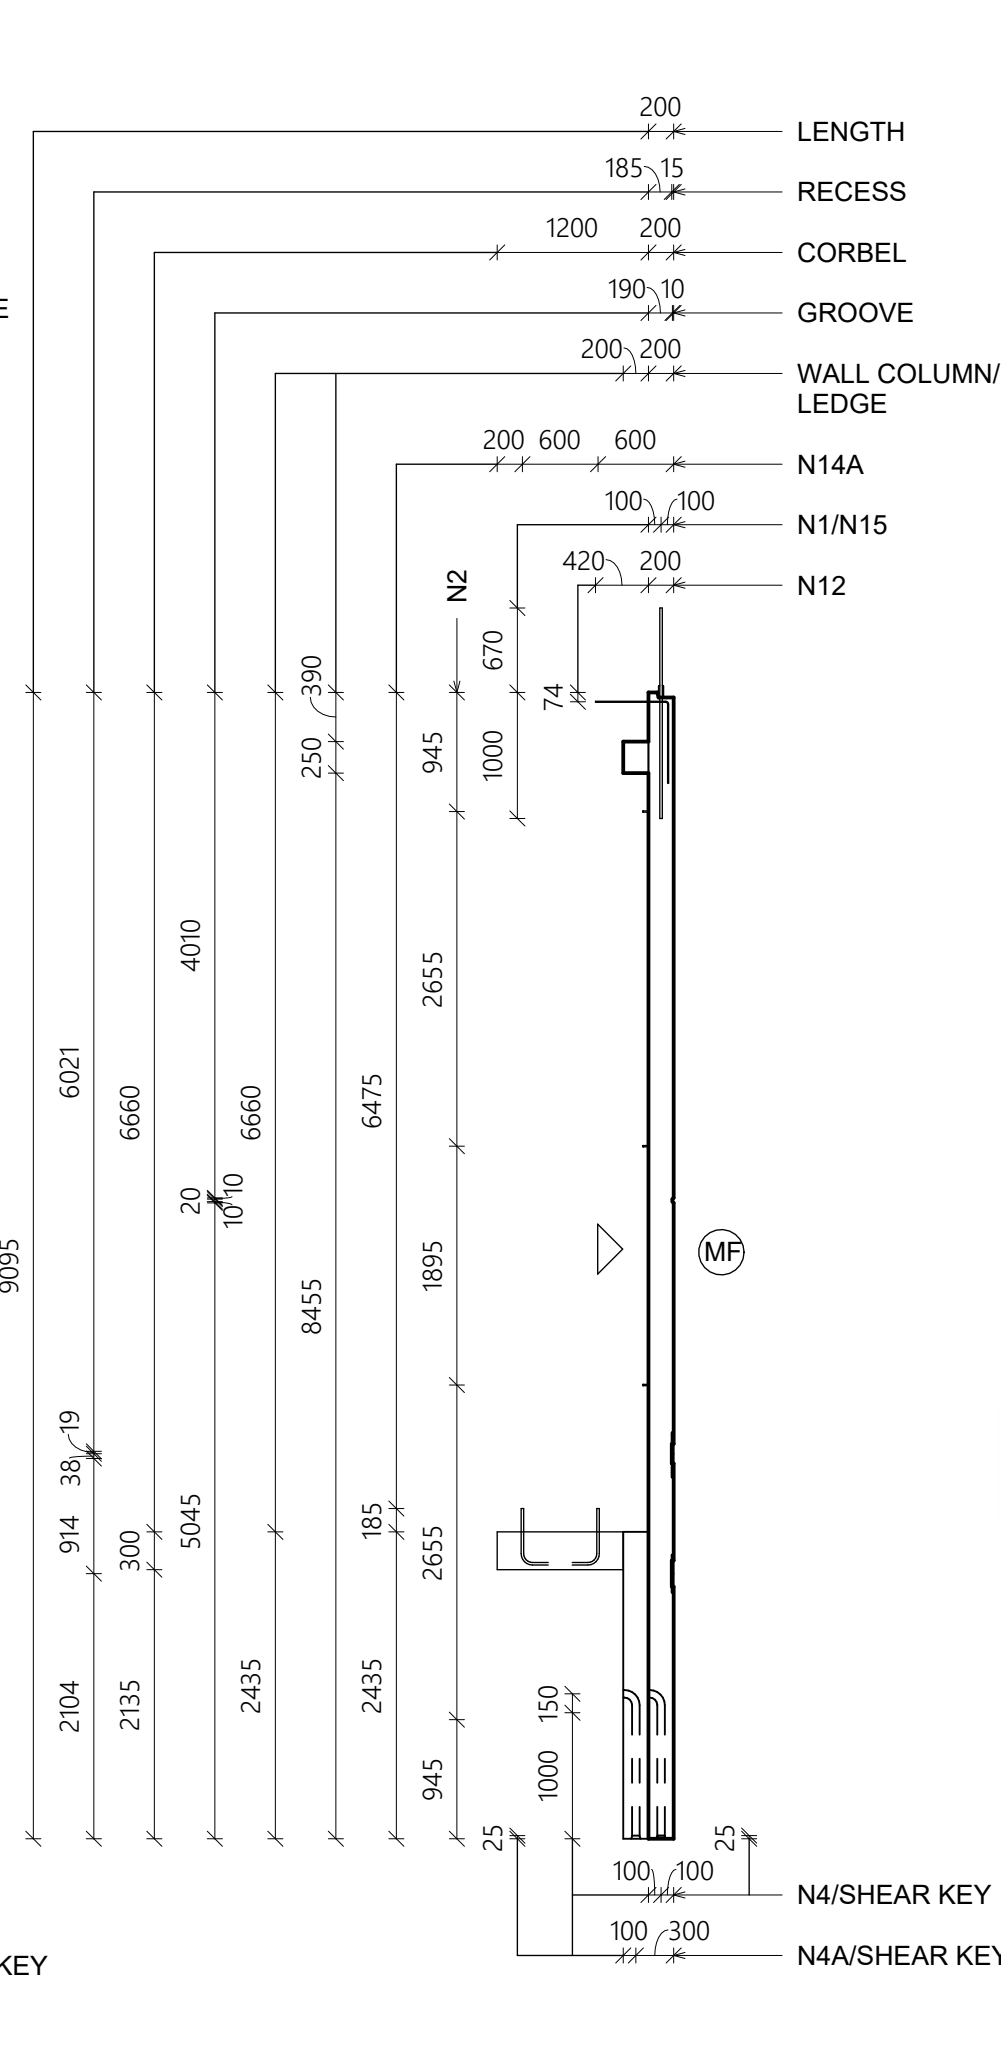

**B SECTION**  
1 : 60

PROJECT :-  
MF FACTORY

GENERAL NOTES:  
  
GRADE OF CONCRETE - M40  
GRADE OF STEEL - Fe500  
STRIPPING STRENGTH - M20  
  
COVER  
WALL - 30mm  
CORBEL - 25mm  
  
ALL DIMENSIONS ARE IN MM  
  
LEGENDS:  
ERECTION MARK -   
MOULD FACE -

CONTRACTOR :-  
**VME Precast Products**  
  
Arihant Esta, 2g2, 2<sup>nd</sup> floor,  
No.370, Church Road, Mogappair East,  
Chennai-600037.  
Tel:+91- 98400 - 41400 / 90802 - 22066

STRUCTURAL CONSULTANT :-  
  
**ES STRUCTURAL CONSULTANT**  
B167, 12th cross street, Jawahar Nagar,  
Palayamkottai, Tirunelveli-627007  
Cell No: +91 9865803764

|                   |          |              |      |       |
|-------------------|----------|--------------|------|-------|
| 0                 | 14-06-25 | FOR APPROVAL | PK   | PRC   |
| Rev               | Date     | Description  | Chkd | Appd. |
| REVISION SCHEDULE |          |              |      |       |

DRAWING TITLE :-  
PW-GF-11-MOULD DRAWING

JOB NO. : ESP24075  
ELEMENT NO. : PW-GF-11  
DWG. NO. : PW-GF-11(M1)  
SCALE : 1 : 60

DRAWN BY:- IH  
SHEET SIZE:- A3  
REV.NO:- 0  
LEVEL. :