

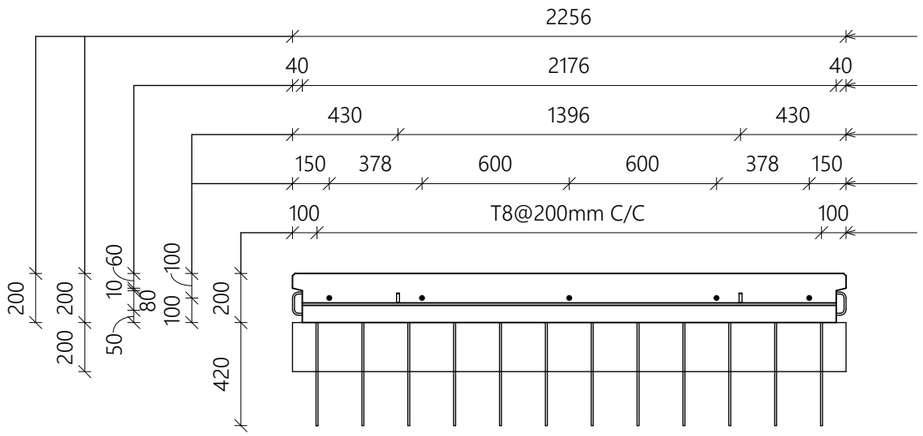



1 SECTION
1 : 25

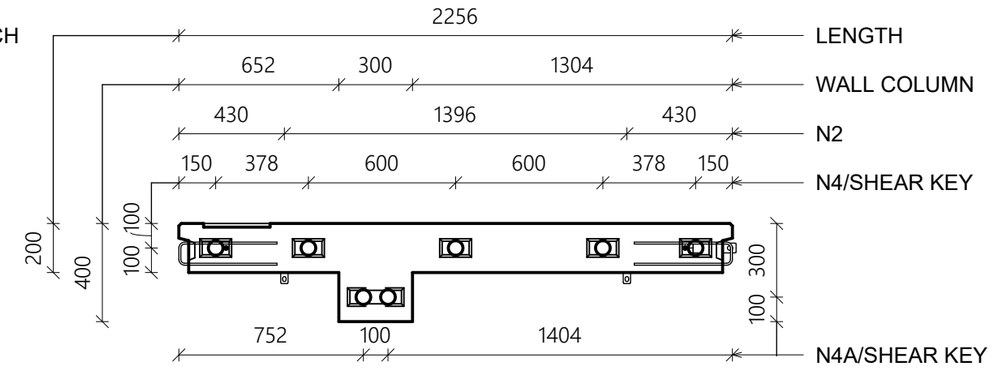


3 SECTION
1 : 25

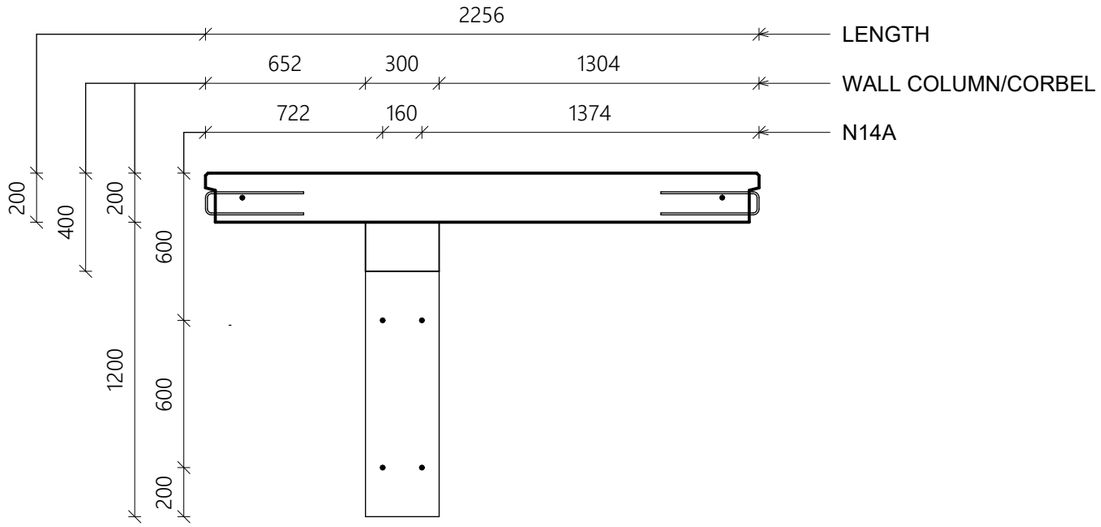


2 SECTION
1 : 25

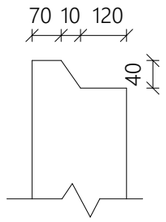


TOP NOTCH DETAIL

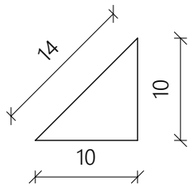


TYPICAL CHAMFER DETAIL

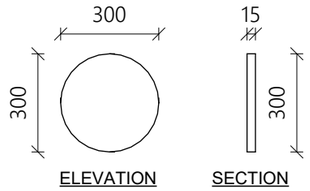


RECESS DETAIL

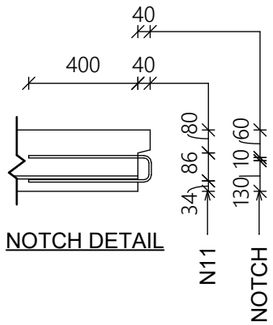

NOTCH DETAIL

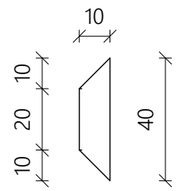

TYPICAL GROOVE DETAIL

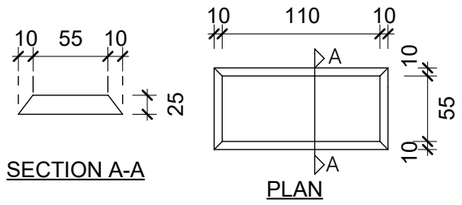

TYPICAL SHEAR KEY DETAIL


Insert Schedule		
Ref.No	Type	Count
N1	RR-SA-4.0-180	2
N2	RR-SA-2.5-200	8
N3	RR-SA-3.0-200	4
N4	60 mm dowel tube	5
N4A	60 mm dowel tube	2

Weight Schedule	
Volume	Weight
4.30 m^3	10754.32 kg

Projecting Bar Schedule		
Ref.No	Bar Diameter	Quantity
N12	8 mm	12

Dowel Bar Schedule		
Ref.No	Bar Diameter	Quantity
N14A	20 mm	2
N15	20 mm	5

U Bar Schedule		
Ref.No	Bar Diameter	Quantity
N11	8 mm	92

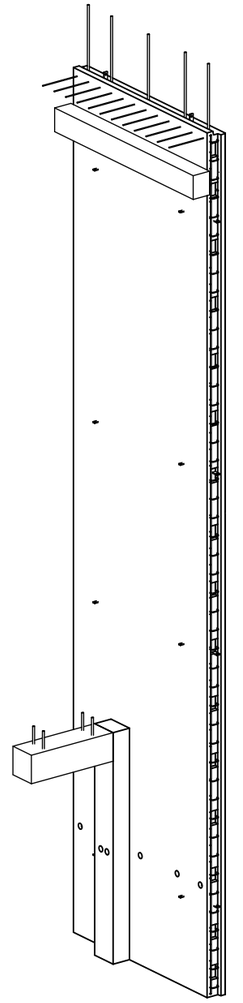

4 3D VIEW

PROJECT -:
MF FACTORY

GENERAL NOTES:

GRADE OF CONCRETE	- M40
GRADE OF STEEL	- Fe500
STRIPPING STRENGTH	- M20

COVER

WALL	- 30mm
CORBEL	- 25mm

ALL DIMENSIONS ARE IN MM

LEGENDS:

ERECTION MARK - △

MOULD FACE - (MF)

CONTRACTOR -:

VME Precast Products

Arihant Esta, 2g2, 2nd floor,
No.370, Church Road, Mogappair East,
Chennai-600037.
Tel:+91- 98400 - 41400 / 90802 - 22066

STRUCTURAL CONSULTANT -:

ES STRUCTURAL CONSULTANT
B167, 12th cross street, Jawahar Nagar,
Palayamkottai, Tirunelveli-627007
Cell No: +91 9865803764

Rev	Date	Description	Chkd	Appd.
0	14-06-25	FOR APPROVAL	PK	PRC

REVISION SCHEDULE

DRAWING TITLE -:

PW-GF-11-MOULD DRAWING

JOB NO. : ESP24075	DRAWN BY:- IH
ELEMENT NO. : PW-GF-11	SHEET SIZE:- A3
DWG. NO. : PW-GF-11(M2)	REV.NO:- 0
SCALE : As indicated	LEVEL. :