




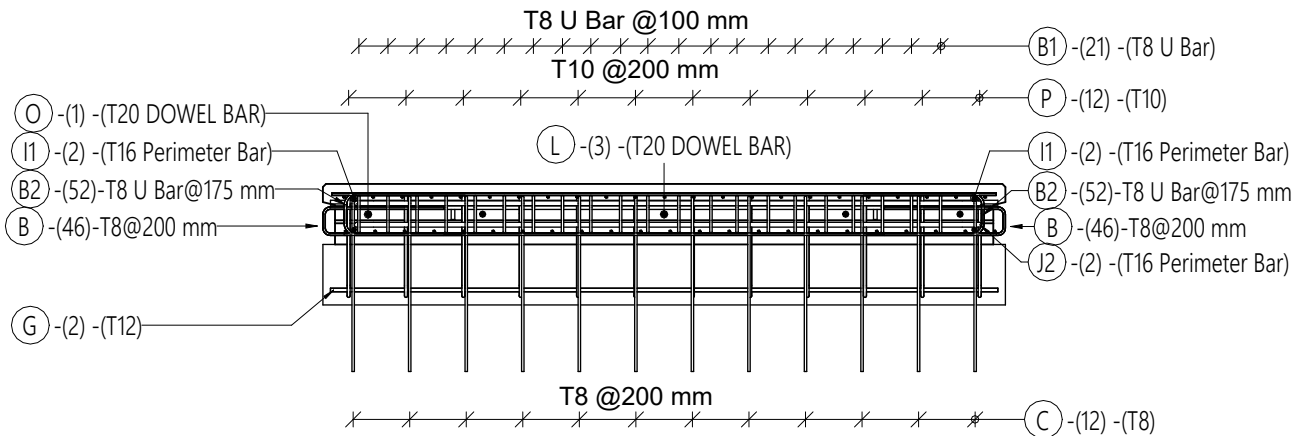

3 SECTION (REINF)  
1 : 25

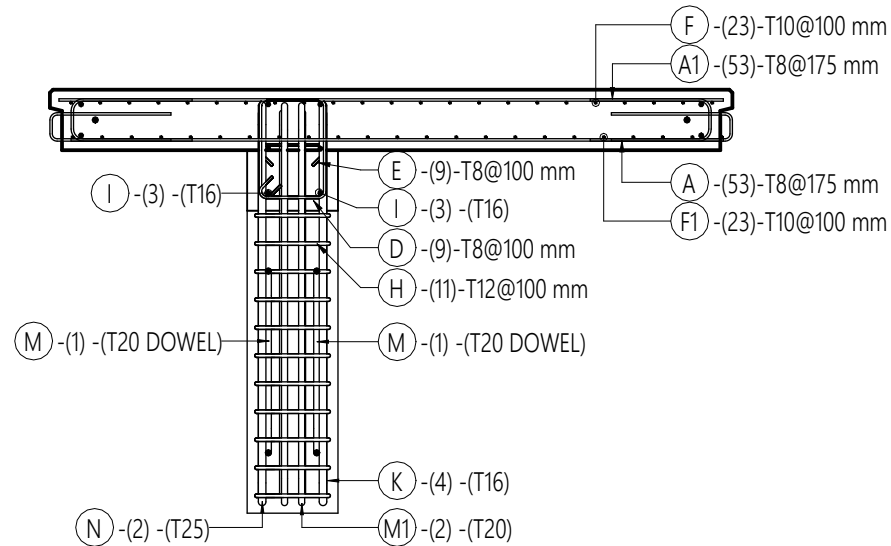

4 SECTION (REINF)  
1 : 25

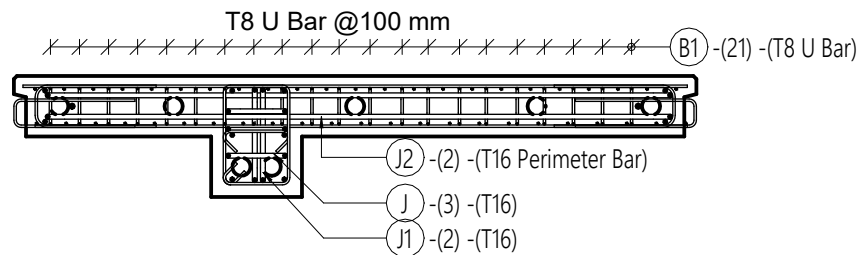

5 SECTION (REINF)  
1 : 25

| Rebar Shape   | Shape Image |
|---------------|-------------|
| M_00          |             |
| M_17          |             |
| Rebar Shape 9 |             |
| M_17A         |             |
| 26            |             |
| M_T1          |             |
| M_T10         |             |

## PROJECT -: MF FACTORY

### GENERAL NOTES:

|                    |         |
|--------------------|---------|
| GRADE OF CONCRETE  | - M40   |
| GRADE OF STEEL     | - Fe500 |
| STRIPPING STRENGTH | - M20   |

### COVER

|        |        |
|--------|--------|
| WALL   | - 30mm |
| CORBEL | - 25mm |

ALL DIMENSIONS ARE IN MM

### LEGENDS:


|               |   |  |
|---------------|---|--|
| ERECTION MARK | - |  |
| MOULD FACE    | - |  |

### CONTRACTOR -:

#### VME Precast Products

 Arihant Esta, 2g2, 2<sup>nd</sup> floor,  
No.370, Church Road, Mogappair East,  
Chennai-600037.  
Tel:+91- 98400 - 41400 / 90802 - 22066

### STRUCTURAL CONSULTANT -:

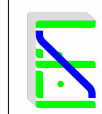 **ES STRUCTURAL CONSULTANT**  
B167, 12th cross street, Jawahar Nagar,  
Palayamkottai, Tirunelveli-627007  
Cell No: +91 9865803764

| 0   | 14-06-25 | FOR APPROVAL | PK   | PRC   |
|-----|----------|--------------|------|-------|
| Rev | Date     | Description  | Chkd | Appd. |

### REVISION SCHEDULE

### DRAWING TITLE -:

PW-GF-11-REINF DRAWING

|                         |                 |
|-------------------------|-----------------|
| JOB NO. : ESP24075      | DRAWN BY:- IH   |
| ELEMENT NO. : PW-GF-11  | SHEET SIZE:- A3 |
| DWG. NO. : PW-GF-11(R2) | REV.NO:- 0      |
| SCALE : 1 : 25          | LEVEL. :        |