


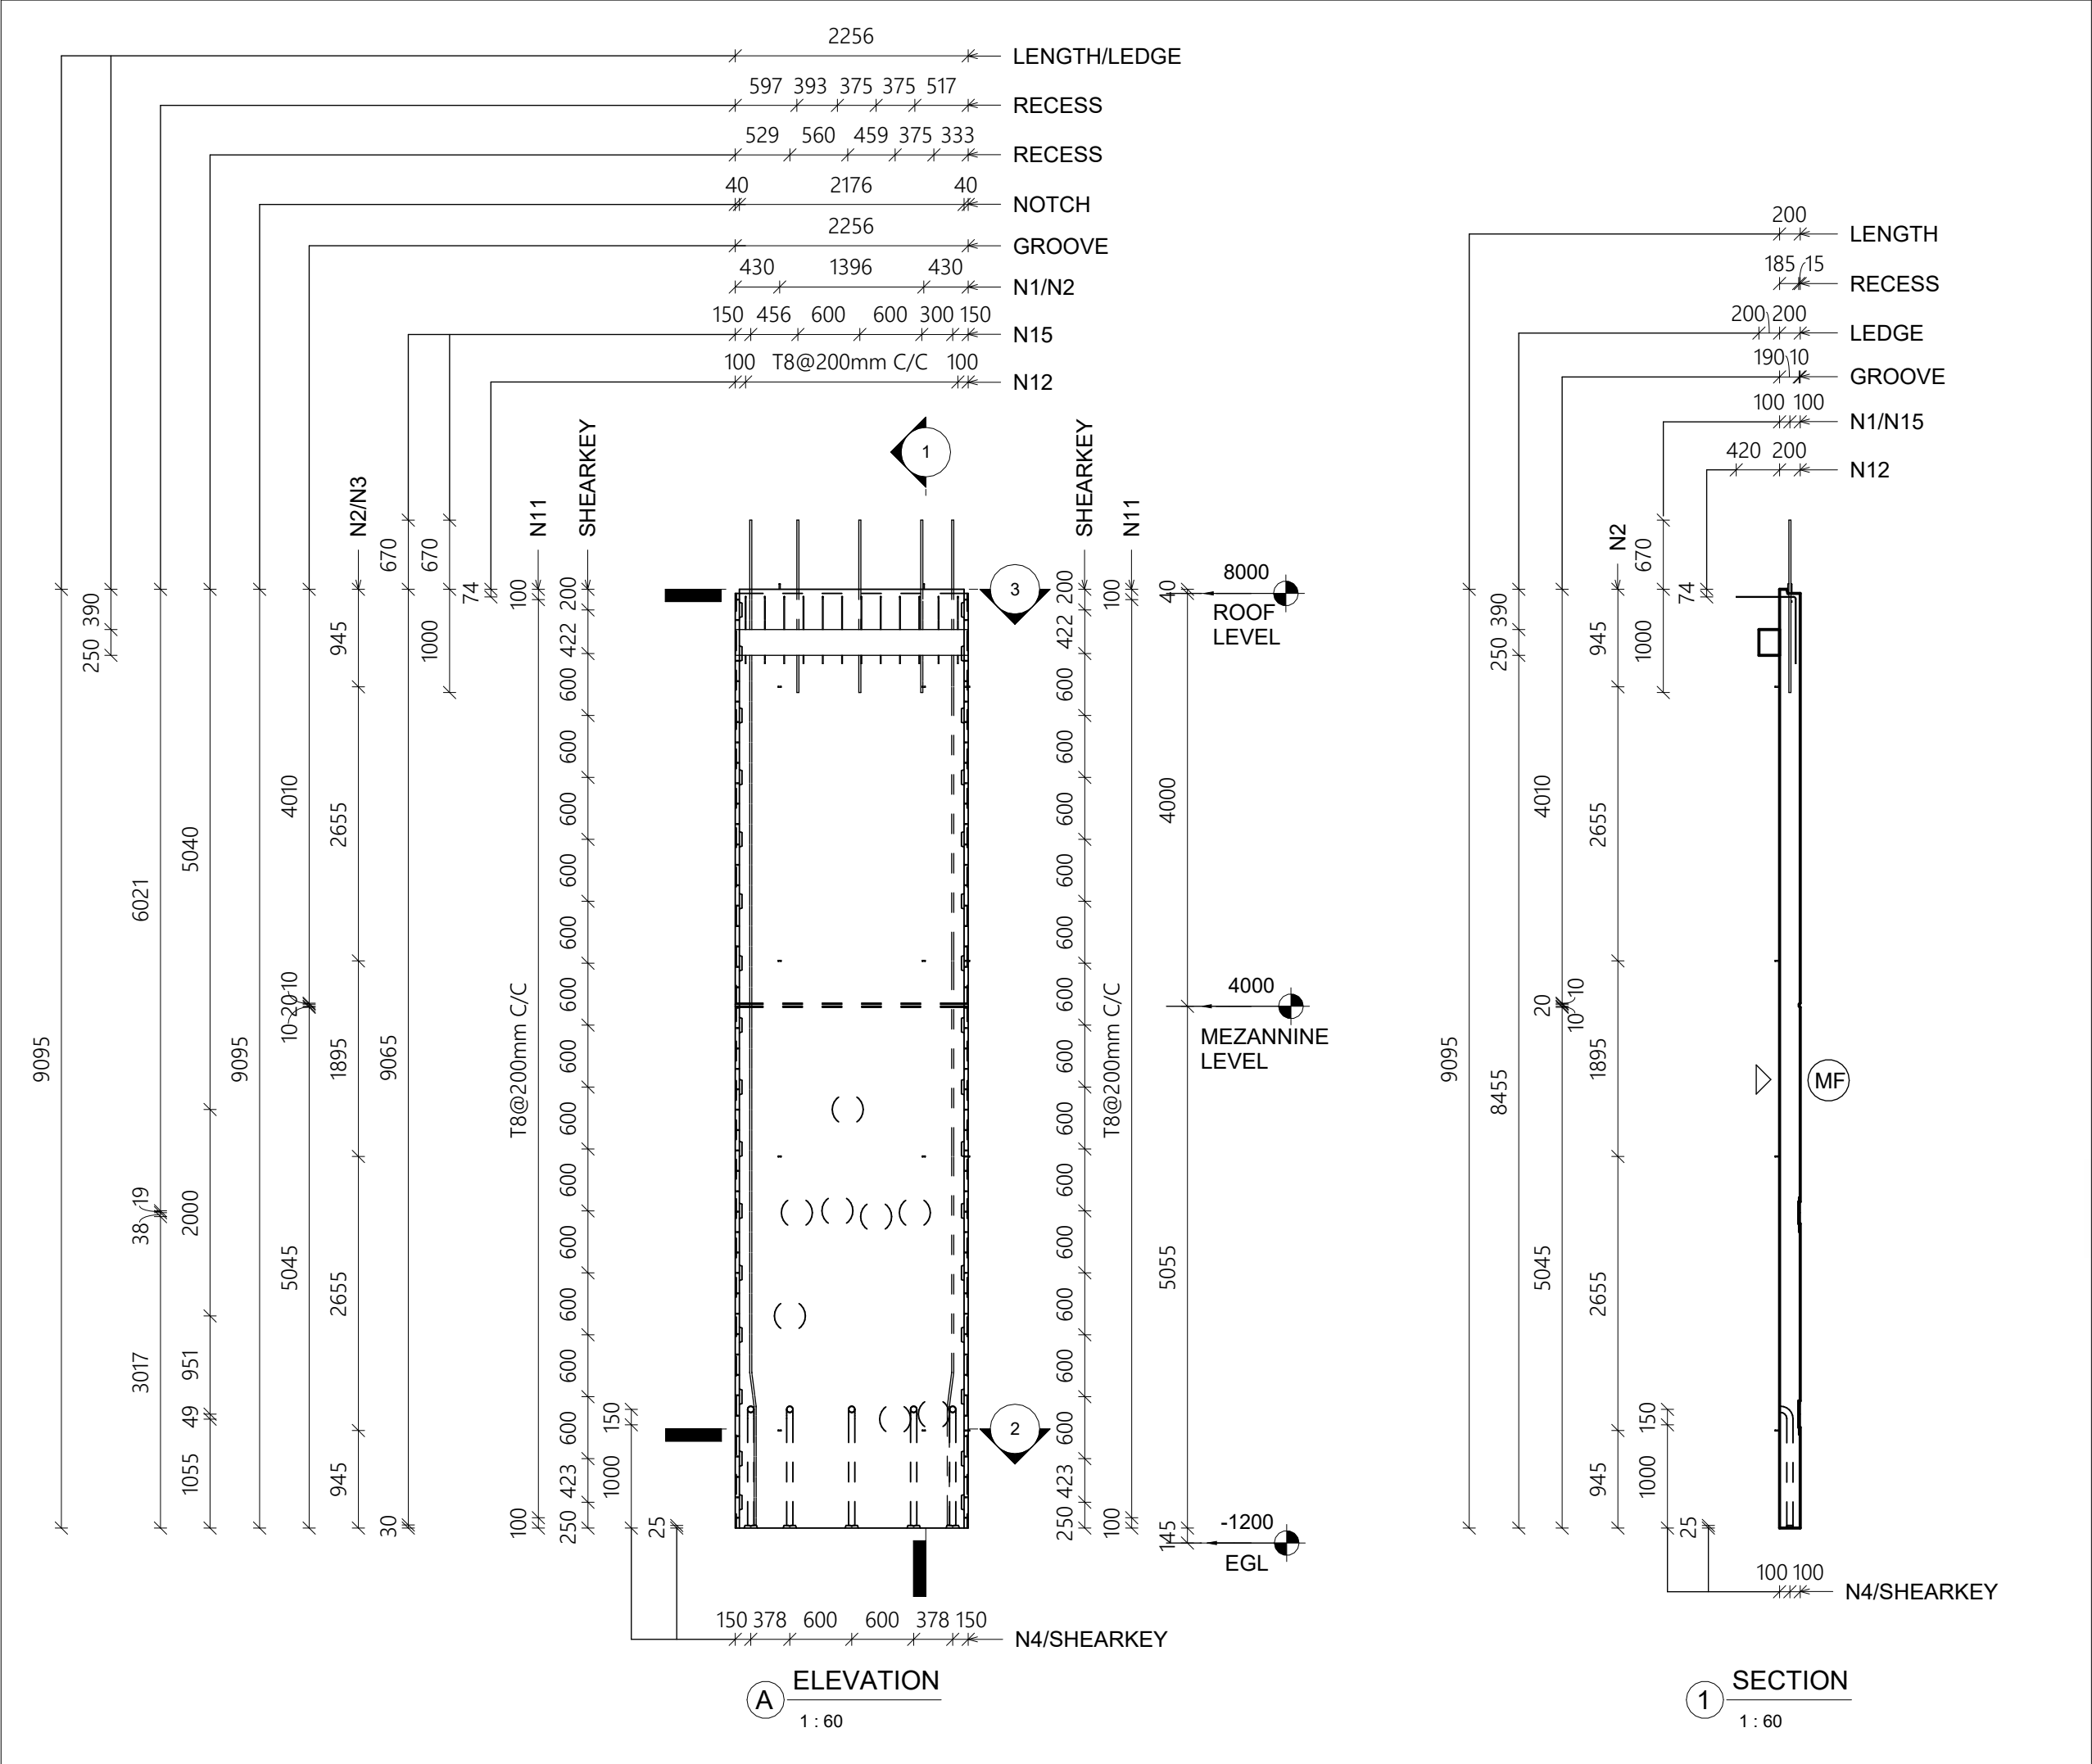

PROJECT -:
MF FACTORY

GENERAL NOTES:

- GRADE OF CONCRETE - M40
- GRADE OF STEEL - Fe500
- STRIPPING STRENGTH - M20

COVER

- WALL - 30mm
- CORBEL - 25mm

ALL DIMENSIONS ARE IN MM

LEGENDS:

- ERECTION MARK -
- MOULD FACE -

CONTRACTOR -:

VME Precast Products
Arihant Esta, 2g2, 2nd floor,
No.370, Church Road, Mogappair East,
Chennai-600037.
Tel:+91- 98400 - 41400 / 90802 - 22066

STRUCTURAL CONSULTANT -:

ES STRUCTURAL CONSULTANT
B167, 12th cross street, Jawahar Nagar,
Palayamkottai, Tirunelveli-627007
Cell No: +91 9865803764

1	26-05-25	FOR APPROVAL	PK	PRC
0	21-04-25	FOR APPROVAL	PK	PRC
Rev	Date	Description	Chkd	Appd.

REVISION SCHEDULE

DRAWING TITLE -:

PW-GF-12-MOULD DRAWING

JOB NO. : ESP24075	DRAWN BY:- AR
ELEMENT NO. : PW-GF-12	SHEET SIZE:- A3
DWG. NO. : PW-GF-12(M1)	REV.NO:- 1
SCALE : 1 : 60	LEVEL. : GF