

PROJECT -:
MF FACTORY

GENERAL NOTES:

- GRADE OF CONCRETE - M40
GRADE OF STEEL - Fe500
WALL COVER - 30mm
ALL DIMENSIONS ARE IN MM

LEGENDS:

- ERECTION MARK - 
MOULD FACE - 

CONTRACTOR -:

VME Precast Products

 Arihant Esta, 2g2, 2nd floor,
No.370, Church Road, Mogappair East,
Chennai-600037.
Tel:+91- 98400 - 41400 / 90802 - 22066

STRUCTURAL CONSULTANT -:

 **ES STRUCTURAL CONSULTANT**
B167, 12th cross street, Jawahar Nagar,
Palayamkottai, Tirunelveli-627007
Cell No: +91 9865803764




0	14-06-25	FOR APPROVAL	PK	PRC
Rev	Date	Description	Chkd	Appd.

REVISION SCHEDULE


DRAWING TITLE -:

PW-GF-13-MOULD DRAWING


JOB NO. : ESP24075	DRAWN BY:- RBN
ELEMENT NO. : PW-GF-13	SHEET SIZE:- A3
DWG. NO. : PW-GF-13(M2)	REV.NO:- 0
SCALE : As indicated	LEVEL. :

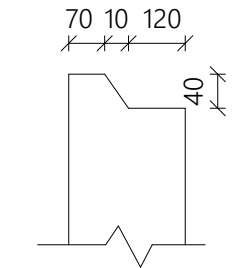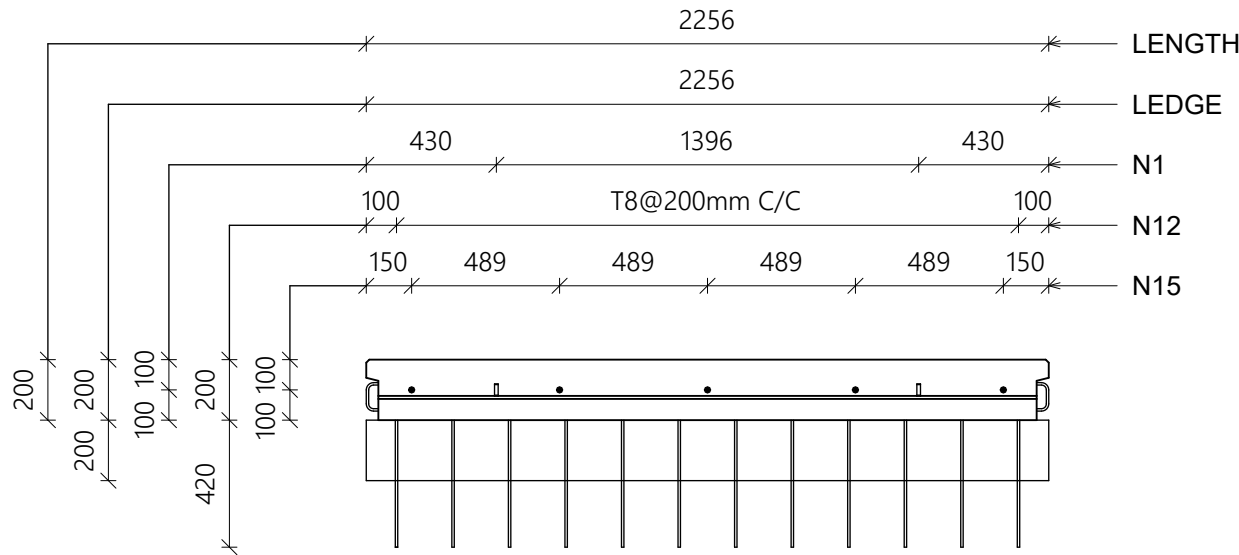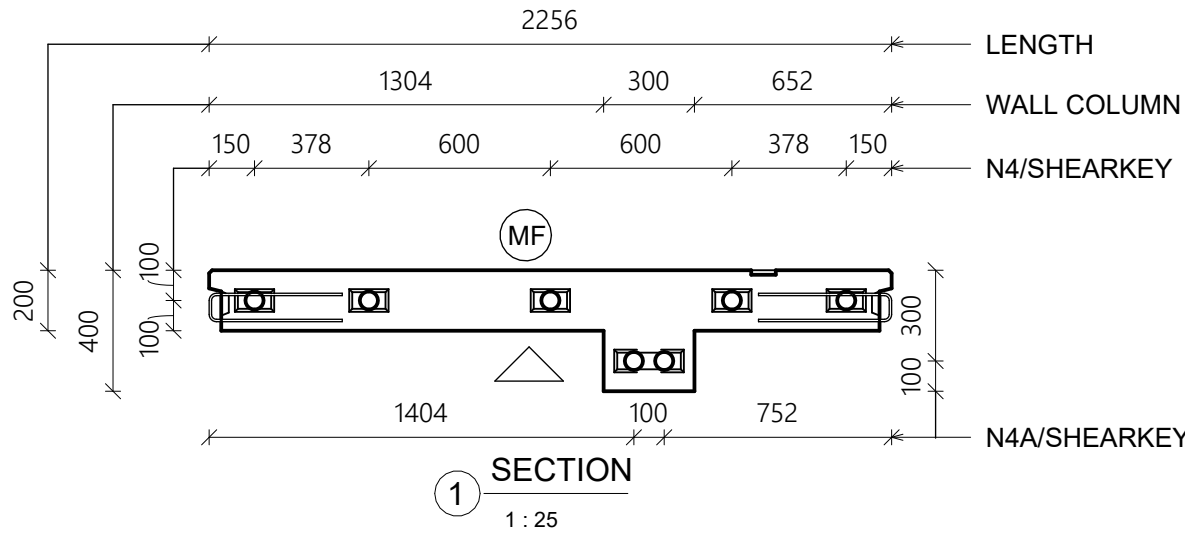


TOP NOTCH DETAIL

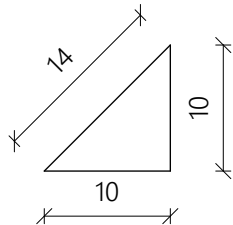


TYPICAL CHAMFER DETAIL

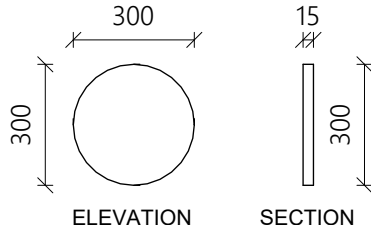


RECESS DETAIL

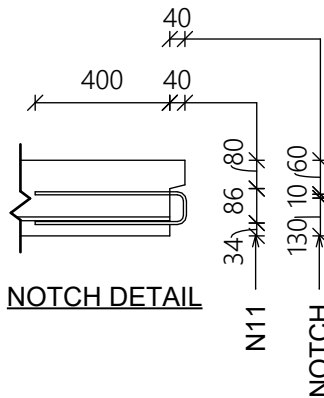


NOTCH DETAIL

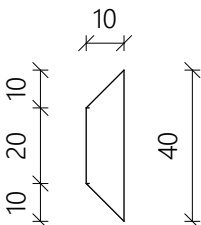

TYPICAL GROOVE DETAIL

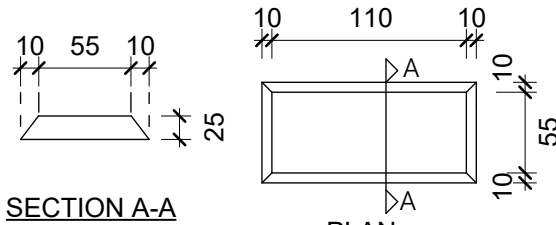

TYPICAL SHEAR KEY DETAIL

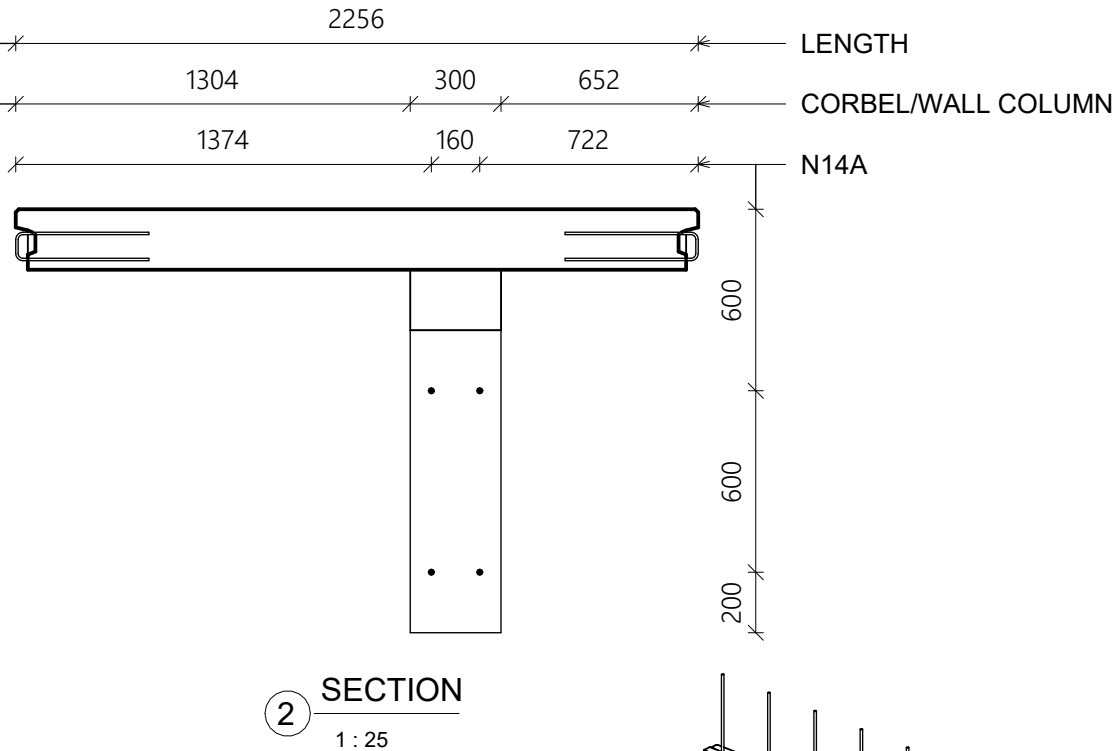

Insert Schedule		
Ref No.	Type	Count
N1	RR-SA-4.0-180	2
N2	RR-SA-2.5-200	8
N3	RR-SA-3.0-200	4
N4	60 mm dowel tube	5
N4A	60 mm dowel tube	2


Weight Schedule	
Volume	Weight
4.30 m ³	10756.85 kg

Dowel Bar Schedule		
Ref.No	Bar Diameter	Count
N14A	20 mm	2
N15	20 mm	5

Projecting Bar Schedule		
Ref.No	Bar Diameter	Count
N12	8 mm	12

U Bar Schedule		
Ref.No	Bar Diameter	Count
N11	8 mm	92

NOTE: FOR REINFORCEMENT DETAILS
REFER PW-GF-11

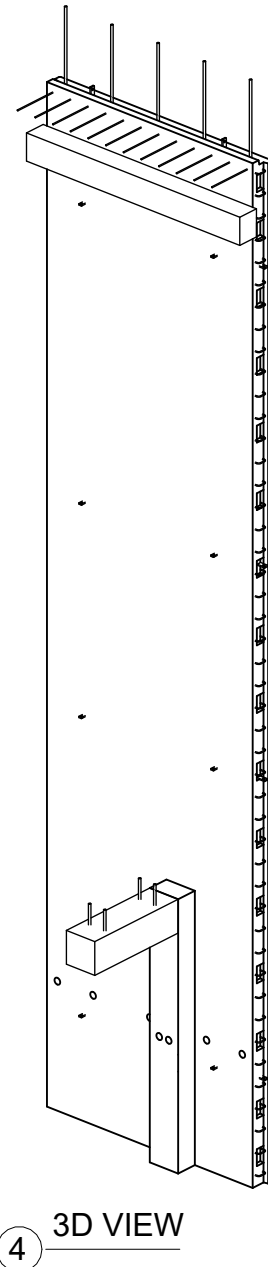

3D VIEW