
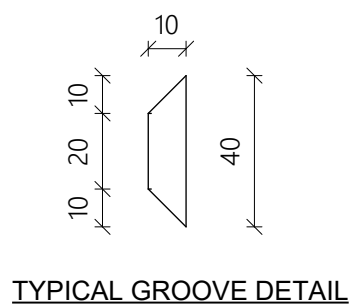
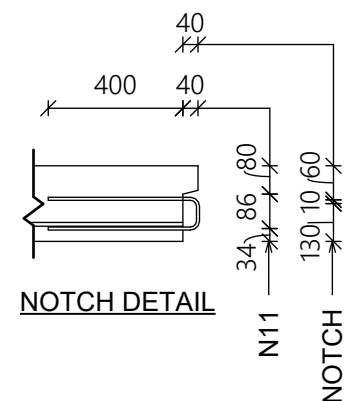
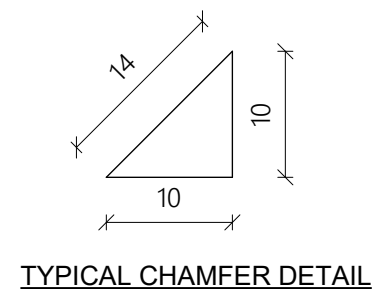


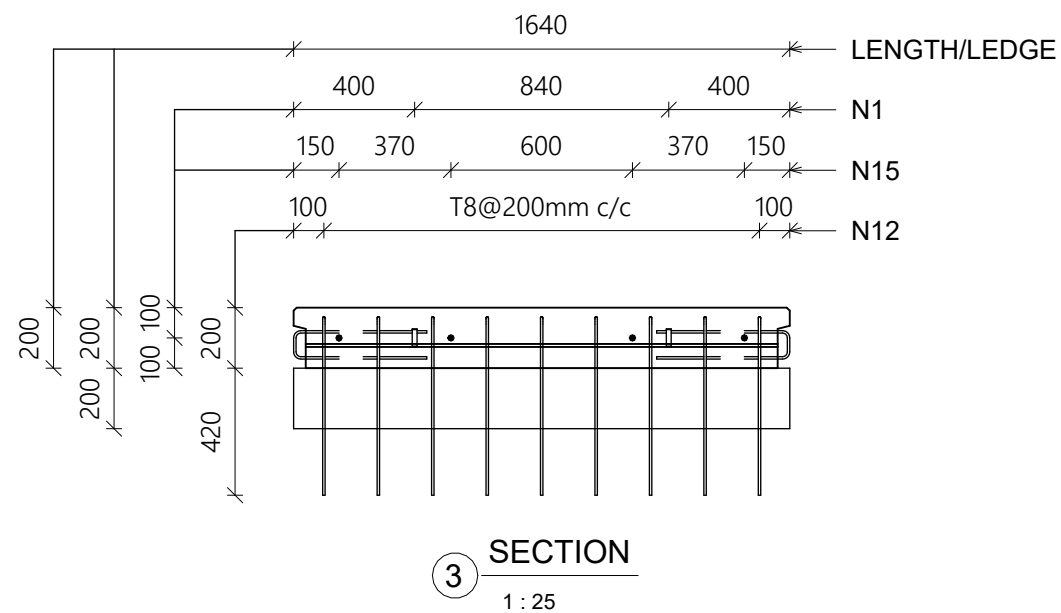


Weight Schedule	
Volume	Weight
2.93 m ³	7325.36 kg

Insert Schedule		
Ref No.	Type	Count
N1	RR-SA-7.5-260	2
N2	RR-SA-1.4-160	8
N3	RR-SA-2.5-200	4
N4	60 mm dowel tube	4


U Bar & Projecting Bar Schedule		
Ref.No	Bar Diameter	Quantity
N11	8 mm	92
N12	8 mm	9

Dowel Bar Schedule		
Ref.No	Bar Diameter	Count
N15	20 mm	4


NOTE: FOR REINFORCEMENT DETAILS
REFER PW-GF-30

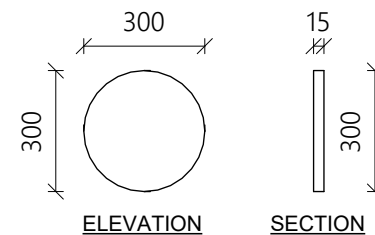

RECESS DETAIL

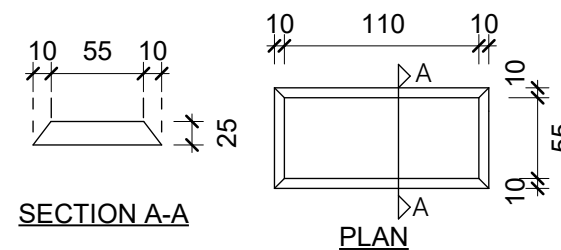

TYPICAL SHEAR KEY DETAIL

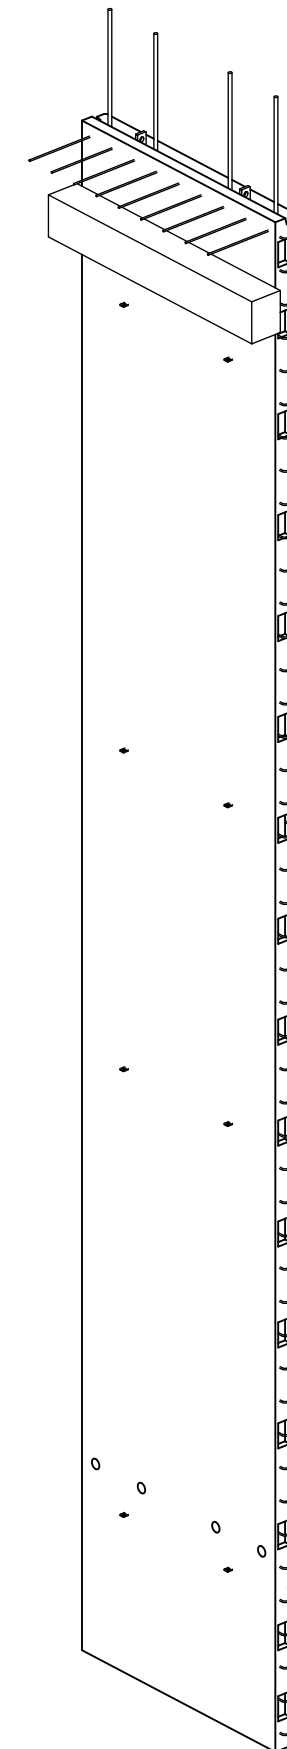

④ 3D VIEW

ERECTION MARK	-	
MOULD FACE	-	

ES STRUCTURAL CONSULTANT
 B167, 12th cross street, Jawahar Nagar,
 Palayamkottai, Tirunelveli-627007
 Cell No: +91 9865803764

1	26-05-25	FOR APPROVAL	PK	PRC
0	08-05-25	FOR APPROVAL	PK	PRC
Rev	Date	Description	Chkd	Appd.

REVISION SCHEDULE

JOB NO. : ESP24075	DRAWN BY:- AR
ELEMENT NO. : PW-GF-15	SHEET SIZE:- A3
DWG. NO. : PW-GF-15(M2)	REV.NO:- 1
SCALE : As indicated	LEVEL. : GF