

PROJECT :-
MF FACTORY

GENERAL NOTES:

GRADE OF CONCRETE	- M40
GRADE OF STEEL	- Fe500
STRIPPING STRENGTH	- M20

COVER

WALL	- 30mm
CORBEL	- 25mm

ALL DIMENSIONS ARE IN MM

LEGENDS:

ERECTION MARK	-	
MOULD FACE	-	

CONTRACTOR :-

VME Precast Products

Arihant Esta, 2g2, 2nd floor,
No.370, Church Road, Mogappair East,
Chennai-600037.
Tel:+91- 98400 - 41400 / 90802 - 22066

STRUCTURAL CONSULTANT :-

 **ES STRUCTURAL CONSULTANT**
B167, 12th cross street, Jawahar Nagar,
Palayamkottai, Tirunelveli-627007
Cell No: +91 9865803764


2	05-06-25	REVISED AS PER COLUDED	PK	PRC
1	02-06-25	REVISED AS PER COLUDED	PK	PRC
0	26-05-25	FOR APPROVAL	PK	PRC
Rev	Date	Description	Chkd	Appd.

REVISION SCHEDULE


DRAWING TITLE :-

PW-GF-18-MOULD DRAWING


JOB NO. : ESP24075	DRAWN BY:- IH
ELEMENT NO. : PW-GF-18	SHEET SIZE:- A3
DWG. NO. : PW-GF-18(M2)	REV.NO:- 2
SCALE : As indicated	LEVEL. :

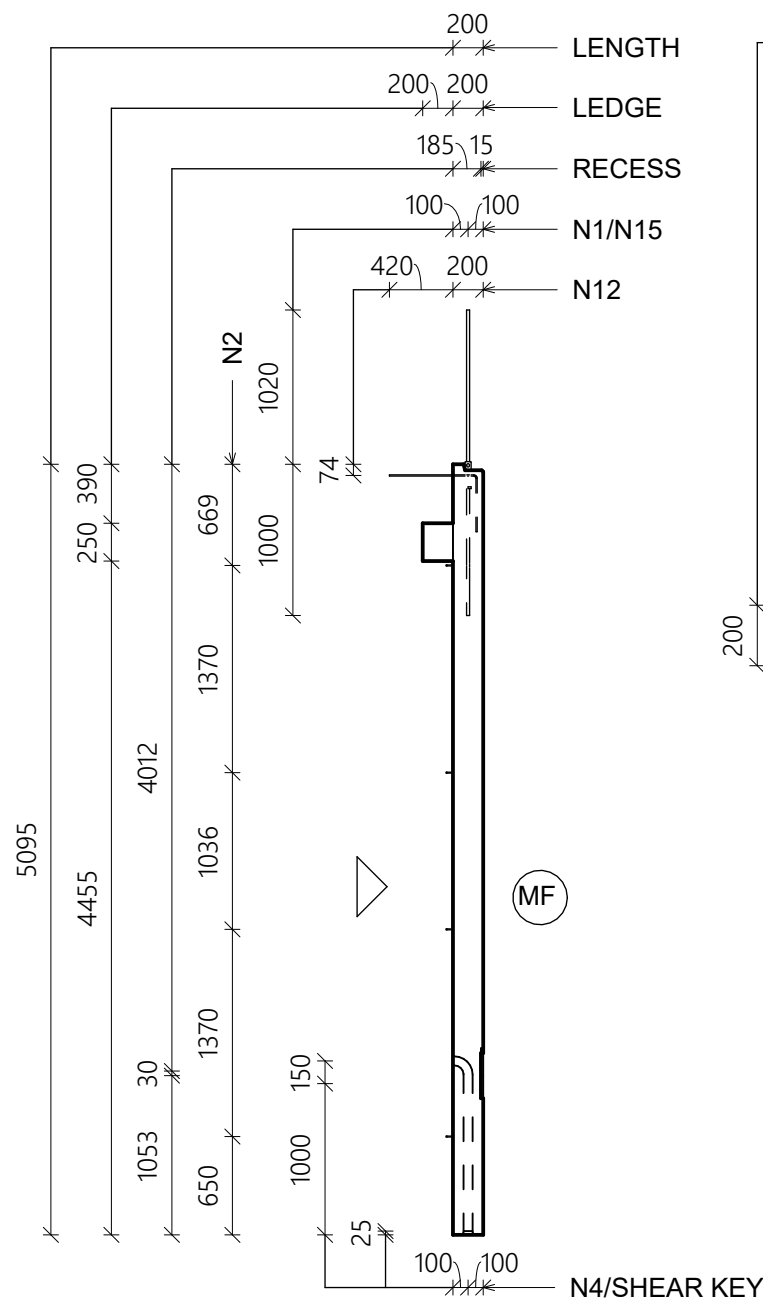


SECTION 2
1 : 50

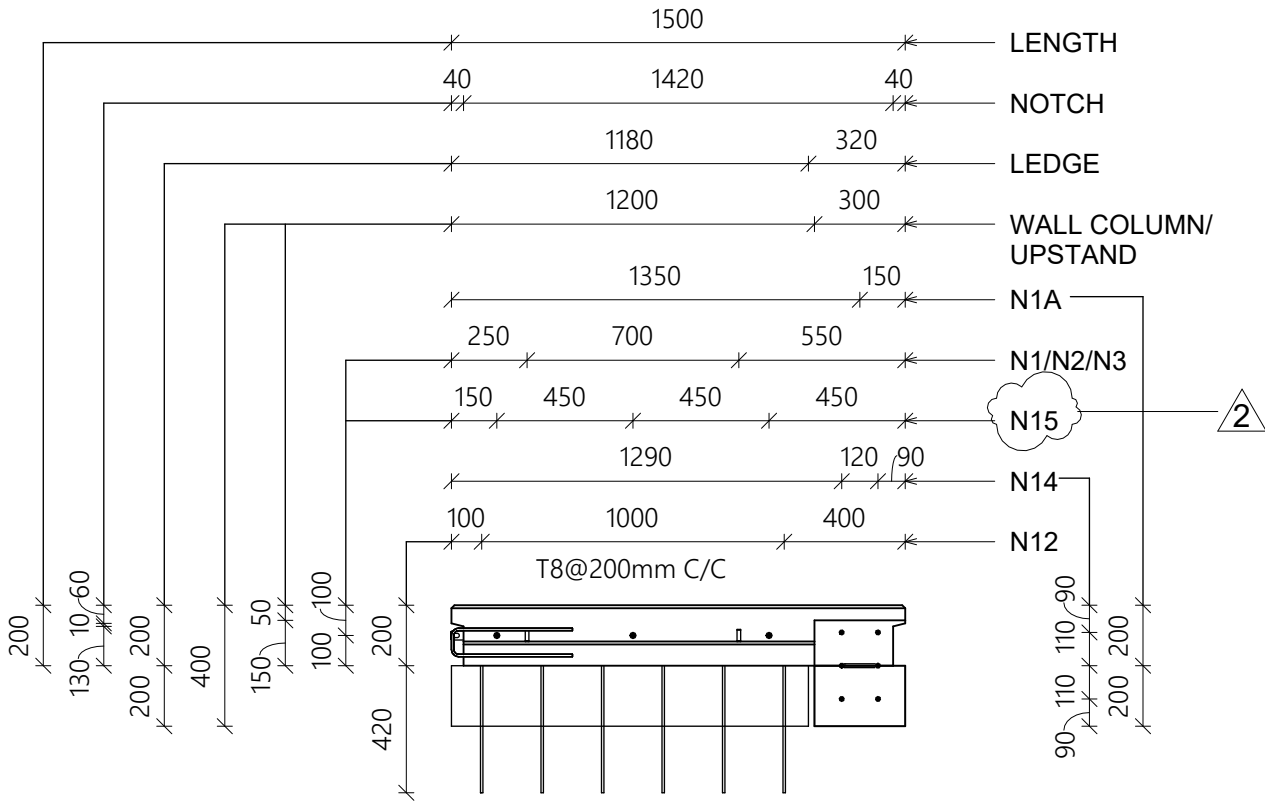

SECTION 3
1 : 25

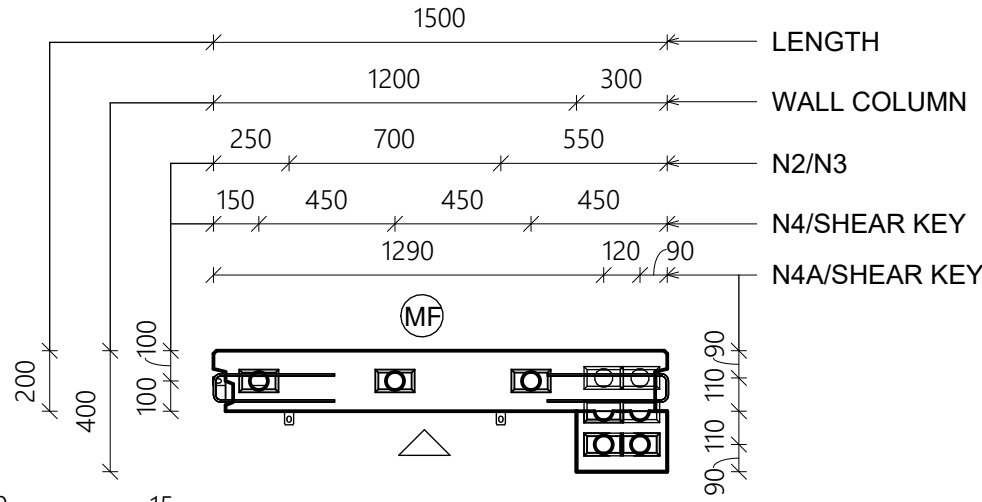

SECTION 4
1 : 25

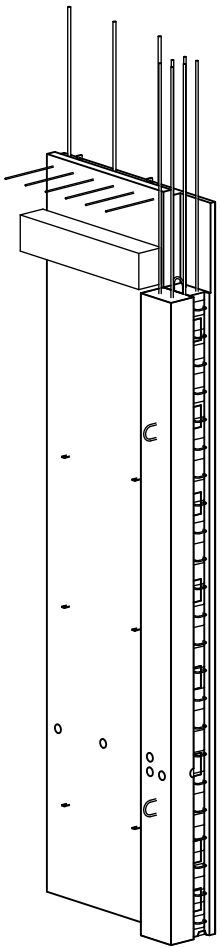

5 3D VIEW

Dowel Bar Schedule

Ref.No	Bar Diameter	Count
N14	16 mm	6
N15	20 mm	3

Loop Bar Schedule

Ref.No	Bar Diameter	Count
N11	8 mm	49

Projecting Bar Schedule


Ref.No	Bar Diameter	Count
N12	8 mm	6

Weight Schedule


Volume	Weight
2.00 m ³	5007.98 kg

Insert Schedule


Ref.No	Type	Count
N1	RR-SA-4.0-180	2
N1A	12.9Ø Lifting insert	1
N2	RR-SA-1.4-160	8
N2A	12.9Ø Lifting insert	2
N3	RR-SA-2.5-250	4
N4	60 mm dowel tube	3
N4A	60 mm dowel tube	6

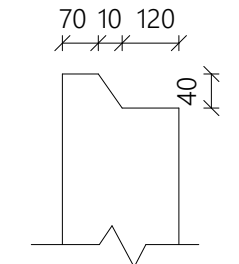


TOP NOTCH DETAIL

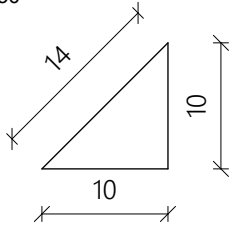


TYPICAL CHAMFER DETAIL

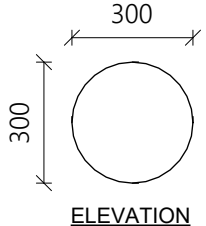


RECESS DETAIL

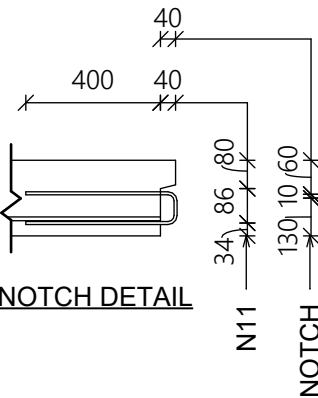

NOTCH DETAIL

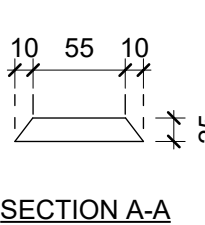

SECTION A-A

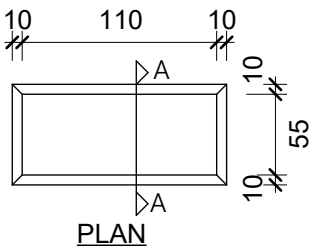

PLAN

TYPICAL SHEAR KEY DETAIL