

PROJECT :-
MF FACTORY

GENERAL NOTES:

GRADE OF CONCRETE	- M40
GRADE OF STEEL	- Fe500
STRIPPING STRENGTH	- M20

COVER

WALL	- 30mm
CORBEL	- 25mm

ALL DIMENSIONS ARE IN MM

LEGENDS:

ERECTION MARK	-	
MOULD FACE	-	

CONTRACTOR :-

VME Precast Products

 Arihant Esta, 2g2, 2nd floor,
No.370, Church Road, Mogappair East,
Chennai-600037.
Tel:+91- 98400 - 41400 / 90802 - 22066

STRUCTURAL CONSULTANT :-

ES STRUCTURAL CONSULTANT

 B167, 12th cross street, Jawahar Nagar,
Palayamkottai, Tirunelveli-627007
Cell No: +91 9865803764


2	05-06-25	REVISED AS PER COLUDED	PK	PRC
1	02-06-25	REVISED AS PER COLUDED	PK	PRC
0	26-05-25	FOR APPROVAL	PK	PRC
Rev	Date	Description	Chkd	Appd.

REVISION SCHEDULE


DRAWING TITLE :-

PW-GF-18-REINF DRAWING


JOB NO. : ESP24075	DRAWN BY:- IH
ELEMENT NO. : PW-GF-18	SHEET SIZE:- A3
DWG. NO. : PW-GF-18(R)	REV.NO:- 2
SCALE : As indicated	LEVEL. :

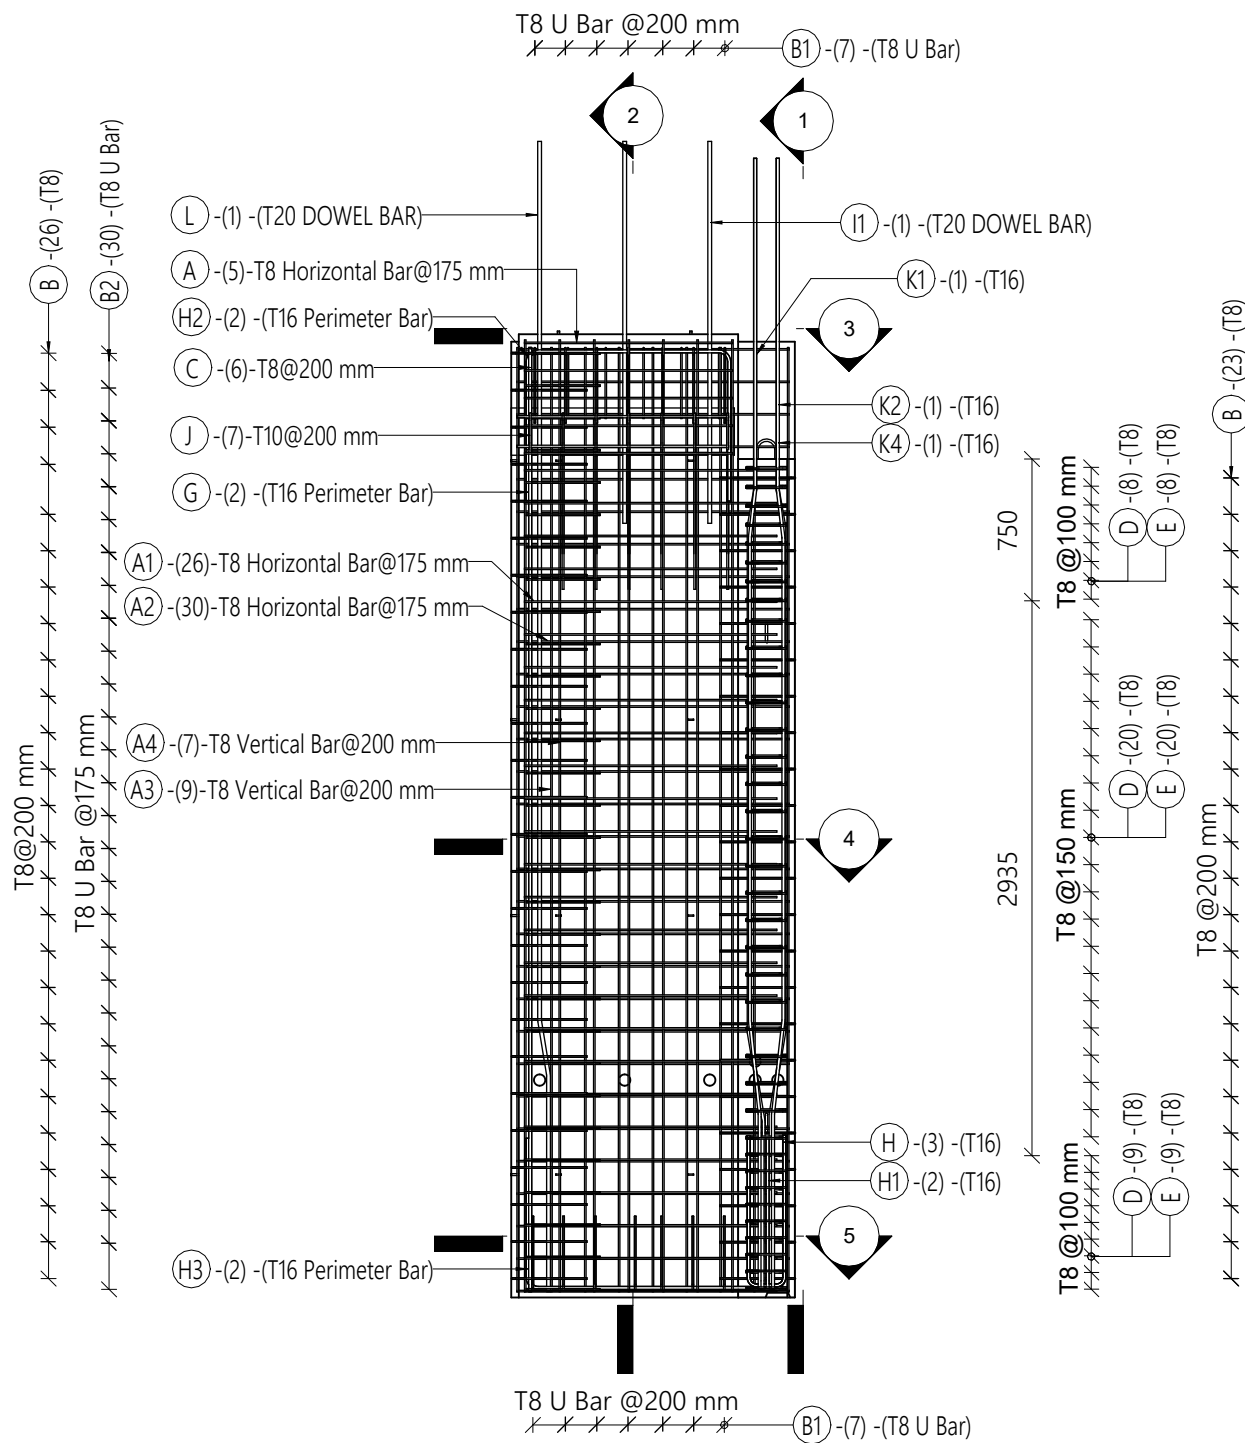


A ELEVATION (REINF)
1 : 40

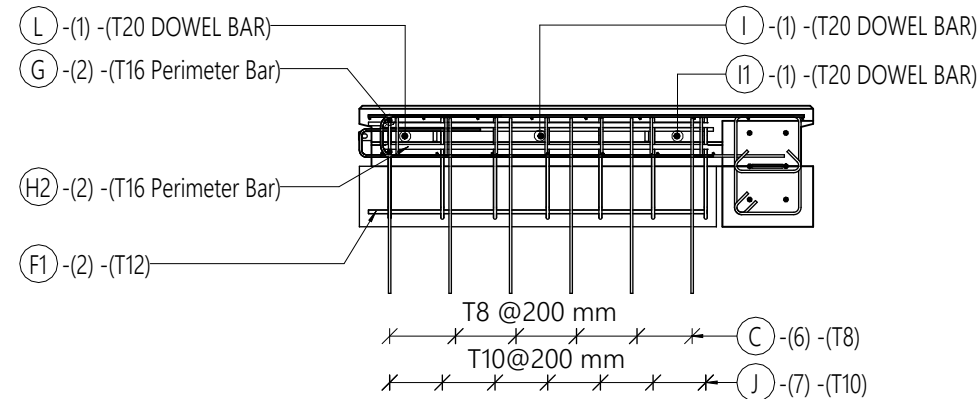


3 SECTION (REINF)
1 : 25

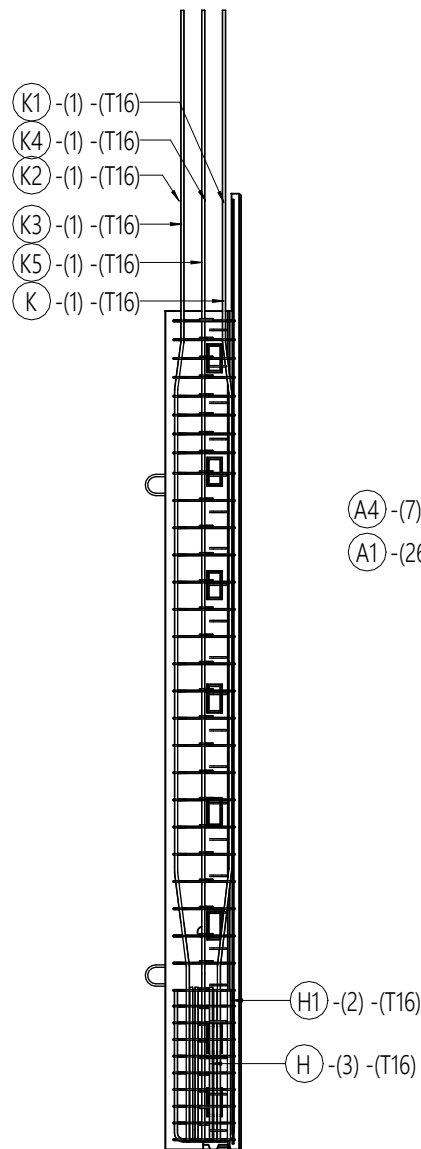


1 SECTION (REINF)
1 : 40

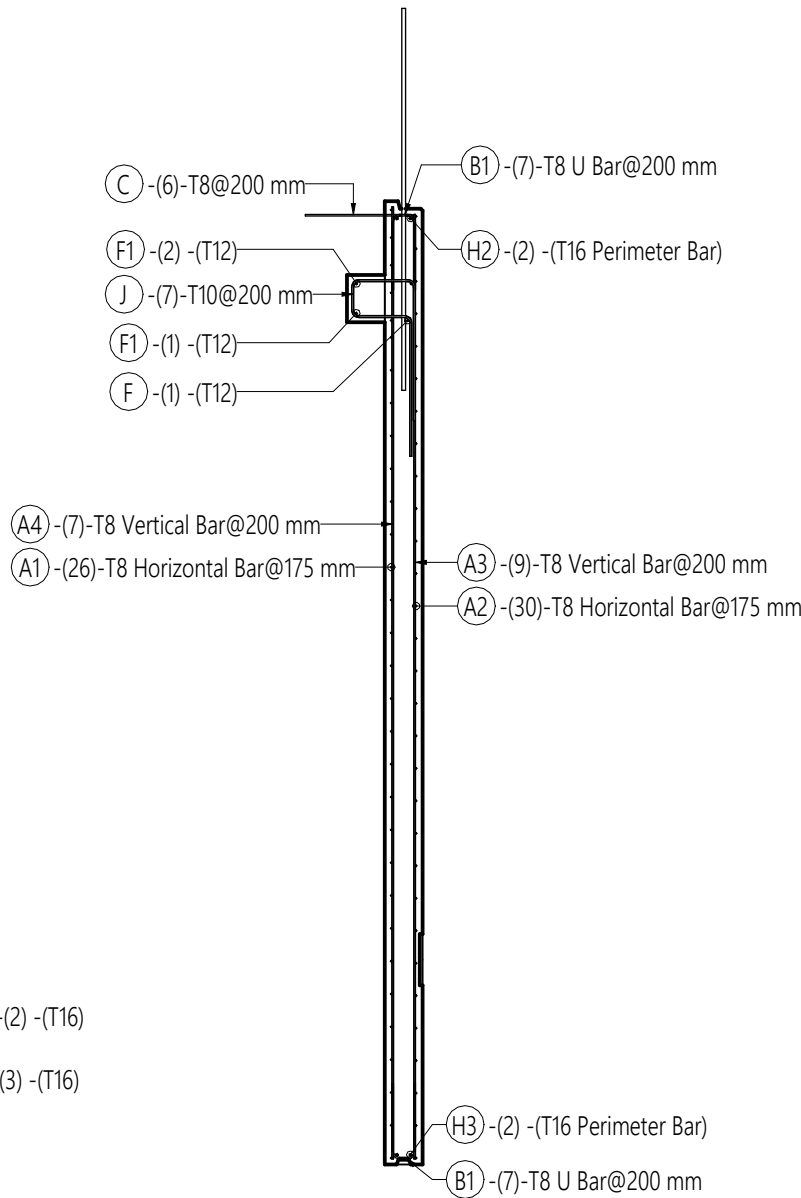

2 SECTION (REINF)
1 : 40

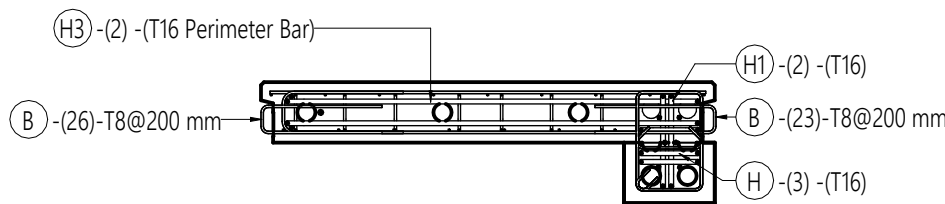

5 SECTION (REINF)
1 : 25

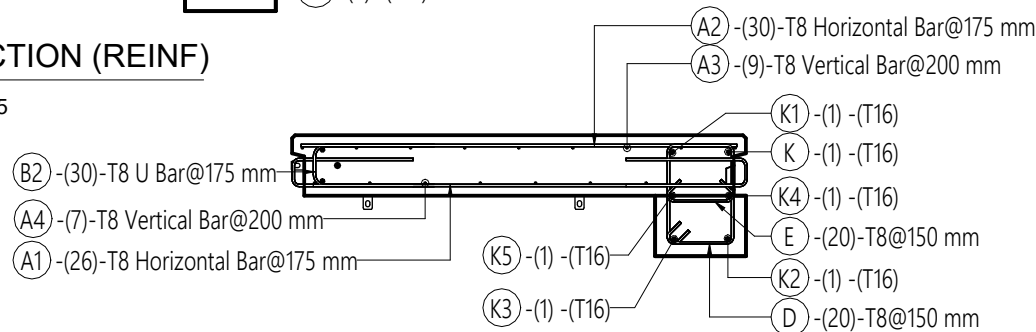

4 SECTION (REINF)
1 : 25