




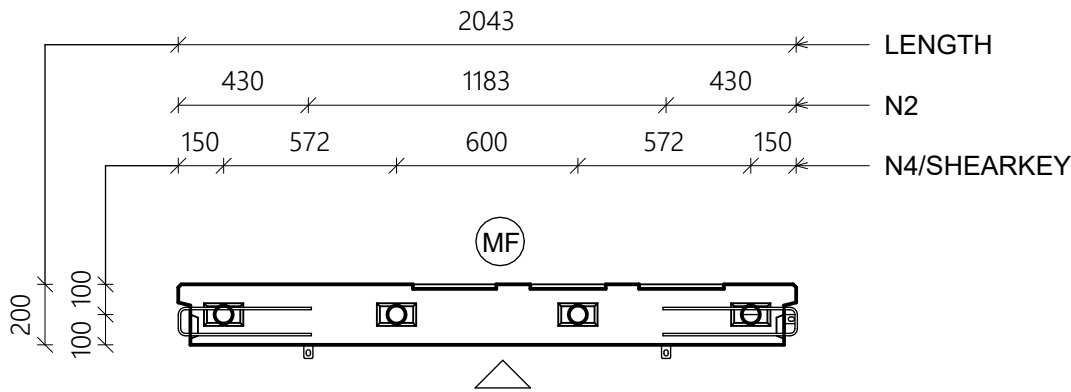


SECTION 2  
1 : 25

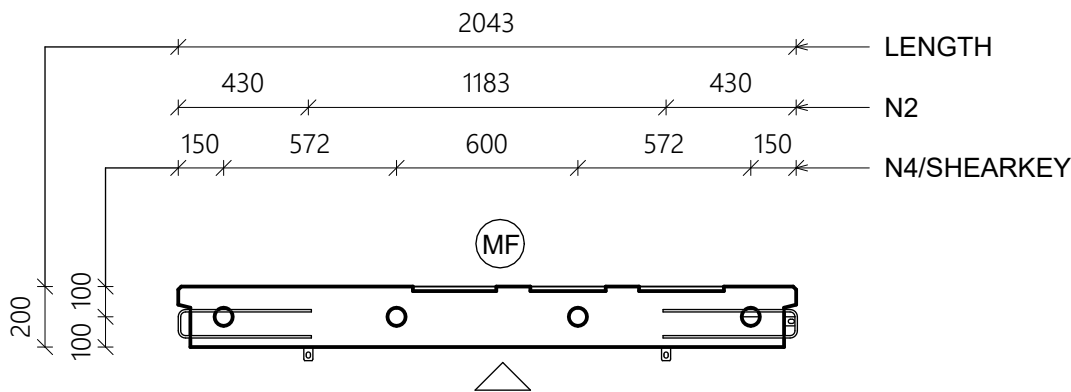


SECTION 3  
1 : 25

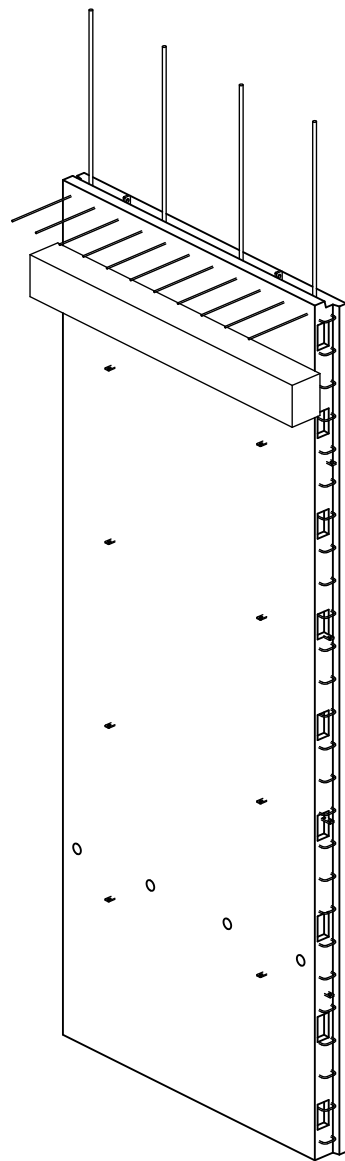


3D VIEW

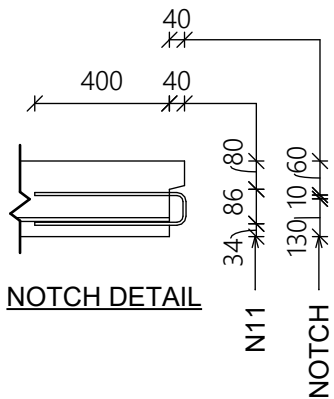

NOTCH DETAIL

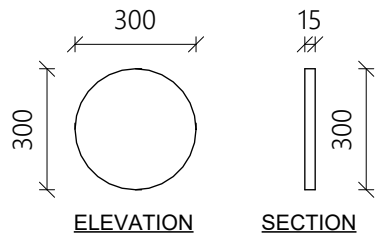

RECESS DETAIL

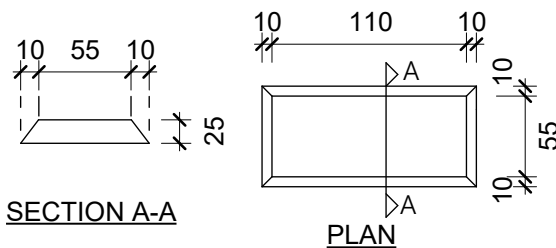

SECTION A-A

PLAN

TYPICAL SHEAR KEY DETAIL


**NOTE:** FOR REINFORCEMENT DETAILS  
REFER PW-GF-07

| Weight Schedule     |            |
|---------------------|------------|
| Volume              | Weight     |
| 2.09 m <sup>3</sup> | 5224.31 kg |


| Insert Schedule |                  |       |
|-----------------|------------------|-------|
| Ref No.         | Type             | Count |
| N1              | RR-SA-4.0-180    | 2     |
| N2              | RR-SA-1.4-160    | 8     |
| N3              | RR-SA-2.5-250    | 4     |
| N4              | 60 mm dowel tube | 4     |

| Dowel Bar Schedule |              |       |
|--------------------|--------------|-------|
| Ref.No             | Bar Diameter | Count |
| N15                | 20 mm        | 4     |

| U Bar & Projecting Bar Schedule |              |          |
|---------------------------------|--------------|----------|
| Ref.No                          | Bar Diameter | Quantity |
| N11                             | 8 mm         | 52       |
| N12                             | 8 mm         | 11       |

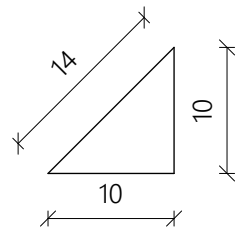

TYPICAL CHAMFER DETAIL

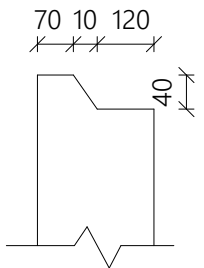

TOP NOTCH DETAIL

## PROJECT -: MF FACTORY

### GENERAL NOTES:

- GRADE OF CONCRETE - M40  
GRADE OF STEEL - Fe500  
STRIPPING STRENGTH - M20

### COVER

- WALL - 30mm  
CORBEL - 25mm

ALL DIMENSIONS ARE IN MM

### LEGENDS:

- ERECTION MARK -
- MOULD FACE -

### CONTRACTOR -:

#### VME Precast Products

 Arihant Esta, 2g2, 2<sup>nd</sup> floor,  
No.370, Church Road, Mogappair East,  
Chennai-600037.  
Tel:+91- 98400 - 41400 / 90802 - 22066

### STRUCTURAL CONSULTANT -:

#### ES STRUCTURAL CONSULTANT

 B167, 12th cross street, Jawahar Nagar,  
Palayamkottai, Tirunelveli-627007  
Cell No: +91 9865803764

|     |          |              |      |       |
|-----|----------|--------------|------|-------|
| 1   | 26-05-25 | FOR APPROVAL | PK   | PRC   |
| 0   | 08-05-25 | FOR APPROVAL | PK   | PRC   |
| Rev | Date     | Description  | Chkd | Appd. |

### REVISION SCHEDULE

### DRAWING TITLE -:

PW-GF-19-MOULD DRAWING

|                         |                 |
|-------------------------|-----------------|
| JOB NO. : ESP24075      | DRAWN BY:- AR   |
| ELEMENT NO. : PW-GF-19  | SHEET SIZE:- A3 |
| DWG. NO. : PW-GF-19(M2) | REV.NO:- 1      |
| SCALE : As indicated    | LEVEL. : GF     |