
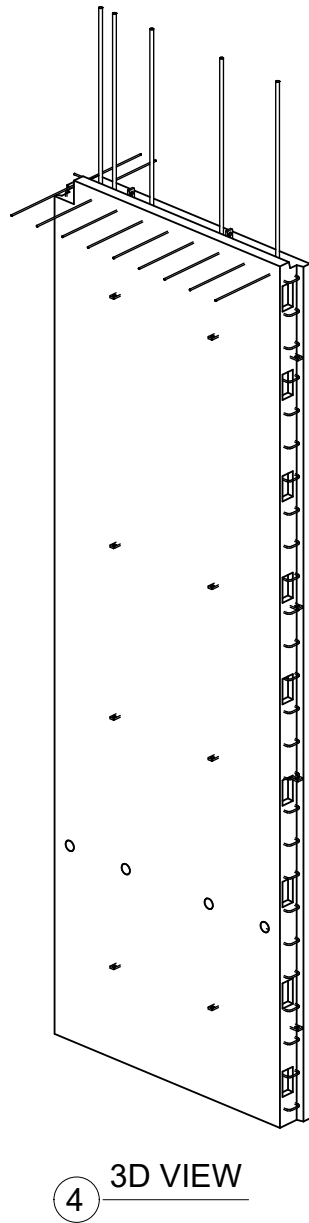
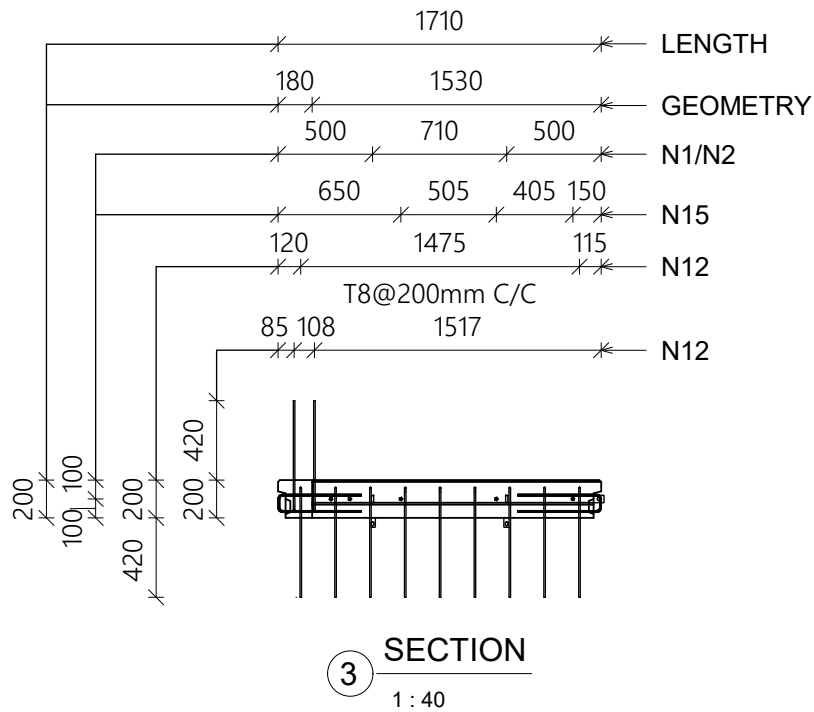






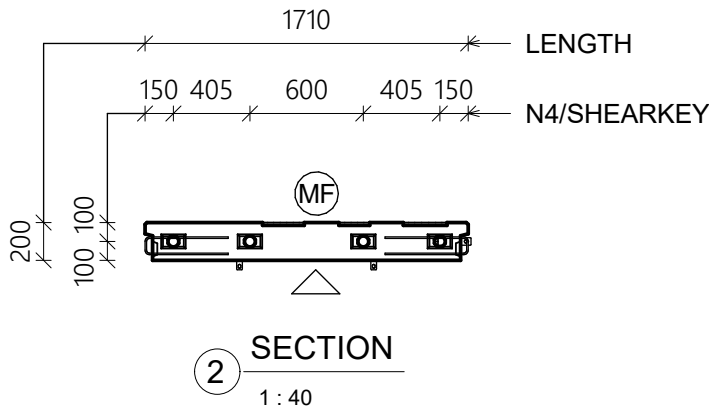


Weight Schedule	
Volume	Weight
1.65 m³	4122.53 kg

U-Bar & Dowel Bar &Schedule		
Ref.No	Bar Diameter	Count
N11	8 mm	51
N15	20 mm	5

Insert Schedule		
Ref No.	Type	Count
N1	RR-SA-4.0-180	2
N2	RR-SA-2.5-150	8
N3	RR-SA-3.0-200	4
N4	60 mm dowel tube	4

Projecting Bar Schedule		
Ref.No	Bar Diameter	Quantity
N12	8 mm	11

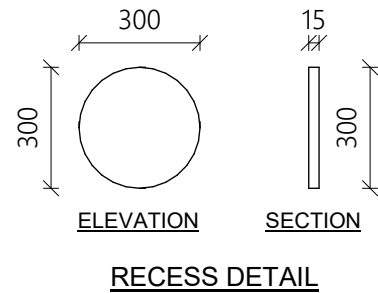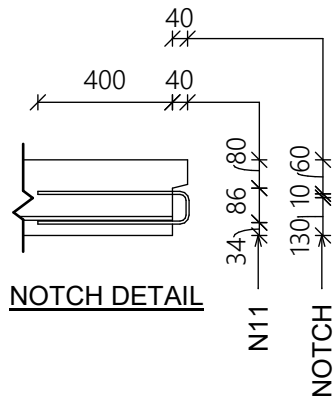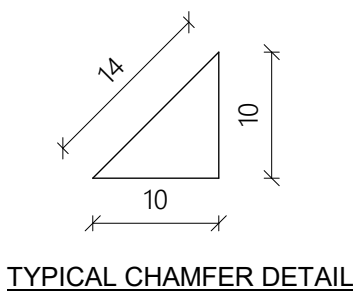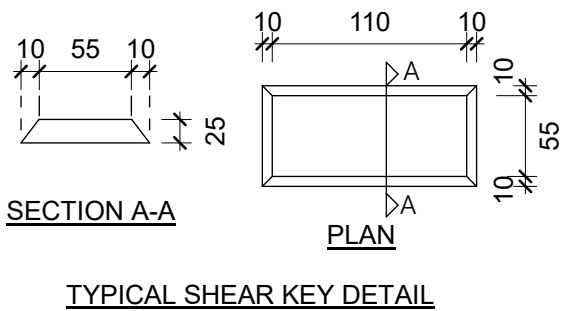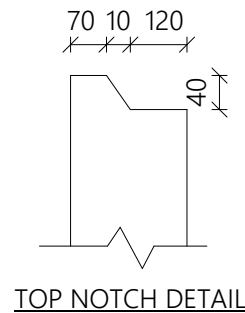

PROJECT -:
MF FACTORY

GENERAL NOTES:

GRADE OF CONCRETE - M40
GRADE OF STEEL - Fe500
STRIPPING STRENGTH - M20

COVER

WALL - 30mm
CORBEL - 25mm

ALL DIMENSIONS ARE IN MM

LEGENDS:

ERECTION MARK -

MOULD FACE -

CONTRACTOR -:

VME Precast Products
Arihant Esta, 2g2, 2nd floor,
No.370, Church Road, Mogappair East,
Chennai-600037.
Tel:+91- 98400 - 41400 / 90802 - 22066

STRUCTURAL CONSULTANT -:

ES STRUCTURAL CONSULTANT
B167, 12th cross street, Jawahar Nagar,
Palayamkottai, Tirunelveli-627007
Cell No: +91 9865803764

1	26-05-25	FOR APPROVAL	PK	PRC
0	21-04-25	FOR APPROVAL	PK	PRC
Rev	Date	Description	Chkd	Appd.

REVISION SCHEDULE

DRAWING TITLE -:

PW-GF-26-MOULD DRAWING

JOB NO. : ESP24075
ELEMENT NO. : PW-GF-26
DWG. NO. : PW-GF-26(M2)
SCALE : As indicated

DRAWN BY:- AR
SHEET SIZE:- A3
REV.NO:- 1
LEVEL. :