
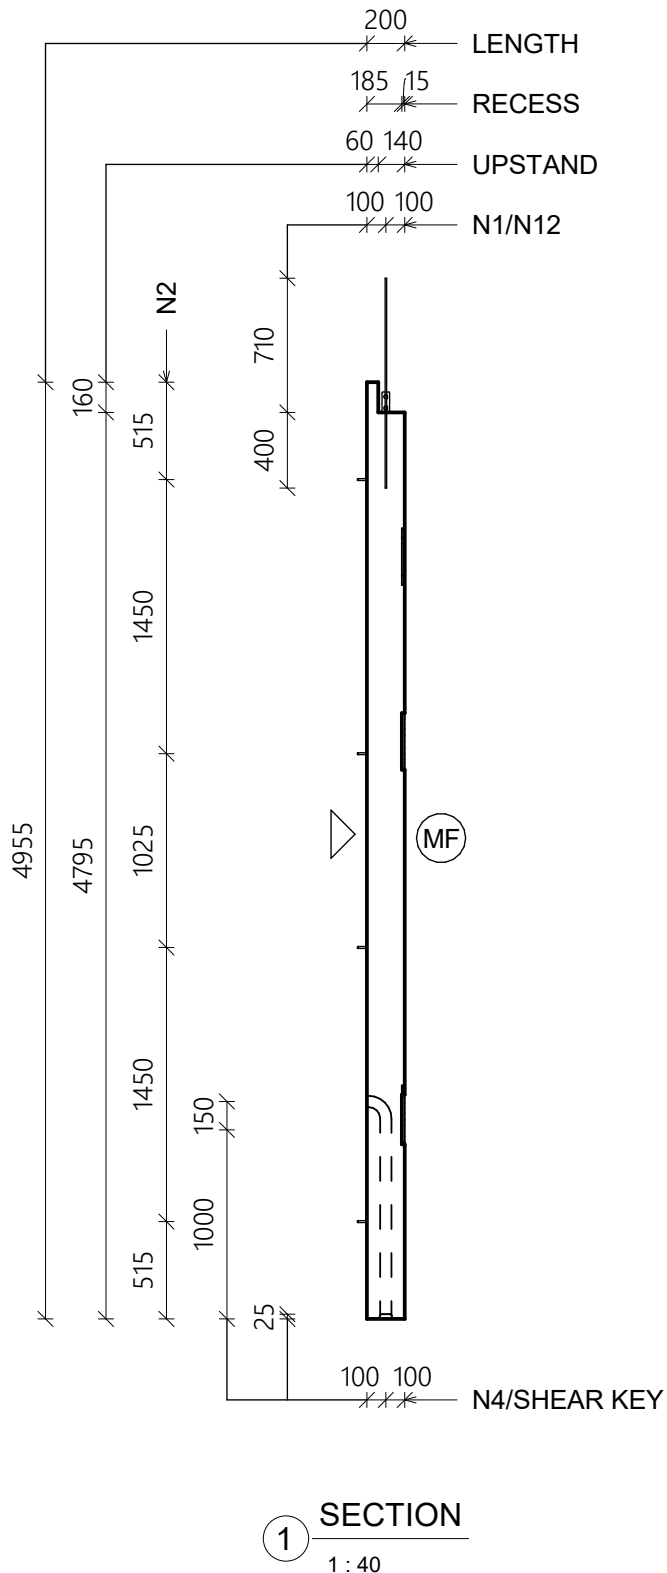
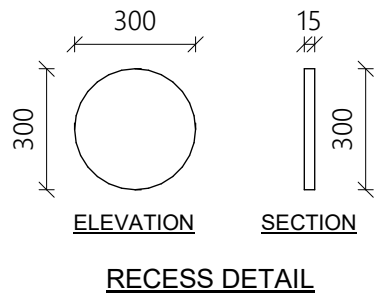
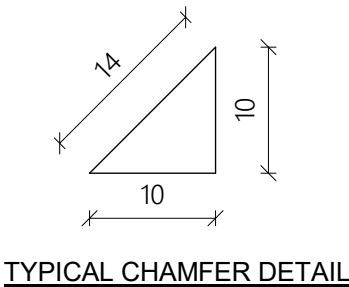


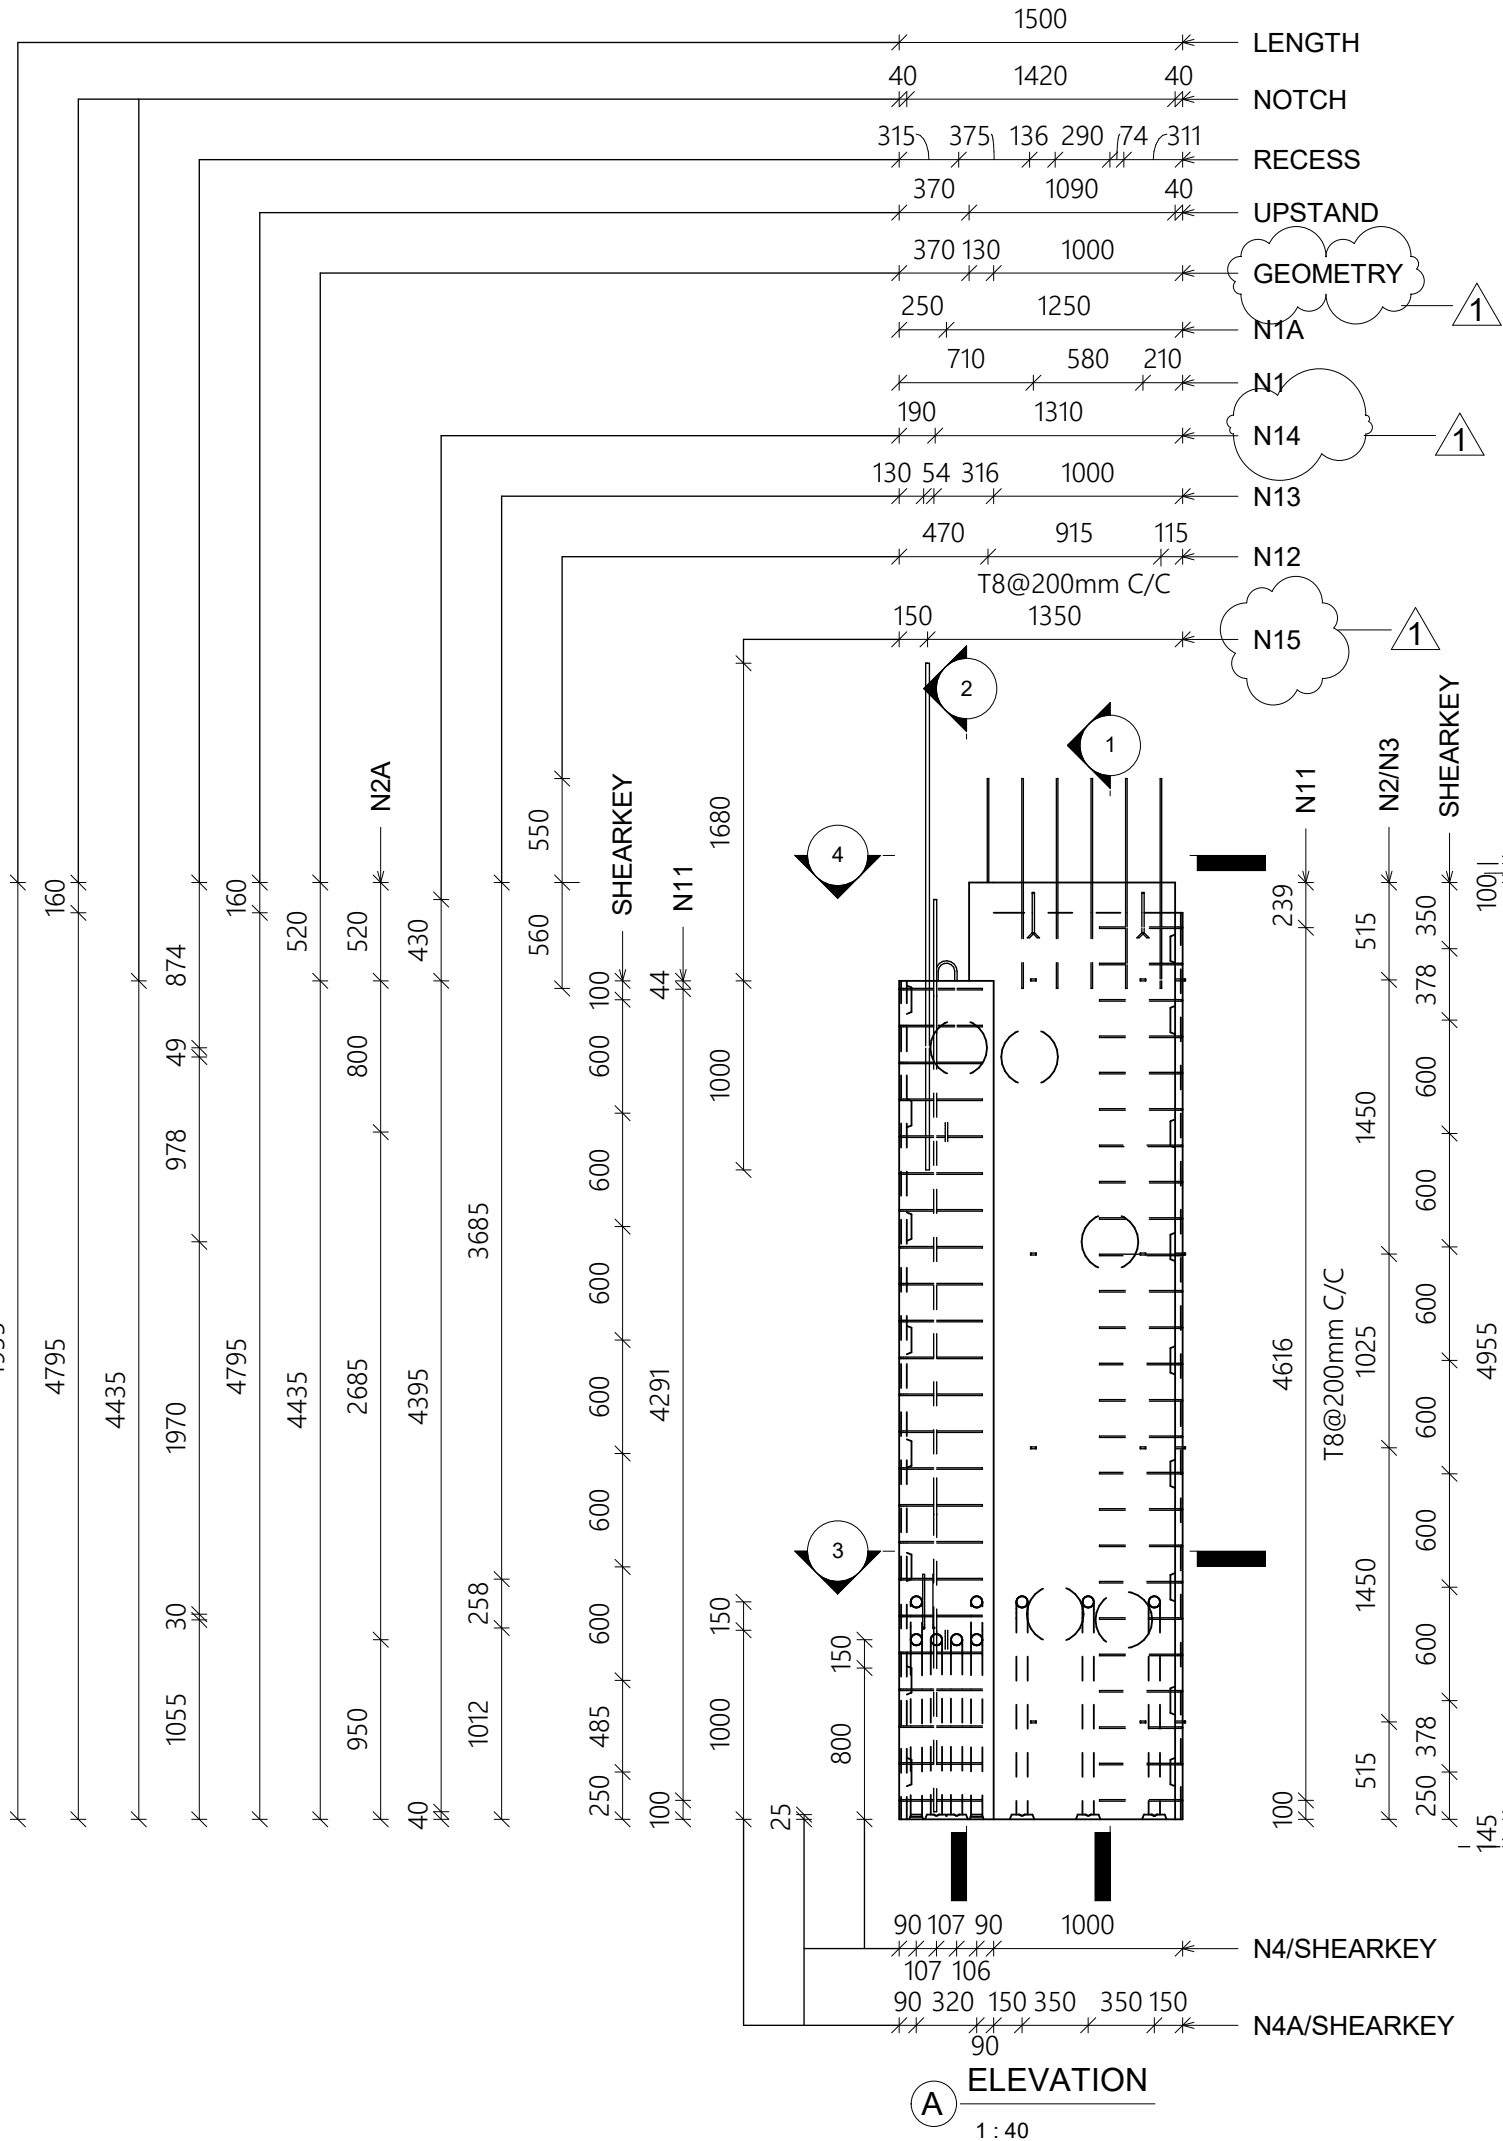

PROJECT :-
MF FACTORY

GENERAL NOTES:

GRADE OF CONCRETE

- M40

GRADE OF STEEL

- Fe500

STRIPPING STRENGTH

- M20

COVER

WALL

- 30mm

COLUMN

- 40mm

ALL DIMENSIONS ARE IN MM

LEGENDS:

ERECTION MARK

-

MOULD FACE

-

CONTRACTOR :-

VME Precast Products

Arihant Esta, 2g2, 2nd floor,
No.370, Church Road, Mogappair East,
Chennai-600037.
Tel:+91- 98400 - 41400 / 90802 - 22066

STRUCTURAL CONSULTANT :-

ES STRUCTURAL CONSULTANT

B167, 12th cross street, Jawahar Nagar,
Palayamkottai, Tirunelveli-627007
Cell No: +91 9865803764

1	02-06-25	REVISED AS PER COULDED	PK	PRC
0	26-05-25	FOR APPROVAL	PK	PRC
Rev	Date	Description	Chkd	Appd.

REVISION SCHEDULE

DRAWING TITLE :-

PW-GF-27-MOULD DRAWING

JOB NO. : ESP24075

ELEMENT NO. : PW-GF-27

DWG. NO. : PW-GF-27(M1)

SCALE : As indicated

DRAWN BY:- AR

SHEET SIZE:- A3

REV.NO:- 1

LEVEL. : GF