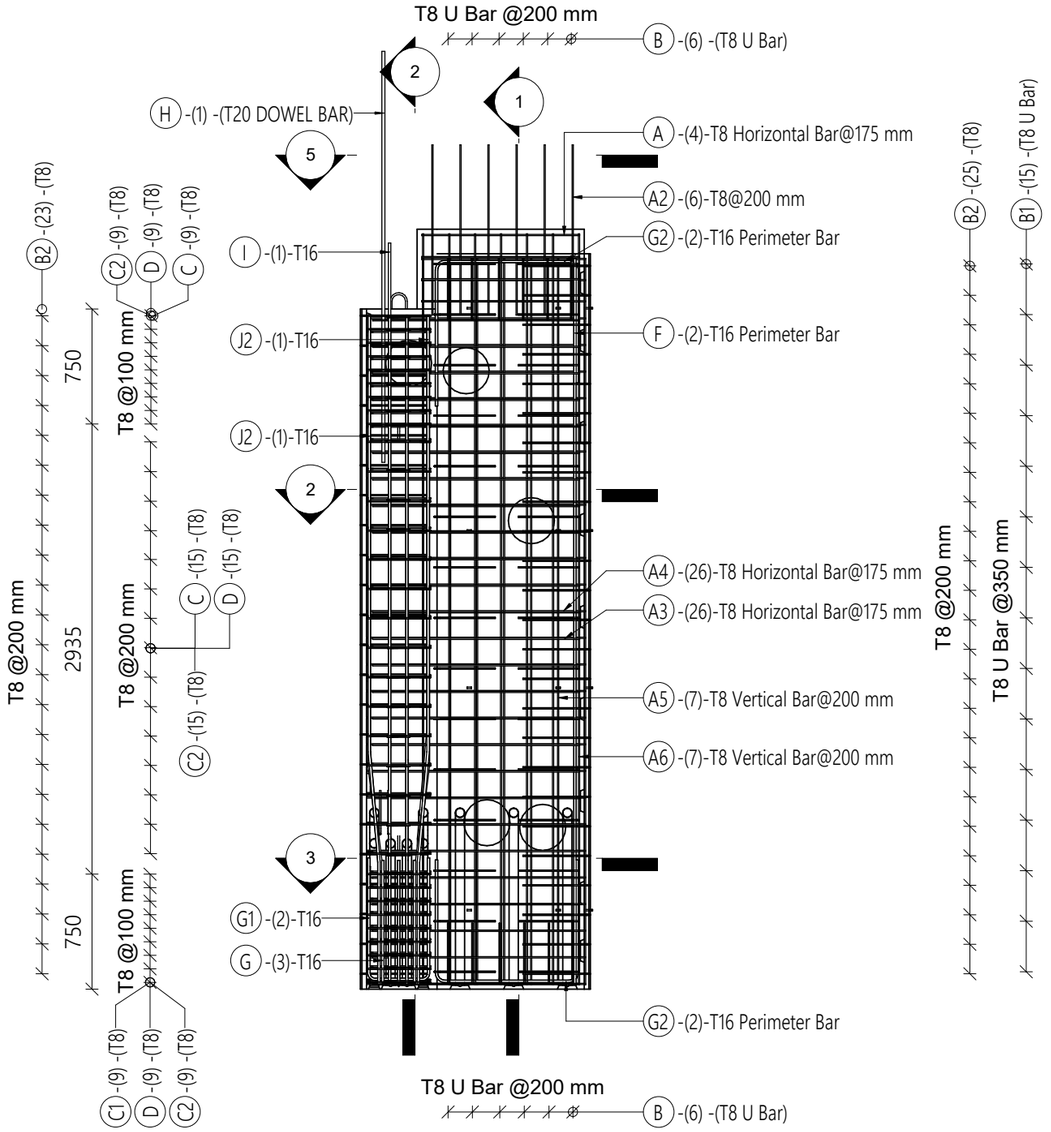

A ELEVATION (REINF)

1 : 40

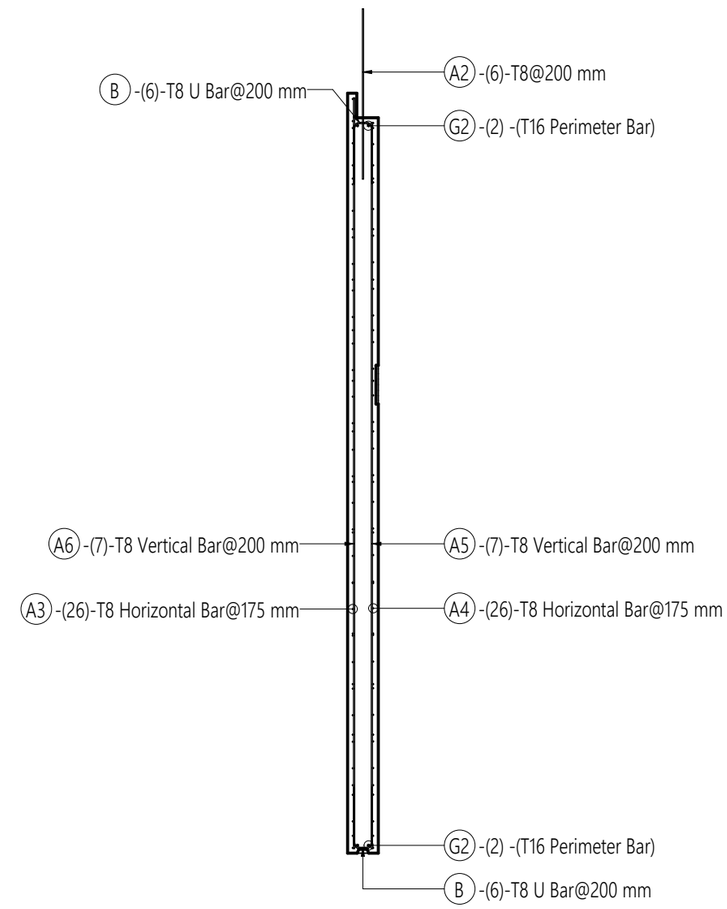

1 SECTION (REINF)

1 : 40

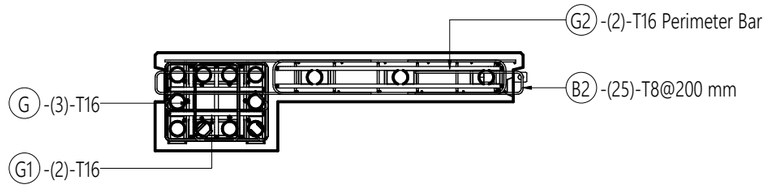

3 SECTION (REINF)

1 : 25

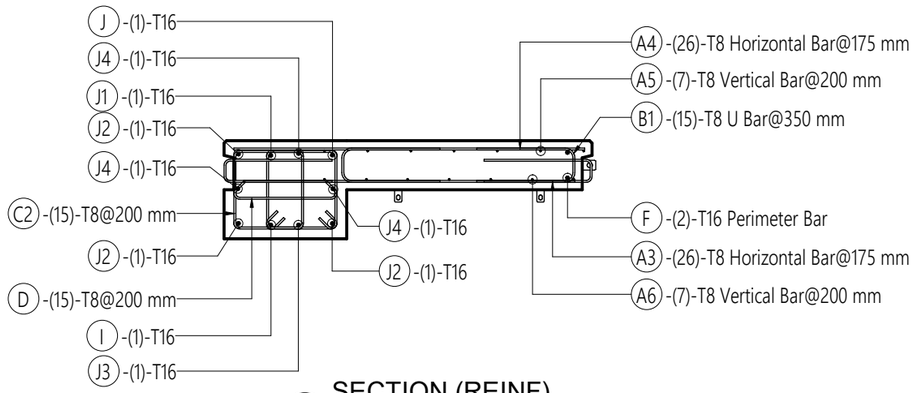

2 SECTION (REINF)

1 : 25

PROJECT -:
MF FACTORY

GENERAL NOTES:

GRADE OF CONCRETE	- M40
GRADE OF STEEL	- Fe500
STRIPPING STRENGTH	- M20

COVER

WALL	- 30mm
COLUMN	- 40mm

ALL DIMENSIONS ARE IN MM

LEGENDS:

ERECTION MARK - △

MOULD FACE - (MF)

CONTRACTOR -:

VME Precast Products

Arihant Esta, 2g2, 2nd floor,
No.370, Church Road, Mogappair East,
Chennai-600037.
Tel:+91- 98400 - 41400 / 90802 - 22066

STRUCTURAL CONSULTANT -:

ES STRUCTURAL CONSULTANT

B167, 12th cross street, Jawahar Nagar,
Palayamkottai, Tirunelveli-627007
Cell No: +91 9865803764

Rev	Date	Description	Chkd	Appd.
1	02-06-25	REVISED AS PER COLUDED	PK	PRC
0	26-05-25	FOR APPROVAL	PK	PRC

REVISION SCHEDULE

DRAWING TITLE -:

PW-GF-27-REINF DRAWING

JOB NO. : ESP24075	DRAWN BY:- AR
ELEMENT NO. : PW-GF-27	SHEET SIZE:- A3
DWG. NO. : PW-GF-27(R1)	REV.NO:- 1
SCALE : As indicated	LEVEL. : GF