



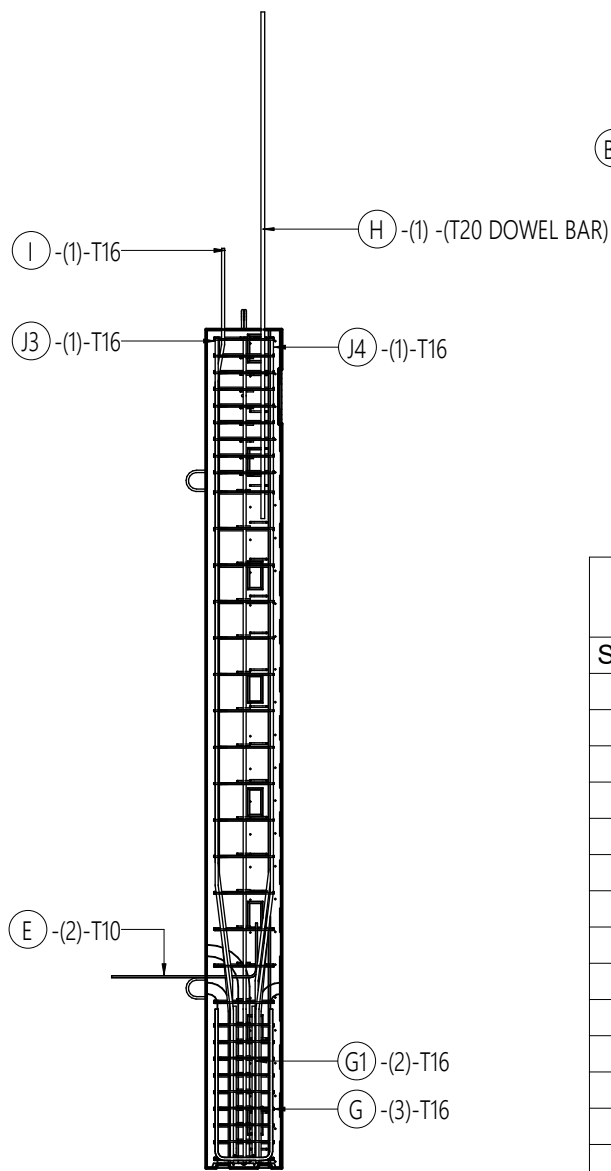

2 SECTION (REINF)
1 : 40

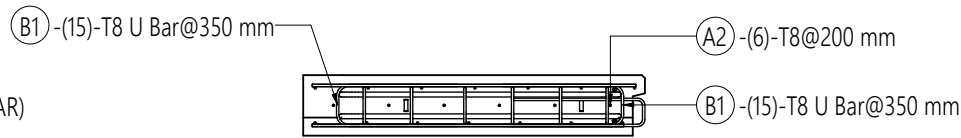

5 SECTION (REINF)
1 : 25

Summary Schedule		
Bar Diameter	Total Bar Length	Weight
8 mm	344200 mm	135.99 kg
10 mm	2100 mm	1.30 kg
16 mm	73375 mm	115.96 kg
20 mm	2700 mm	6.67 kg
422375 mm		259.91 kg

Rebar schedule for PW-GF-27(A)												
Schedule Mark	Bar Diameter	Shape	A	B	C	D	E	G	Bar Length	Total Bar Length	Quantity	Weight
A	8 mm	M_00	0 mm	1030 mm	0 mm	0 mm	0 mm	0 mm	1050 mm	4200 mm	4	1.66 kg
A1	8 mm	M_00	0 mm	1070 mm	0 mm	0 mm	0 mm	0 mm	1075 mm	3225 mm	3	1.27 kg
A2	8 mm	M_00	0 mm	1110 mm	0 mm	0 mm	0 mm	0 mm	1125 mm	6750 mm	6	2.67 kg
A3	8 mm	M_00	0 mm	1350 mm	0 mm	0 mm	0 mm	0 mm	1350 mm	35100 mm	26	13.87 kg
A4	8 mm	M_00	0 mm	1430 mm	0 mm	0 mm	0 mm	0 mm	1450 mm	37700 mm	26	14.89 kg
A5	8 mm	M_00	0 mm	4735 mm	0 mm	0 mm	0 mm	0 mm	4750 mm	33250 mm	7	13.14 kg
A6	8 mm	M_00	0 mm	4895 mm	0 mm	0 mm	0 mm	0 mm	4900 mm	34300 mm	7	13.55 kg
B	8 mm	M_17	0 mm	400 mm	120 mm	400 mm	0 mm	0 mm	900 mm	10800 mm	12	4.27 kg
B1	8 mm	M_17	0 mm	400 mm	140 mm	400 mm	0 mm	0 mm	900 mm	27000 mm	30	10.67 kg
B2	8 mm	M_17	0 mm	440 mm	90 mm	440 mm	0 mm	0 mm	950 mm	45600 mm	48	18.02 kg
C	8 mm	M_T1	70 mm	150 mm	320 mm	150 mm	320 mm	70 mm	1050 mm	25200 mm	24	9.96 kg
C1	8 mm	M_T1	70 mm	185 mm	320 mm	180 mm	320 mm	70 mm	1125 mm	10125 mm	9	4.00 kg
C2	8 mm	M_T1	70 mm	320 mm	420 mm	320 mm	420 mm	70 mm	1575 mm	51975 mm	33	20.53 kg
D	8 mm	M_T10	70 mm	420 mm	0 mm	0 mm	0 mm	70 mm	575 mm	18975 mm	33	7.50 kg
E	10 mm	M_17A	0 mm	285 mm	770 mm	0 mm	0 mm	0 mm	1050 mm	2100 mm	2	1.30 kg
F	16 mm	M_00	0 mm	4735 mm	0 mm	0 mm	0 mm	0 mm	4750 mm	9500 mm	2	15.01 kg
G	16 mm	M_17	0 mm	800 mm	300 mm	800 mm	0 mm	0 mm	1850 mm	5550 mm	3	8.77 kg
G1	16 mm	M_17	0 mm	800 mm	400 mm	800 mm	0 mm	0 mm	1950 mm	3900 mm	2	6.16 kg
G2	16 mm	M_17	0 mm	800 mm	930 mm	800 mm	0 mm	0 mm	2475 mm	4950 mm	2	7.82 kg
G2	16 mm	M_17	0 mm	950 mm	930 mm	800 mm	0 mm	0 mm	2625 mm	5250 mm	2	8.30 kg
H	20 mm	M_00	0 mm	2680 mm	0 mm	0 mm	0 mm	0 mm	2700 mm	2700 mm	1	6.67 kg
378150 mm										282	190.02 kg	

Rebar schedule for PW-GF-27(B)												
Schedule Mark	Bar Diameter	Shape	A	B	C	D	E	Bar Length	Total Bar Length	Quantity	Weight	
I	16 mm	Rebar Shape 30	950 mm	625 mm	2550 mm	195 mm	510 mm	4850 mm	4850 mm	1	7.66 kg	
4850 mm										1	7.66 kg	

Rebar schedule for PW-GF-27(C)									
Schedule Mark	Bar Diameter	Shape	A	B	C	Bar Length	Total Bar Length	Quantity	Weight
J	16 mm	26	935 mm	720 mm	2695 mm	4375 mm	4375 mm	1	6.91 kg
J1	16 mm	26	950 mm	590 mm	2815 mm	4375 mm	4375 mm	1	6.91 kg
J2	16 mm	26	795 mm	720 mm	2845 mm	4375 mm	13125 mm	3	20.74 kg
J3	16 mm	26	810 mm	660 mm	2900 mm	4375 mm	4375 mm	1	6.91 kg
J4	16 mm	26	810 mm	625 mm	2930 mm	4375 mm	13125 mm	3	20.74 kg
39375 mm								9	62.23 kg

PROJECT -: MF FACTORY

GENERAL NOTES:

GRADE OF CONCRETE	- M40
GRADE OF STEEL	- Fe500
STRIPPING STRENGTH	- M20

COVER

WALL	- 30mm
COLUMN	- 40mm

ALL DIMENSIONS ARE IN MM

LEGENDS:

ERECTION MARK	-	
MOULD FACE	-	

CONTRACTOR -:

VME Precast Products

 Arihant Esta, 2g2, 2nd floor,
No.370, Church Road, Mogappair East,
Chennai-600037.
Tel:+91- 98400 - 41400 / 90802 - 22066

STRUCTURAL CONSULTANT -:

 **ES STRUCTURAL CONSULTANT**
B167, 12th cross street, Jawahar Nagar,
Palayamkottai, Tirunelveli-627007
Cell No: +91 9865803764

1	02-06-25	REVISED AS PER COULDED	PK	PRC
0	26-05-25	FOR APPROVAL	PK	PRC
Rev	Date	Description	Chkd	Appd.

REVISION SCHEDULE

DRAWING TITLE -:

PW-GF-27-REINF DRAWING

JOB NO. : ESP24075	DRAWN BY:- AR
ELEMENT NO. : PW-GF-27	SHEET SIZE:- A3
DWG. NO. : PW-GF-27(R2)	REV.NO:- 1
SCALE : As indicated	LEVEL. : GF