
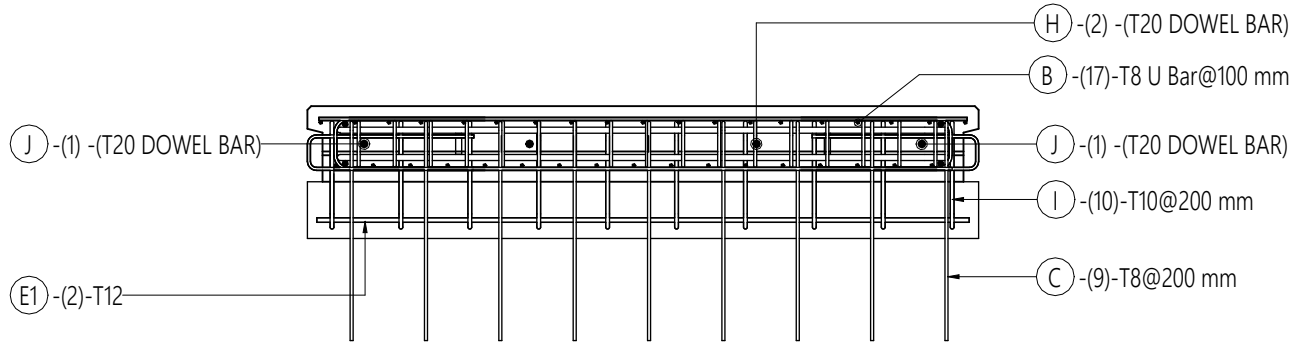
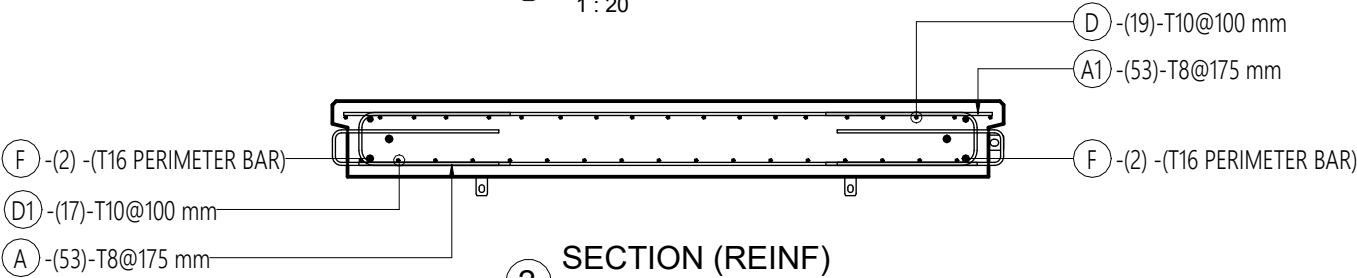


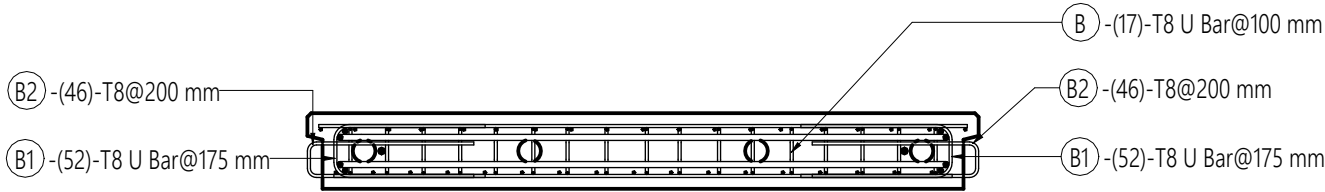

Rebar schedule for PW-GF-30(A)

Schedule Mark	Bar Diameter	Shape	B	C	D	Bar Length	Total Bar Length	Quantity	Weight
A	8 mm	M_00	1635 mm	0 mm	0 mm	1650 mm	87450 mm	53	34.55 kg
A1	8 mm	M_00	1715 mm	0 mm	0 mm	1725 mm	91425 mm	53	36.12 kg
B	8 mm	M_17	400 mm	120 mm	400 mm	900 mm	30600 mm	34	12.09 kg
B1	8 mm	M_17	400 mm	140 mm	400 mm	900 mm	93600 mm	104	36.98 kg
B2	8 mm	M_17	440 mm	90 mm	440 mm	950 mm	87400 mm	92	34.53 kg
C	8 mm	M_17A	580 mm	500 mm	0 mm	1075 mm	9675 mm	9	3.82 kg
D	10 mm	M_00	8995 mm	0 mm	0 mm	9000 mm	171000 mm	19	105.56 kg
D1	10 mm	M_00	9030 mm	0 mm	0 mm	9050 mm	153850 mm	17	94.98 kg
E	12 mm	M_00	1635 mm	0 mm	0 mm	1650 mm	3300 mm	2	2.93 kg
E1	12 mm	M_00	1725 mm	0 mm	0 mm	1725 mm	3450 mm	2	3.07 kg
F	16 mm	M_00	9035 mm	0 mm	0 mm	9050 mm	36200 mm	4	57.21 kg
G	16 mm	M_17	800 mm	1615 mm	800 mm	3150 mm	12600 mm	4	19.91 kg
H	20 mm	M_00	1670 mm	0 mm	0 mm	1675 mm	3350 mm	2	8.27 kg
							783900 mm	395	450.02 kg

Rebar schedule for PW-GF-30(B)

Schedule Mark	Bar Diameter	Shape	A	B	C	D	E	Bar Length	Total Bar Length	Quantity	Weight
I	10 mm	Rebar Shape 9	400 mm	270 mm	315 mm	285 mm	500 mm	1675 mm	16750 mm	10	10.34 kg
									16750 mm	10	10.34 kg

Rebar schedule for PW-GF-30(C)

Schedule Mark	Bar Diameter	Shape	A	B	C	Bar Length	Total Bar Length	Quantity	Weight
J	20 mm	26	1150 mm	285 mm	8300 mm	9750 mm	19500 mm	2	48.15 kg
							19500 mm	2	48.15 kg

Rebar Shape	Shape Image
M_00	
M_17	
Rebar Shape 9	
M_17A	
26	

Summary Schedule

Bar Diameter	Total Bar Length	Weight
8 mm	400150 mm	158.09 kg
10 mm	341600 mm	210.88 kg
12 mm	6750 mm	6.00 kg
16 mm	48800 mm	77.12 kg
20 mm	22850 mm	56.42 kg
		820150 mm 508.52 kg

PROJECT -:
MF FACTORY

GENERAL NOTES:

GRADE OF CONCRETE - M40
GRADE OF STEEL - Fe500
STRIPPING STRENGTH - M20

COVER

WALL - 30mm
CORBEL - 25mm

ALL DIMENSIONS ARE IN MM

LEGENDS:

ERECTION MARK -

MOULD FACE -

CONTRACTOR -:

VME Precast Products

 Arihant Esta, 2g2, 2nd floor,
No.370, Church Road, Mogappair East,
Chennai-600037.
Tel:+91- 98400 - 41400 / 90802 - 22066

STRUCTURAL CONSULTANT -:

 **ES STRUCTURAL CONSULTANT**
B167, 12th cross street, Jawahar Nagar,
Palayamkottai, Tirunelveli-627007
Cell No: +91 9865803764

1	26-05-25	FOR APPROVAL	PK	PRC
0	21-04-25	FOR APPROVAL	PK	PRC
Rev	Date	Description	Chkd	Appd.

REVISION SCHEDULE

DRAWING TITLE -:

PW-GF-30-REINF DRAWING

JOB NO. : ESP24075	DRAWN BY:- AR
ELEMENT NO. : PW-GF-30	SHEET SIZE:- A3
DWG. NO. : PW-GF-30(R2)	REV.NO:- 1
SCALE : 1 : 20	LEVEL. : GF