


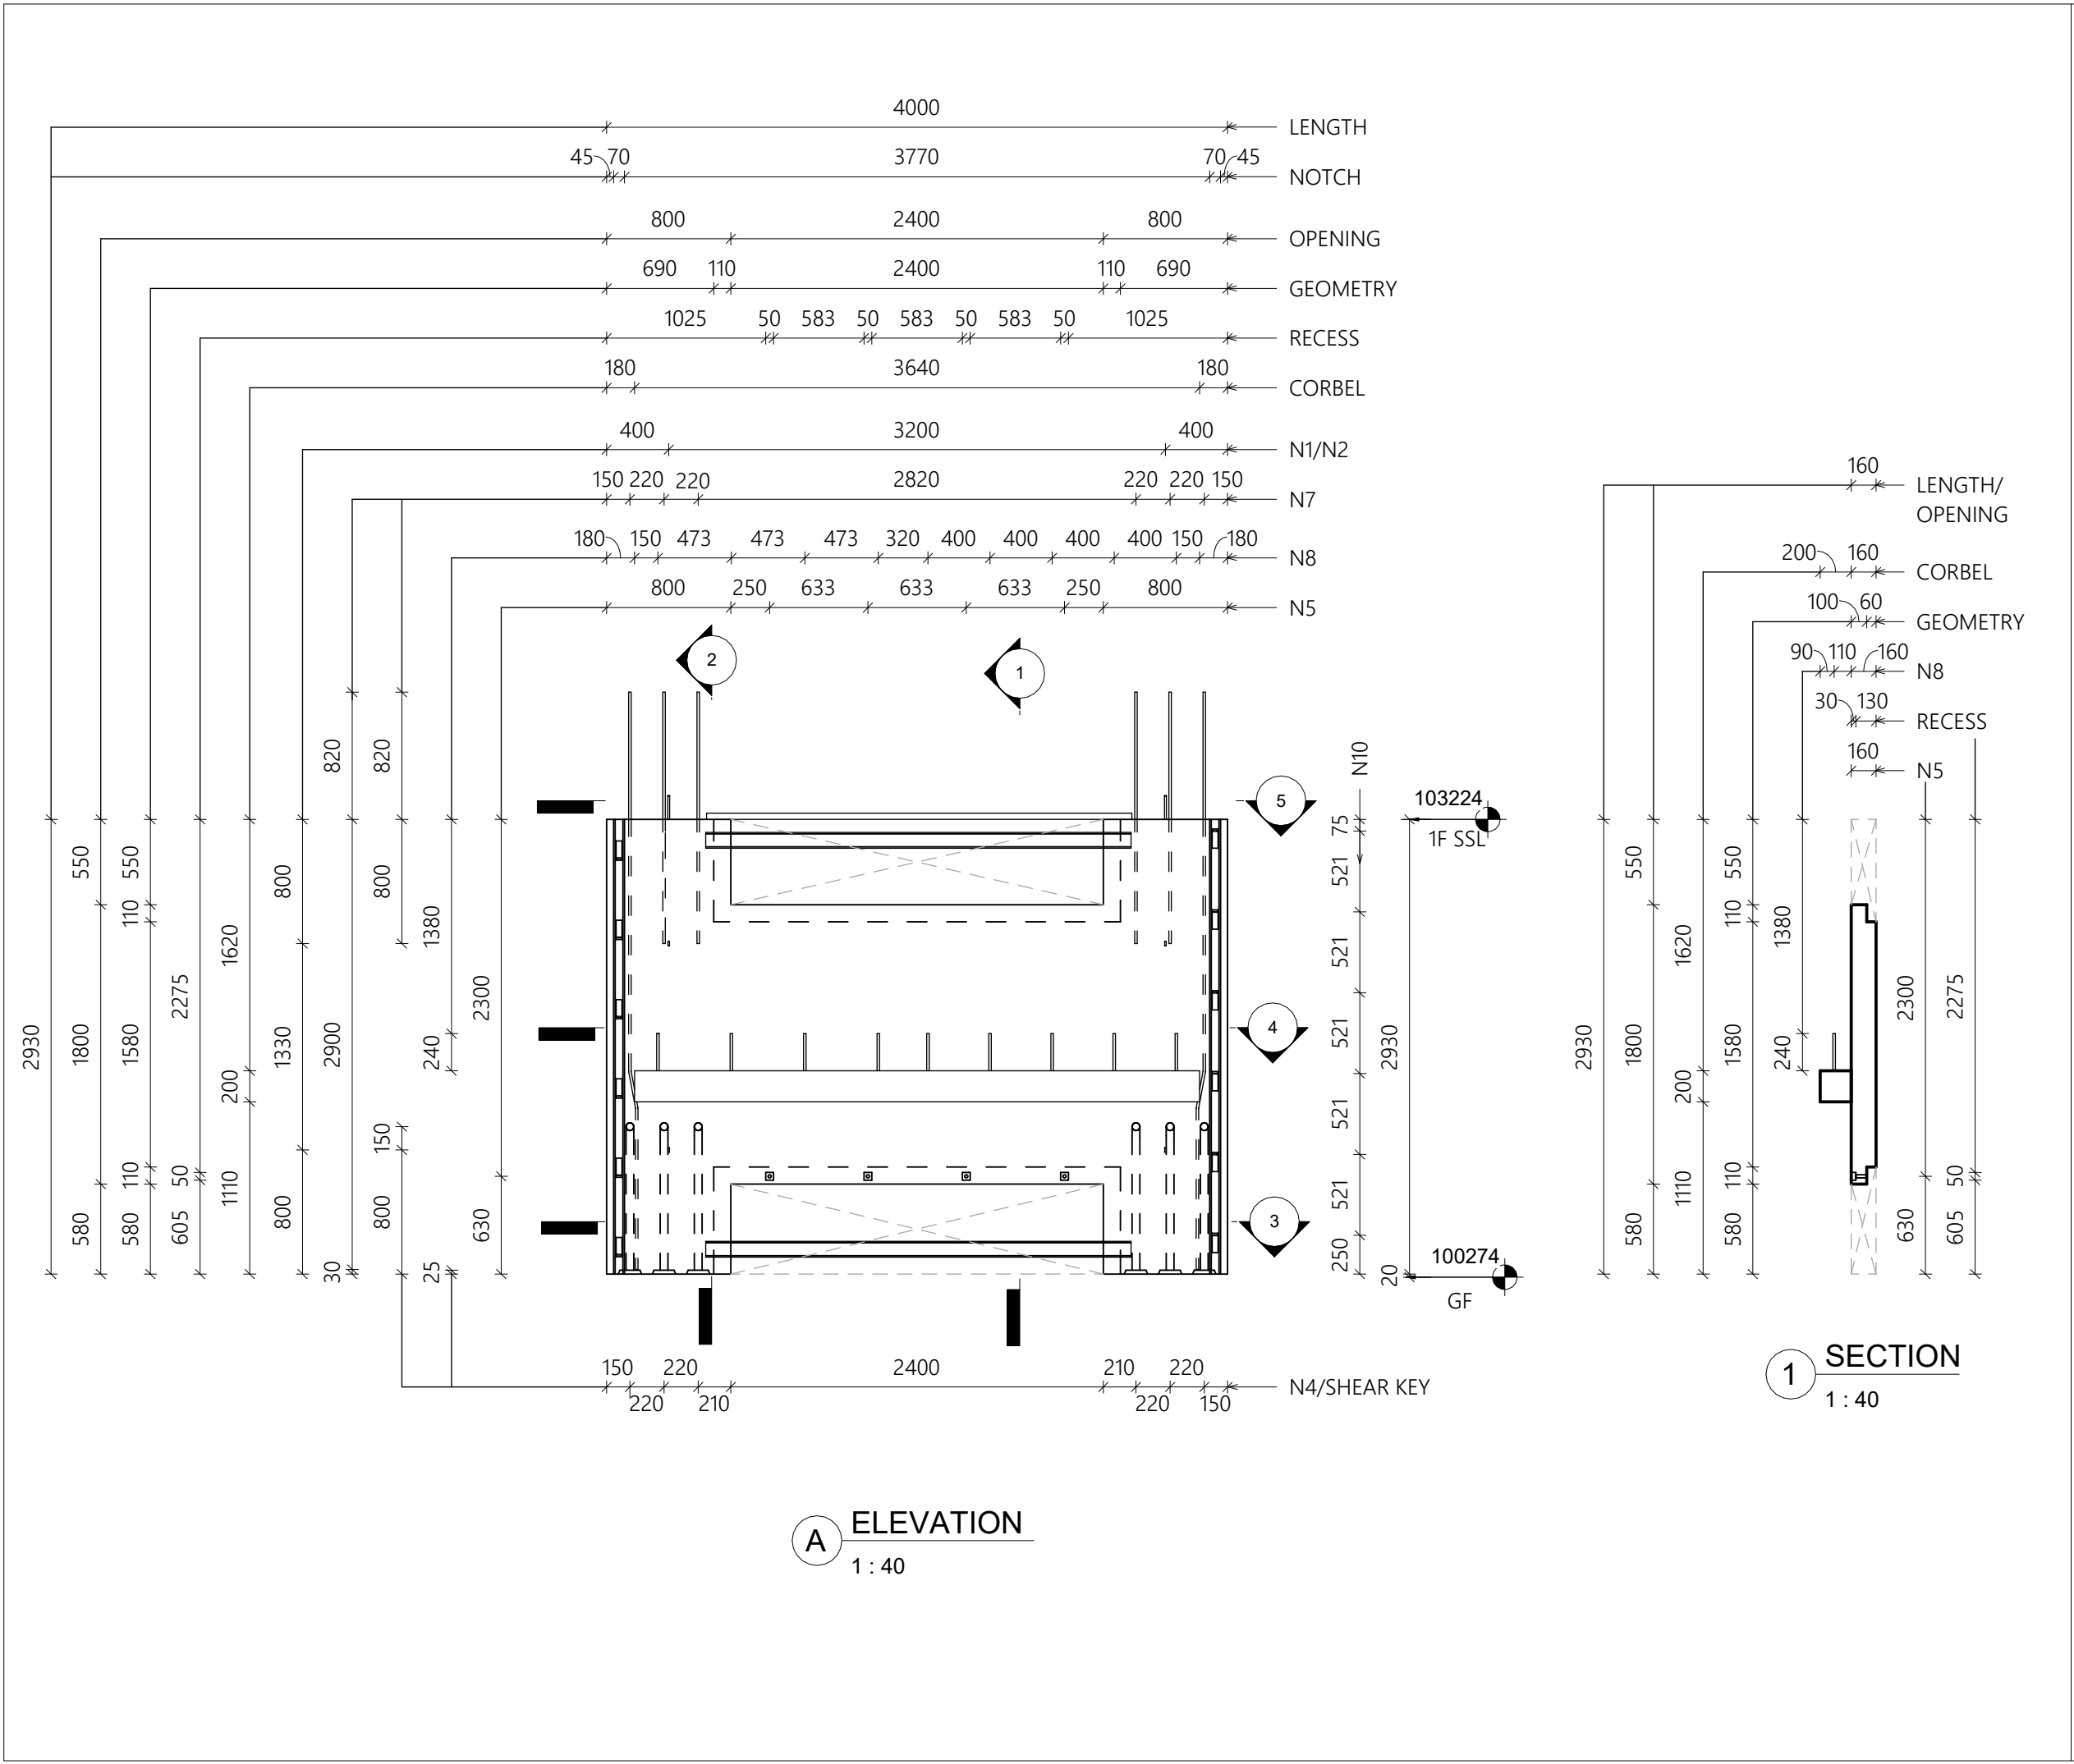

PROJECT -:

APOLLO GIRLS HOSTEL BUILDING
(RIGHT WING)-CHITTOOR

GENERAL NOTES:

GRADE OF CONCRETE

-

M40

GRADE OF STEEL

-

Fe550

STRIPPING STRENGTH

-

M20

LIFTING,TRANSPORTATION
AND ERECTION

-

M35

COVER:

WALL

-

30mm

ALL DIMENSIONS ARE IN MM

LEGENDS:

ERECTION MARK

-



MOULD FACE

-



CONTRACTOR -:



124,Eraiyr Road,Vallam (A) Village,
Sriperumbudur,Kanchipuram-602105,
Tamil Nadu,India Chennai-600 037,India

STRUCTURAL CONSULTANT -:



ES STRUCTURAL CONSULTANT
B167, 12th cross street, Jawahar Nagar,
Palayamkottai, Tirunelveli-627007
Cell No : +91 98658 03764

0	16-05-26	FOR PRODUCTION	GRS	PRC
Rev	Date	Description	Chkd	Appd.

REVISION SCHEDULE

DRAWING TITLE -:

PW-GF-09-MOULD DRAWING

ES JOB NO : ESP25087	DRAWN BY:- GMP
ELEMENT NO : PW-GF-09	SHEET SIZE:- A3
SHEET NO : PW-GF-09(M1)	REV.NO:- 0
SCALE : 1: 40	LEVEL :