




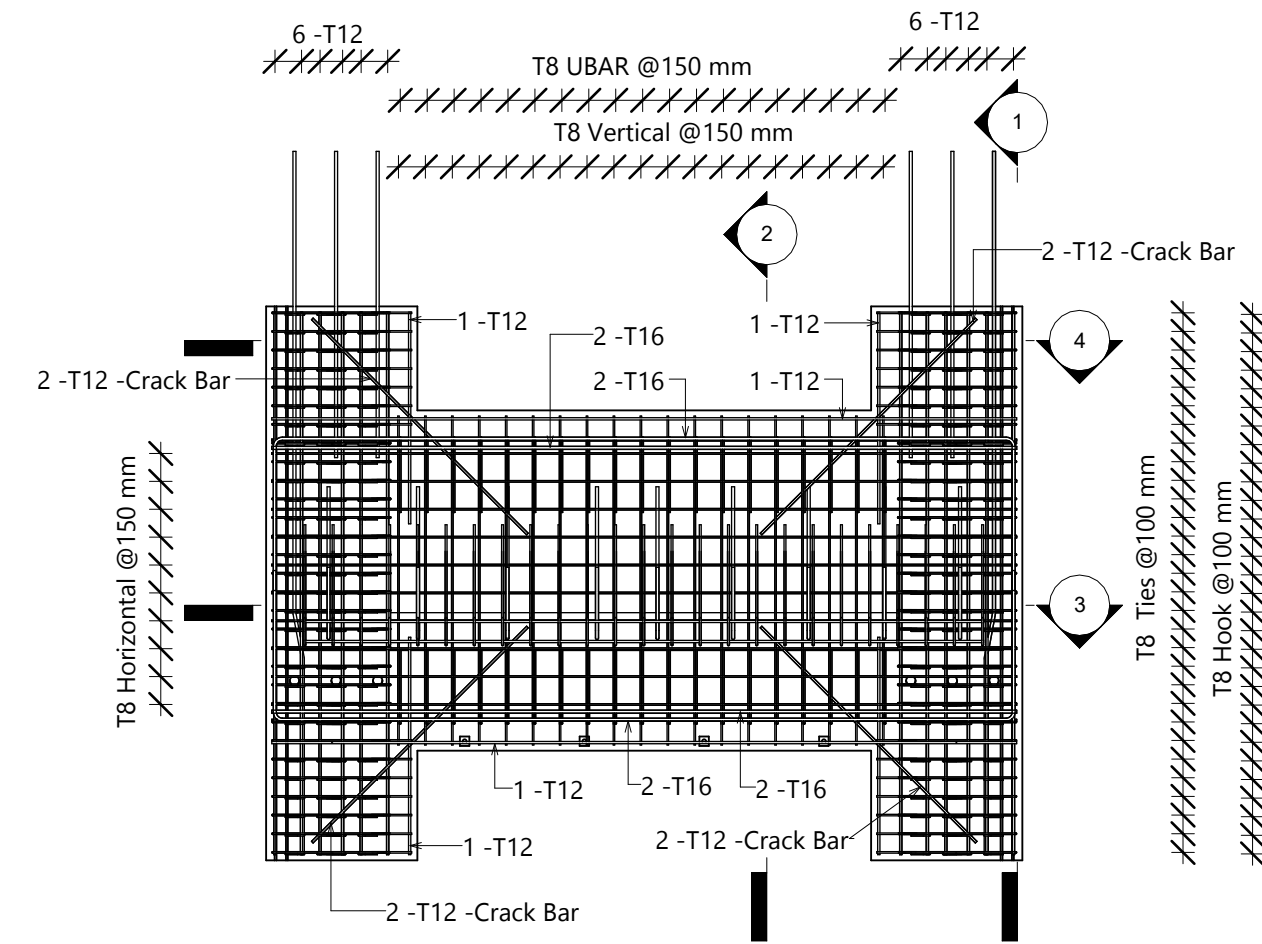


A ELEVATION(REINF)
1 : 40

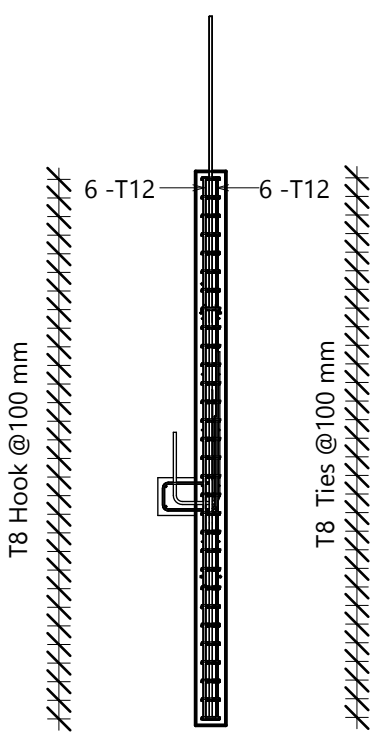


1 SECTION(REINF)
1 : 40

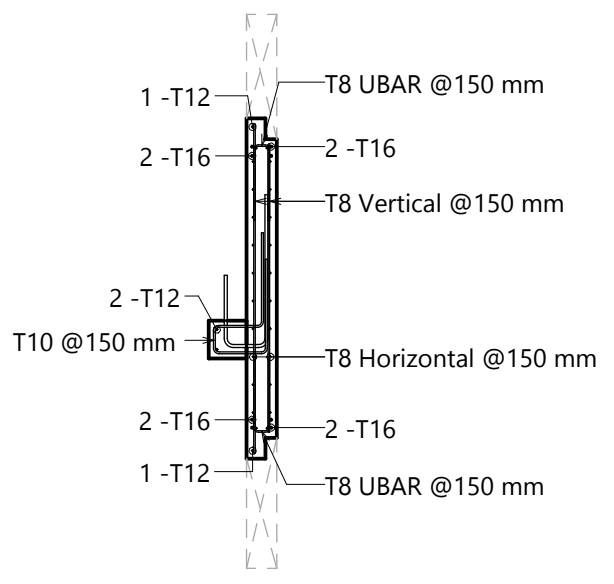

2 SECTION(REINF)
1 : 40

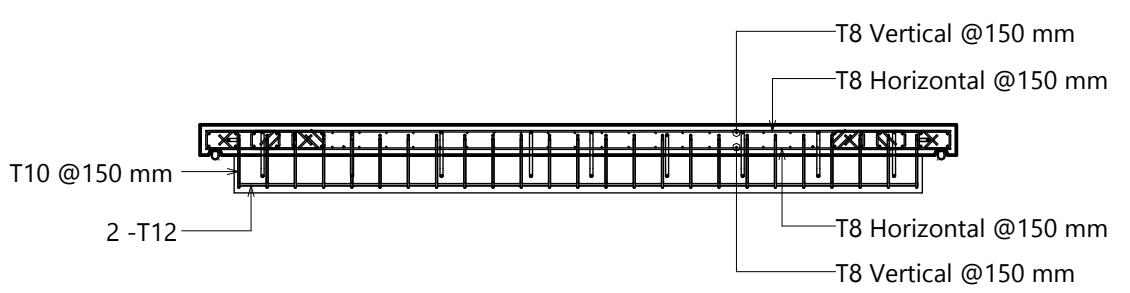

3 SECTION(REINF)
1 : 40

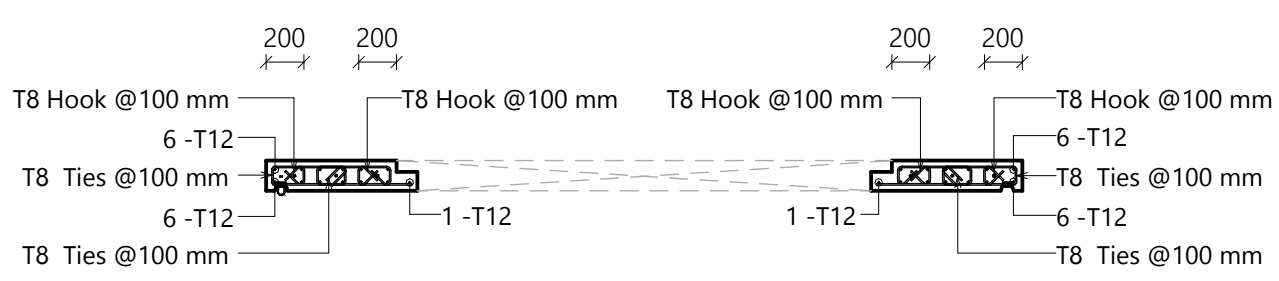

4 SECTION(REINF)
1 : 40

Summary Schedule		
Bar Diameter	Total Bar Length	Weight
8 mm	357475 mm	141.23 kg
10 mm	56425 mm	34.83 kg
12 mm	101650 mm	90.36 kg
16 mm	67800 mm	107.15 kg
	583350 mm	373.57 kg

NOTE:
REINFORCEMENT TYPICAL FOR ;
PW-GF-09,PW-1F-09,PW-2F-09,PW-3F-09,
PW-4F-09,PW-5F-09,PW-6F-09,PW-7F-09

NOTE:
LENGTH,LIFTING,DEMOULDING,DOWEL TUBE,
DOWEL BAR,PROJECTING BAR,U-BAR
REFER FOR INDIVIDUAL MOULD DRAWING

PROJECT -:
APOLLO GIRLS HOSTEL BUILDING
(RIGHT WING)-CHITTOOR

GENERAL NOTES:
GRADE OF CONCRETE - M40
GRADE OF STEEL - Fe550
STRIPPING STRENGTH - M20
LIFTING,TRANSPORTATION
AND ERECTION - M35

COVER:
WALL - 30mm
CORBEL - 25mm
ALL DIMENSIONS ARE IN MM

LEGENDS:
ERECTION MARK - 
MOULD FACE - 

CONTRACTOR -:
VME PRECAST PRODUCTS
 124,Eraiyr Road,Vallam (A) Village,
Sriperumbudur,Kanchipuram-602105,
Tamil Nadu,India Chennai-600 037,India

STRUCTURAL CONSULTANT -:
 ES STRUCTURAL CONSULTANT
B167, 12th cross street, Jawahar Nagar,
Palayamkottai, Tirunelveli-627007
Cell No : +91 98658 03764

0	17-05-26	FOR PRODUCTION	ELA	PRC
Rev	Date	Description	Chkd	Appd.

REVISION SCHEDULE

DRAWING TITLE -:
PW-GF-09-REINF DRAWING

ES JOB NO : ESP25087	DRAWN BY:- GRS
ELEMENT NO : PW-GF-09	SHEET SIZE:- A3
SHEET NO : PW-GF-09(R)	REV.NO:- 0
SCALE : 1 : 40	LEVEL :