


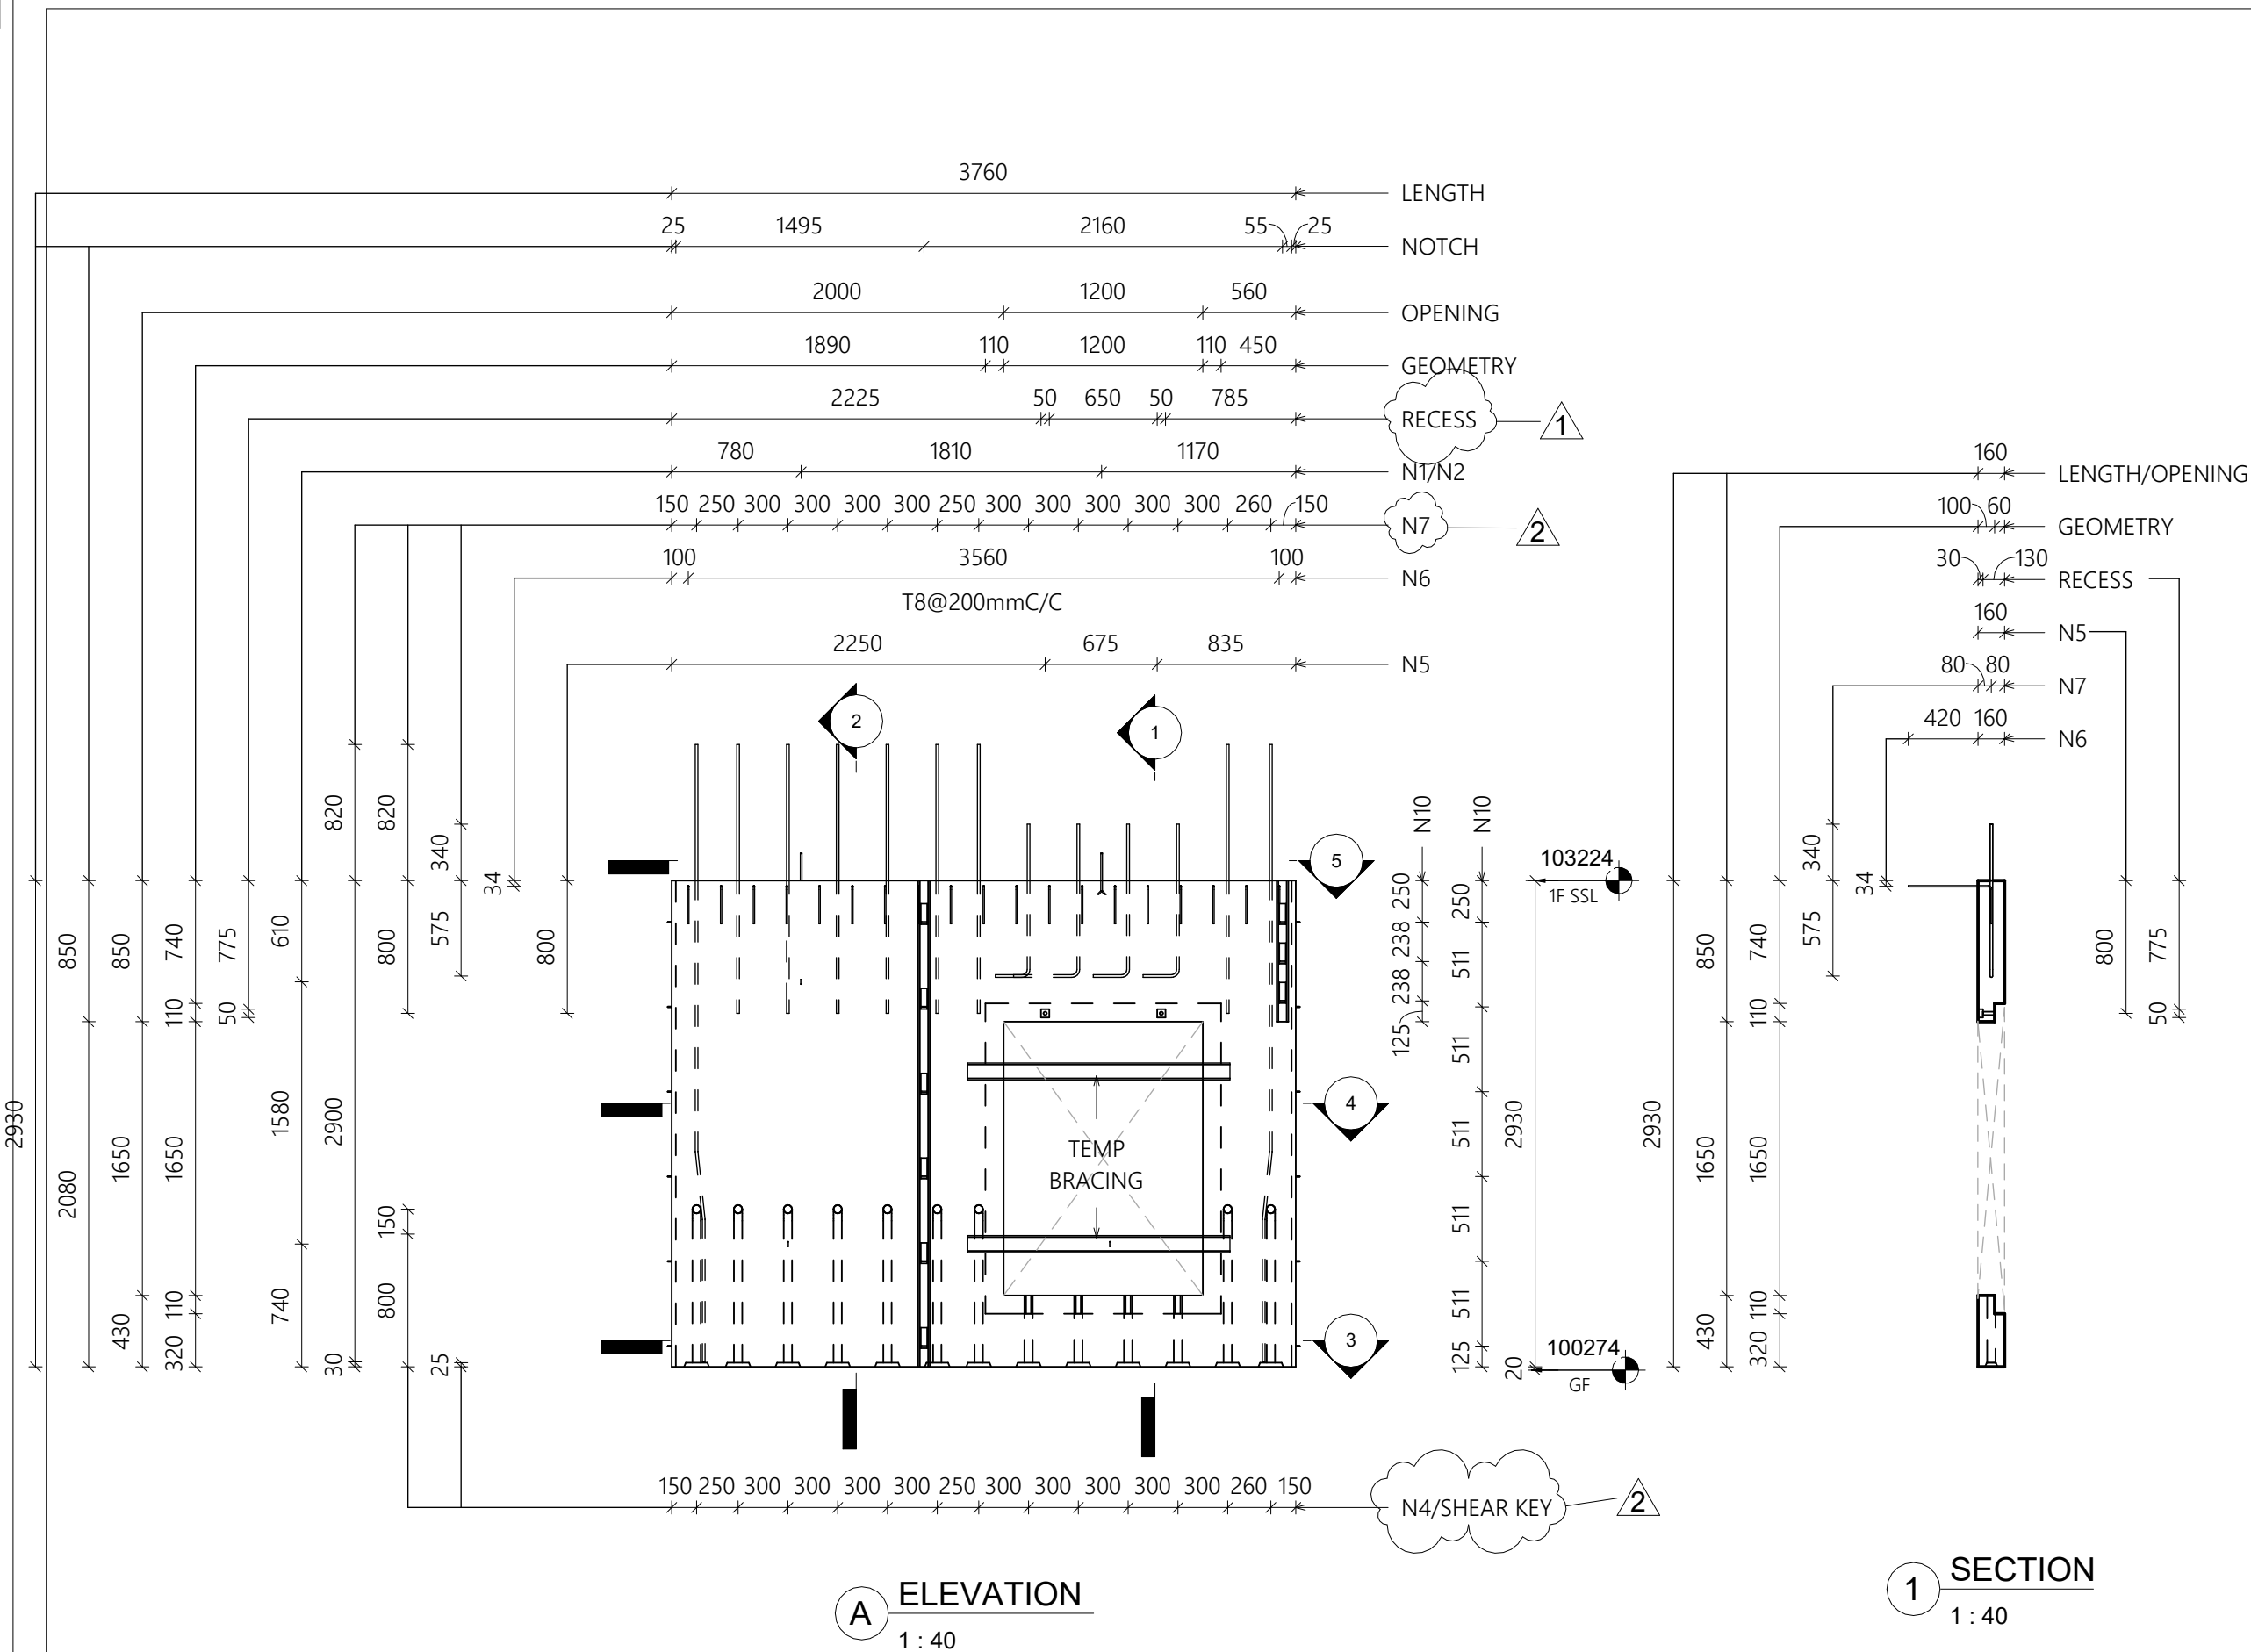

PROJECT -:

APOLLO GIRLS HOSTEL BUILDING
(RIGHT WING)-CHITTOOR

GENERAL NOTES:

GRADE OF CONCRETE - M40

GRADE OF STEEL - Fe550

STRIPPING STRENGTH - M20

LIFTING,TRANSPORTATION
AND ERECTION - M35

COVER:

WALL - 30mm

ALL DIMENSIONS ARE IN MM

LEGENDS:

ERECTION MARK -

MOULD FACE -

CONTRACTOR -:

VME PRECAST PRODUCTS

 124,Eraiyr Road,Vallam (A) Village,
Sriperumbudur,Kanchipuram-602105,
Tamil Nadu,India Chennai-600 037,India

STRUCTURAL CONSULTANT -:

ES STRUCTURAL CONSULTANT

 B167, 12th cross street, Jawahar Nagar,
Palayamkottai, Tirunelveli-627007
Cell No : +91 98658 03764

2	16-05-26	REVISED AS PER CLOUDED	GRS	PRC
1	15-05-26	REVISED AS PER CLOUDED	GRS	PRC
0	05-05-26	FOR PRODUCTION	GRS	PRC
Rev	Date	Description	Chkd	Appd.

REVISION SCHEDULE

DRAWING TITLE -:

PW-GF-02-MOULD DRAWING

ES JOB NO : ESP25087	DRAWN BY:- GMP
ELEMENT NO : PW-GF-02	SHEET SIZE:- A3
SHEET NO : PW-GF-02(M1)	REV.NO:- 2
SCALE : 1 : 40	LEVEL :