




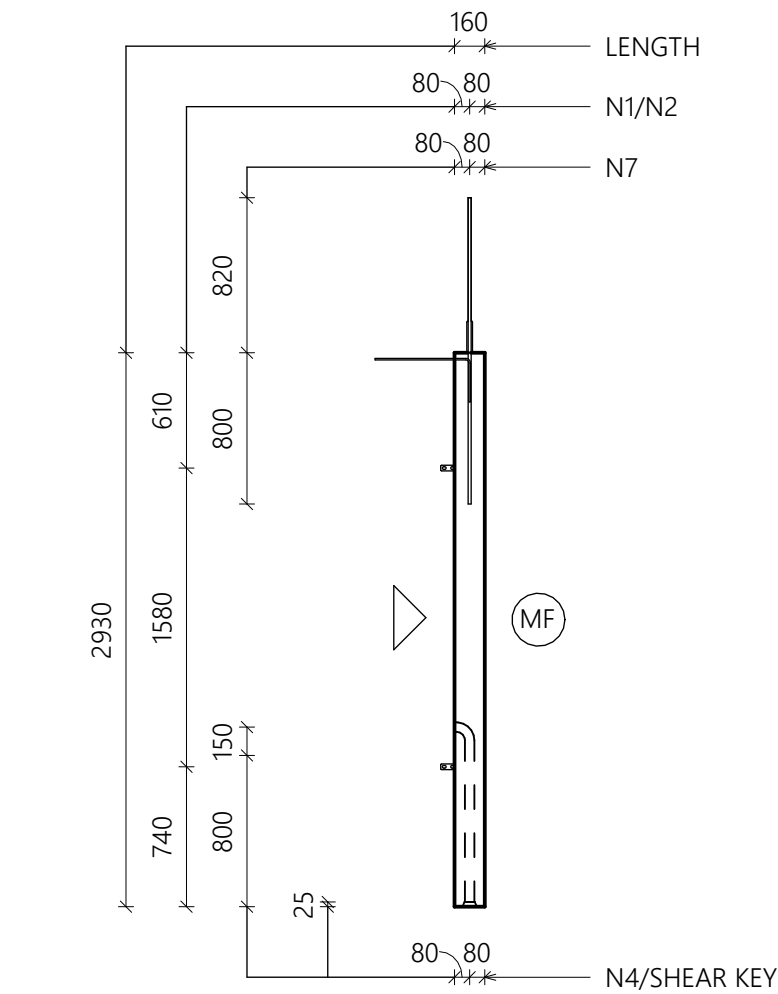


2 SECTION
1 : 40

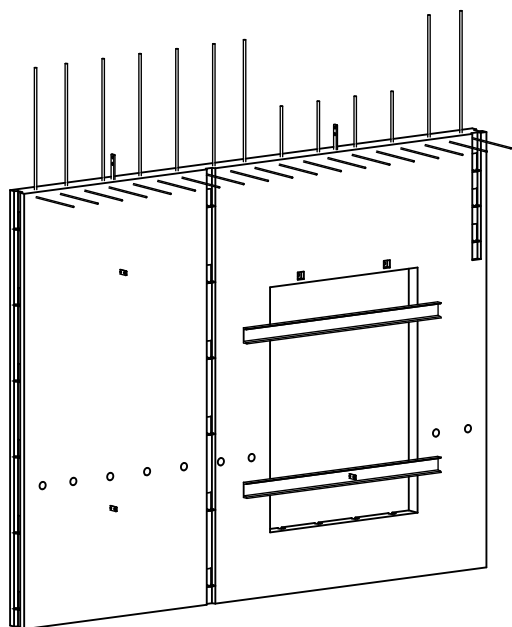


6 3D VIEW

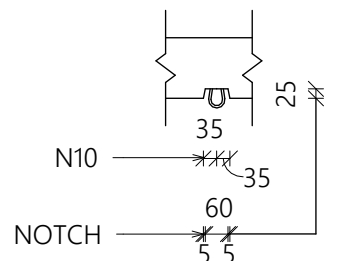


NOTCH DETAIL-A

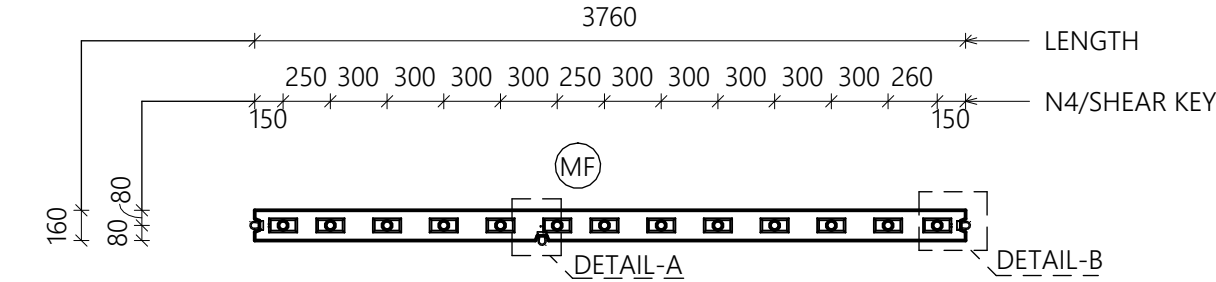

3 SECTION
1 : 40

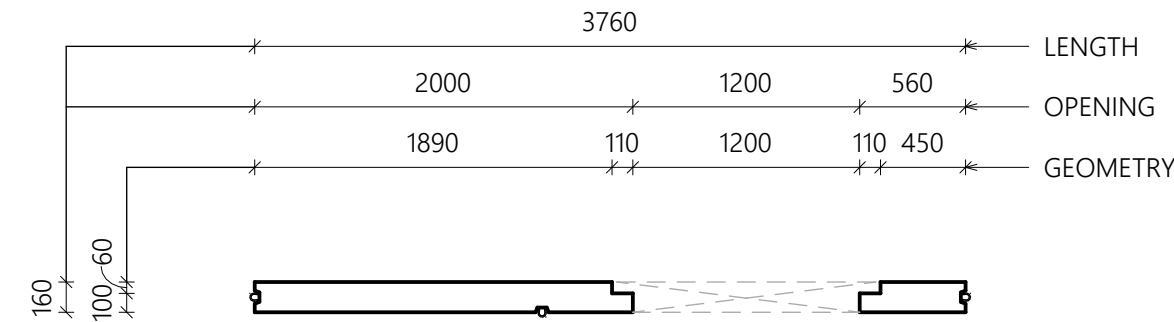

4 SECTION
1 : 40

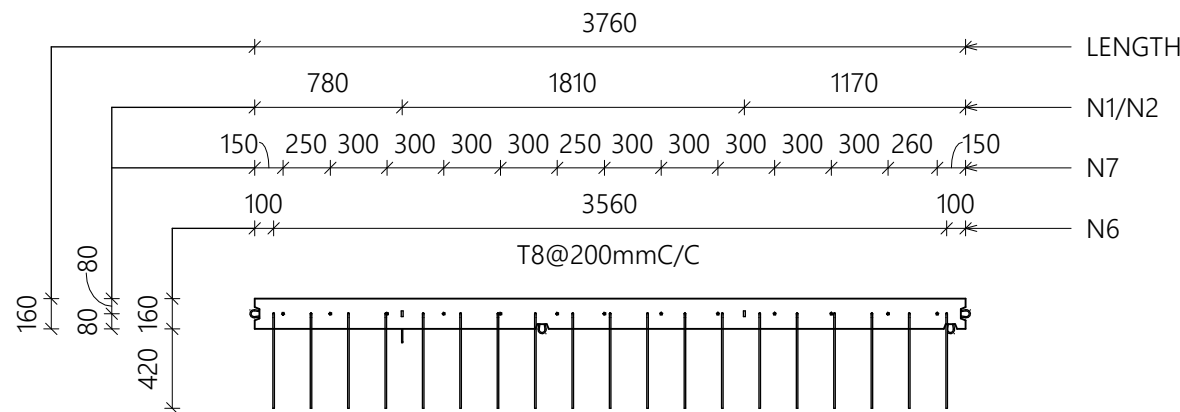

5 SECTION
1 : 40

Dowel Bar Schedule		
Ref No	Bar Diameter	Count
N7	16 mm	13

Projecting Bar Schedule		
Ref No	Bar Diameter	Count
N6	8 mm	19

Weight Schedule	
Volume	Weight
1.37 m ³	3419.86 kg

Insert Schedule		
Ref No	Type	Count
N1	RR-SA-2.5-250	2
N2	RR-SA-1.4-160	3
N4	50 DIA SLEEVE	13
N5	20 Dia Sleeve	2
N10	Wire Loop	21

PROJECT -:

APOLLO GIRLS HOSTEL BUILDING
(RIGHT WING)-CHITTOOR

GENERAL NOTES:

GRADE OF CONCRETE	-	M40
GRADE OF STEEL	-	Fe550
STRIPPING STRENGTH	-	M20
LIFTING,TRANSPORTATION AND ERECTION	-	M35

COVER:

WALL	-	30mm
------	---	------

ALL DIMENSIONS ARE IN MM

LEGENDS:

ERECTION MARK	-	
MOULD FACE	-	

CONTRACTOR -:

VME PRECAST PRODUCTS

 124,Eraiur Road,Vallam (A) Village,
Sriperumbudur,Kanchipuram-602105,
Tamil Nadu,India Chennai-600 037,India

STRUCTURAL CONSULTANT -:

 ES STRUCTURAL CONSULTANT
B167, 12th cross street, Jawahar Nagar,
Palayamkottai, Tirunelveli-627007
Cell No : +91 98658 03764

2	16-05-26	REVISED AS PER CLOUDED	GRS	PRC
1	15-05-26	REVISED AS PER CLOUDED	GRS	PRC
0	05-05-26	FOR PRODUCTION	GRS	PRC
Rev	Date	Description	Chkd	Appd.

REVISION SCHEDULE

DRAWING TITLE -:

PW-GF-02-MOULD DRAWING

ES JOB NO : ESP25087	DRAWN BY:- GMP
ELEMENT NO : PW-GF-02	SHEET SIZE:- A3
SHEET NO : PW-GF-02(M2)	REV.NO:- 2
SCALE : As indicated	LEVEL :