




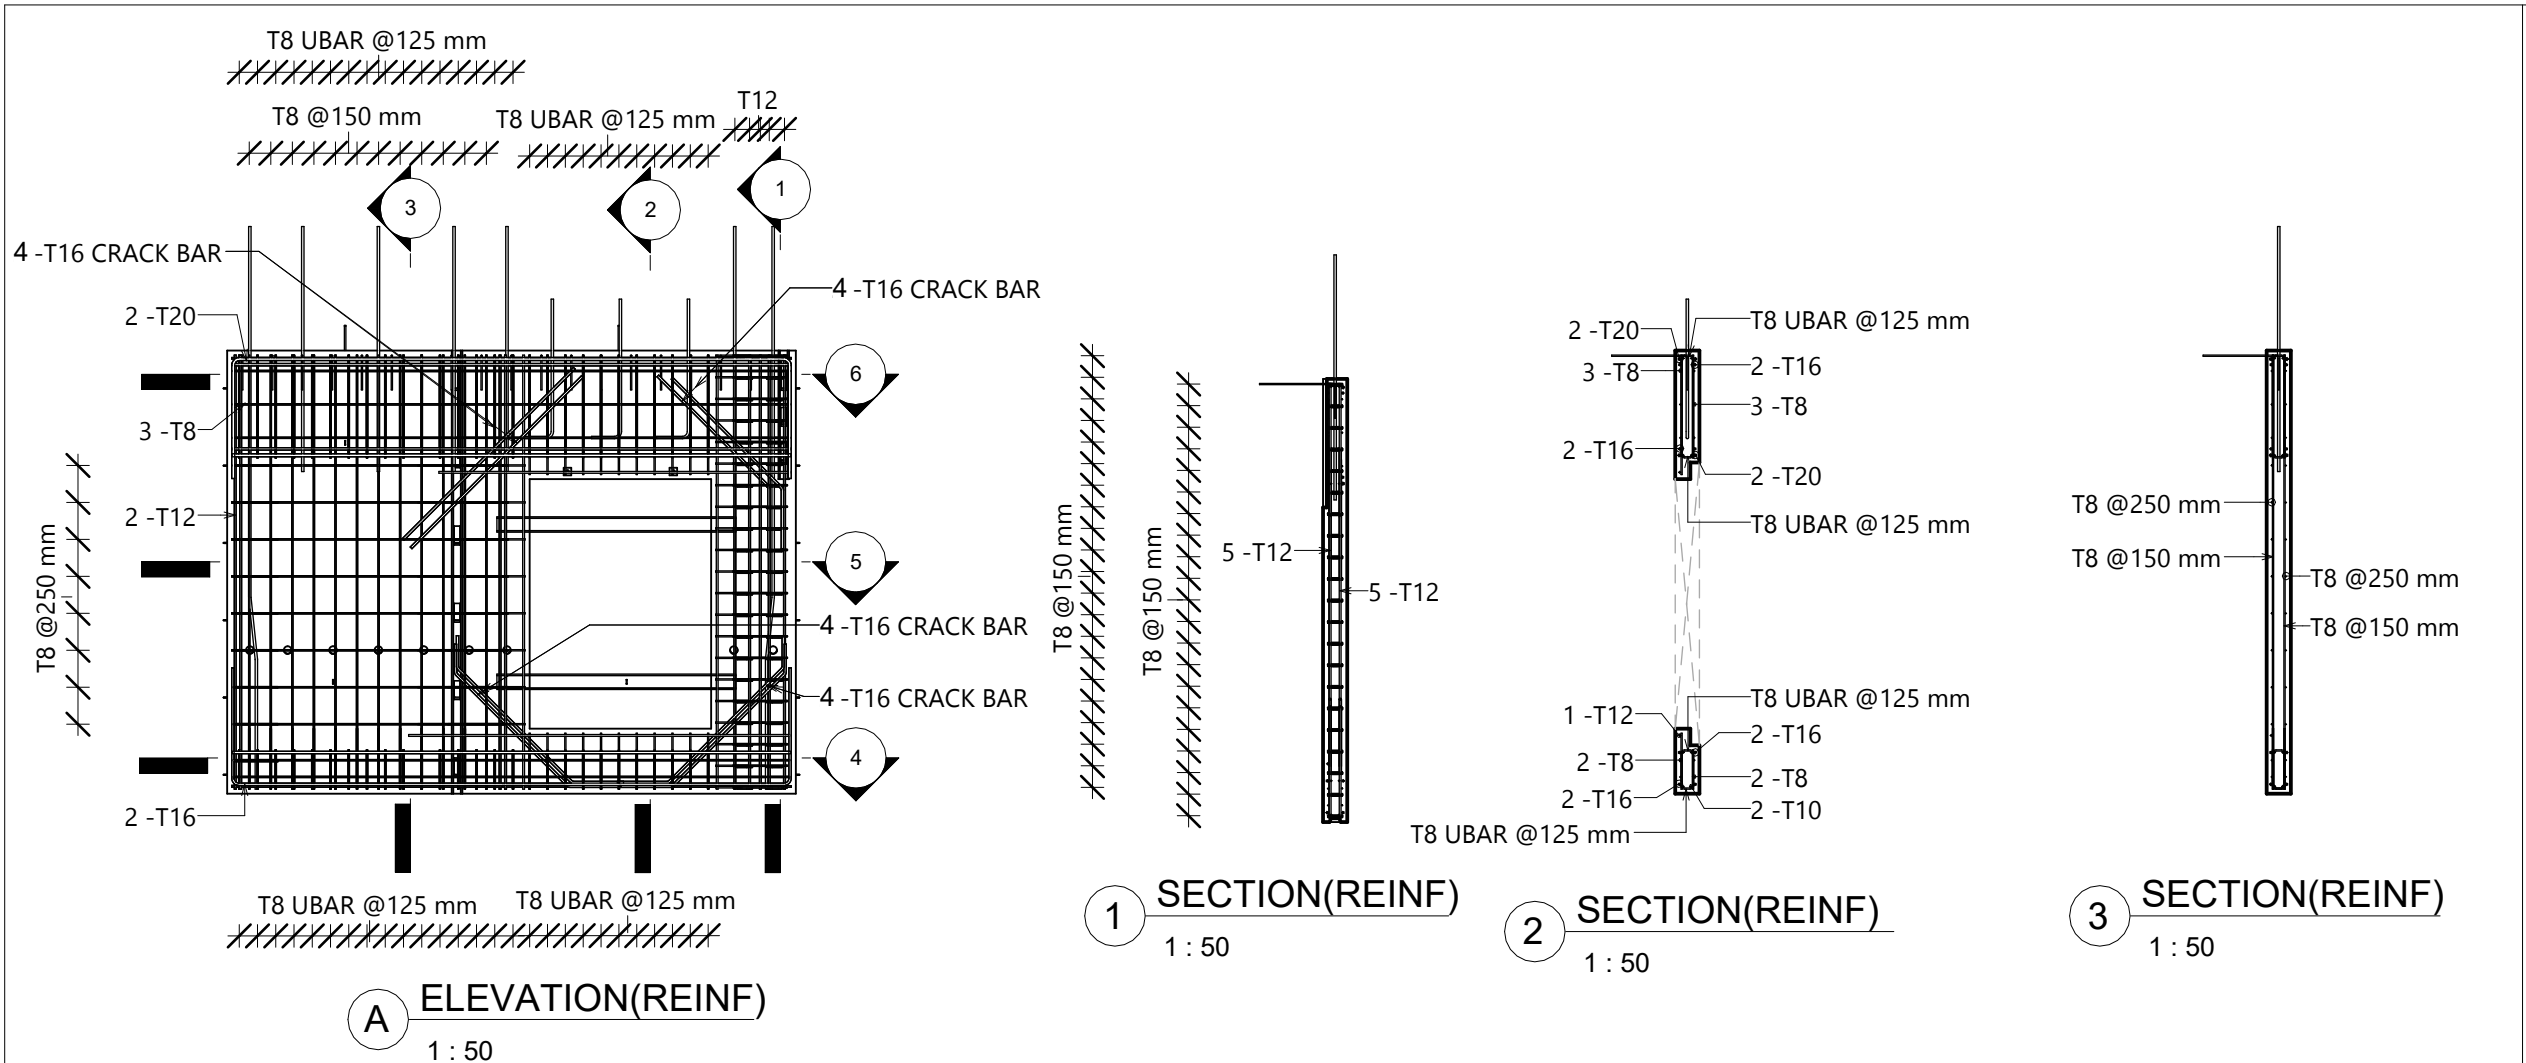


A ELEVATION(REINF)
1 : 50

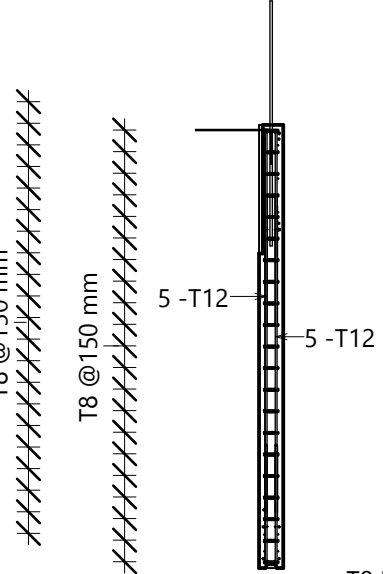


1 SECTION(REINF)
1 : 50

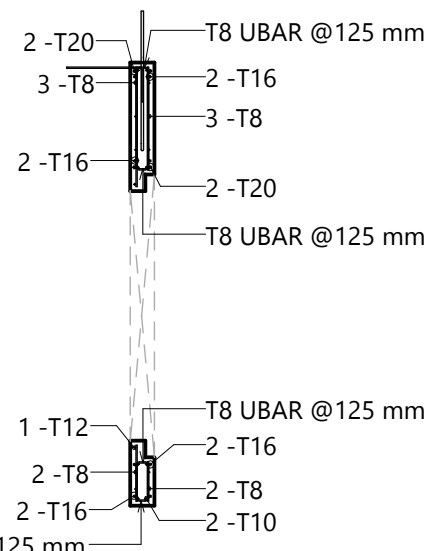


2 SECTION(REINF)
1 : 50

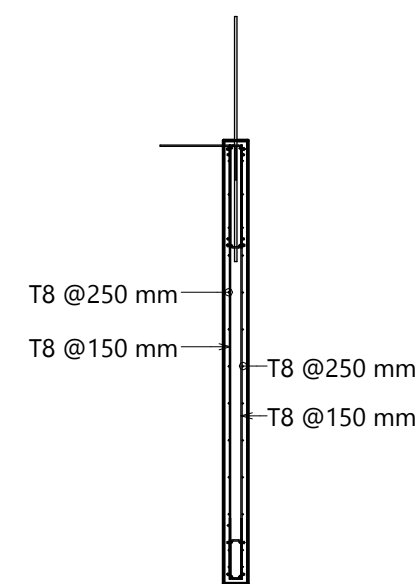


3 SECTION(REINF)
1 : 50

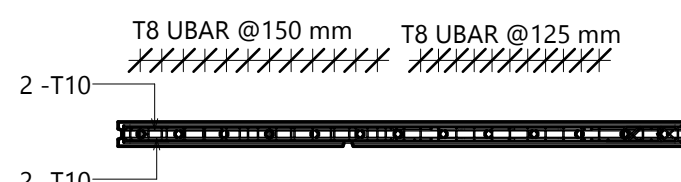

4 SECTION(REINF)
1 : 50

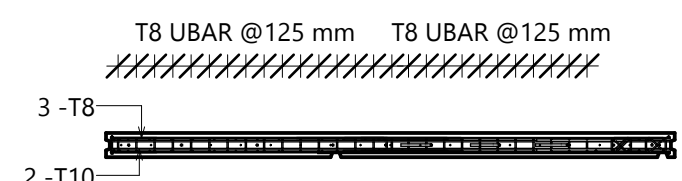

6 SECTION(REINF)
1 : 50

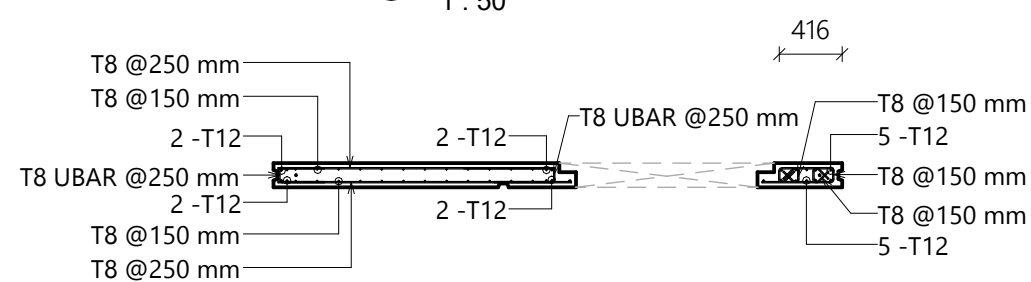

5 SECTION(REINF)
1 : 50

NOTE:
LENGTH,LIFTING,DEMOULDING,DOWEL TUBE,
DOWEL BAR,PROJECTING BAR,U-BAR
REFER FOR INDIVIDUAL MOULD DRAWING

NOTE:
REINFORCEMENT TYPICAL FOR ;
PW-GF-02,PW-1F-02,
PW-2F-02,PW-3F-02,PW-4F-02,
PW-5F-02,PW-6F-02,PW-7F-02

Summary Schedule		
Bar Diameter	Total Bar Length	Weight
8 mm	324150 mm	128.07 kg
10 mm	33200 mm	20.50 kg
12 mm	62400 mm	55.47 kg
16 mm	76650 mm	121.13 kg
20 mm	17850 mm	44.08 kg
	514250 mm	369.24 kg

PROJECT -:

APOLLO GIRLS HOSTEL BUILDING
(RIGHT WING)-CHITTOOR

GENERAL NOTES:

GRADE OF CONCRETE - M40

GRADE OF STEEL - Fe550

STRIPPING STRENGTH - M20

LIFTING,TRANSPORTATION
AND ERECTION - M35

COVER:

WALL - 30mm

ALL DIMENSIONS ARE IN MM

LEGENDS:

ERECTION MARK -

MOULD FACE -

CONTRACTOR -:

VME PRECAST PRODUCTS

 124,Eraiyr Road,Vallam (A) Village,
Sriperumbudur,Kanchipuram-602105,
Tamil Nadu,India Chennai-600 037,India

STRUCTURAL CONSULTANT -:

ES STRUCTURAL CONSULTANT

 B167, 12th cross street, Jawahar Nagar,
Palayamkottai, Tirunelveli-627007
Cell No : +91 98658 03764

0	17-05-26	FOR PRODUCTION	ELA	PRC
Rev	Date	Description	Chkd	Appd.

REVISION SCHEDULE

DRAWING TITLE -:

PW-GF-02-REINF DRAWING

ES JOB NO : ESP25087	DRAWN BY:- GMP
ELEMENT NO : PW-GF-02	SHEET SIZE:- A3
SHEET NO : PW-GF-02(R)	REV.NO:- 0
SCALE : 1 : 50	LEVEL :