




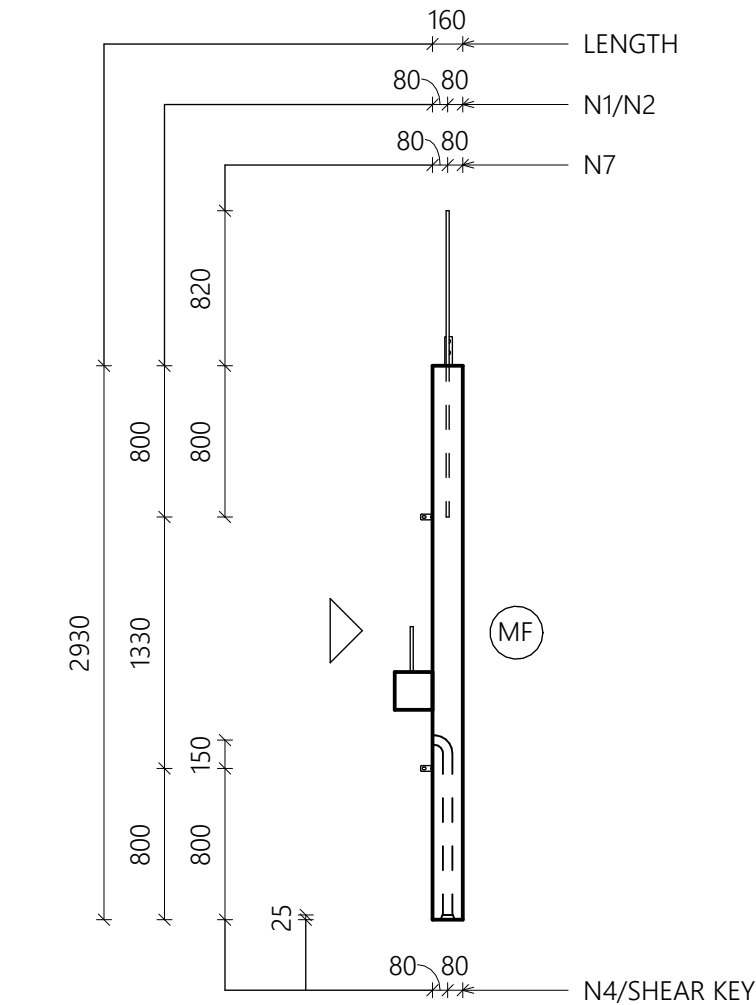


2 SECTION
1 : 40

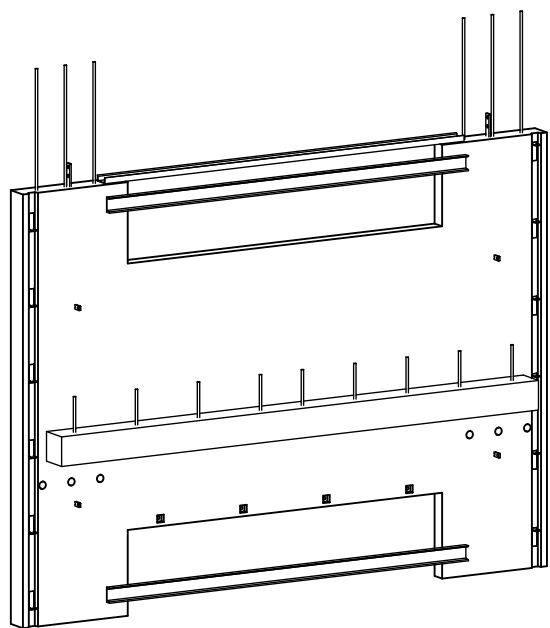


6 3D VIEW

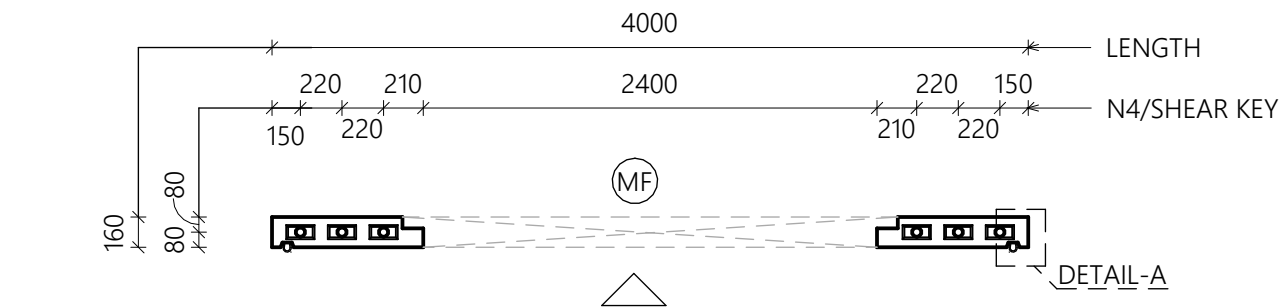


3 SECTION
1 : 40

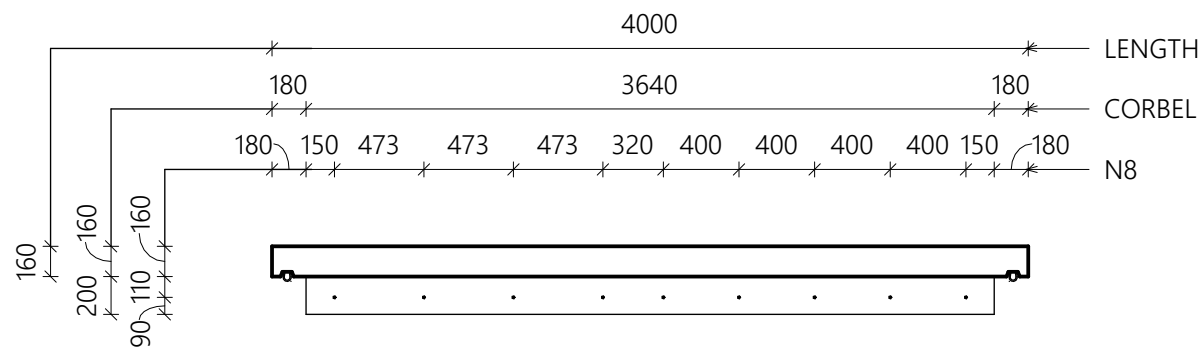

4 SECTION
1 : 40

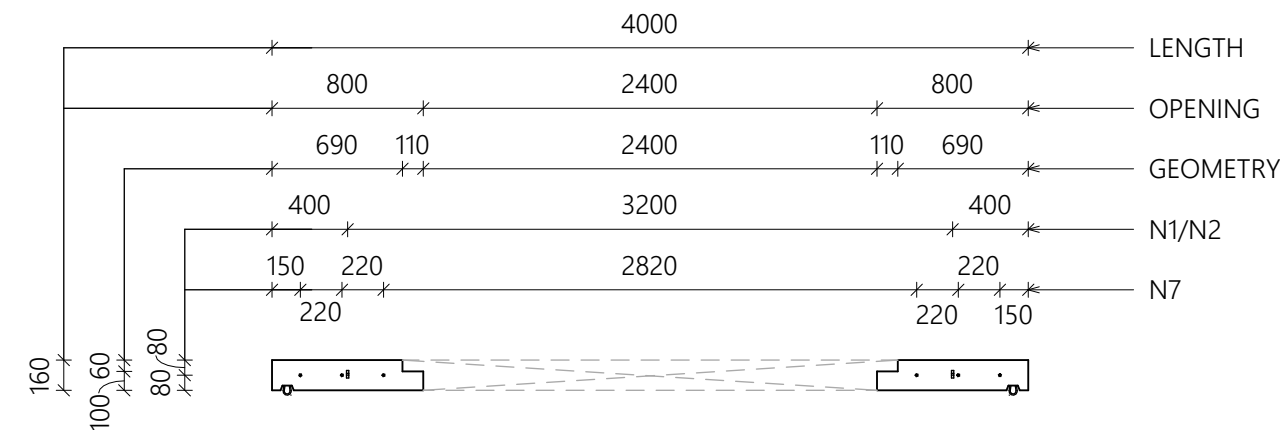

5 SECTION
1 : 40

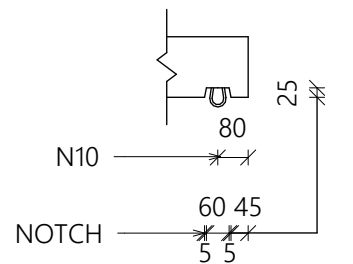

NOTCH DETAIL-A

Dowel Bar Schedule		
Ref No	Bar Diameter	Count
N7	16 mm	6
N8	16 mm	9

Weight Schedule	
Volume	Weight
1.52 m ³	3789.17 kg

Insert Schedule		
Ref No	Type	Count
N1	RR-SA-4.0-240	2
N2	RR-SA-2.5-150	4
N4	50 DIA SLEEVE	6
N5	20 Dia Sleeve	4
N10	Wire Loop	12

PROJECT -:

APOLLO GIRLS HOSTEL BUILDING
(RIGHT WING)-CHITTOOR

GENERAL NOTES:

- GRADE OF CONCRETE - M40
- GRADE OF STEEL - Fe550
- STRIPPING STRENGTH - M20
- LIFTING,TRANSPORTATION AND ERECTION - M35

COVER:

- WALL - 30mm

ALL DIMENSIONS ARE IN MM

LEGENDS:

- ERECTION MARK -
- MOULD FACE -

CONTRACTOR -:

VME PRECAST PRODUCTS

124,Eraiur Road,Vallam (A) Village,
Sriperumbudur,Kanchipuram-602105,
Tamil Nadu,India Chennai-600 037,India

STRUCTURAL CONSULTANT -:

ES STRUCTURAL CONSULTANT
B167, 12th cross street, Jawahar Nagar,
Palayamkottai, Tirunelveli-627007
Cell No : +91 98658 03764

0	16-05-26	FOR PRODUCTION	GRS	PRC
Rev	Date	Description	Chkd	Appd.

REVISION SCHEDULE

DRAWING TITLE -:

PW-GF-09-MOULD DRAWING

ES JOB NO : ESP25087	DRAWN BY:- GMP
ELEMENT NO : PW-GF-09	SHEET SIZE:- A3
SHEET NO : PW-GF-09(M2)	REV.NO:- 0
SCALE : As indicated	LEVEL :