



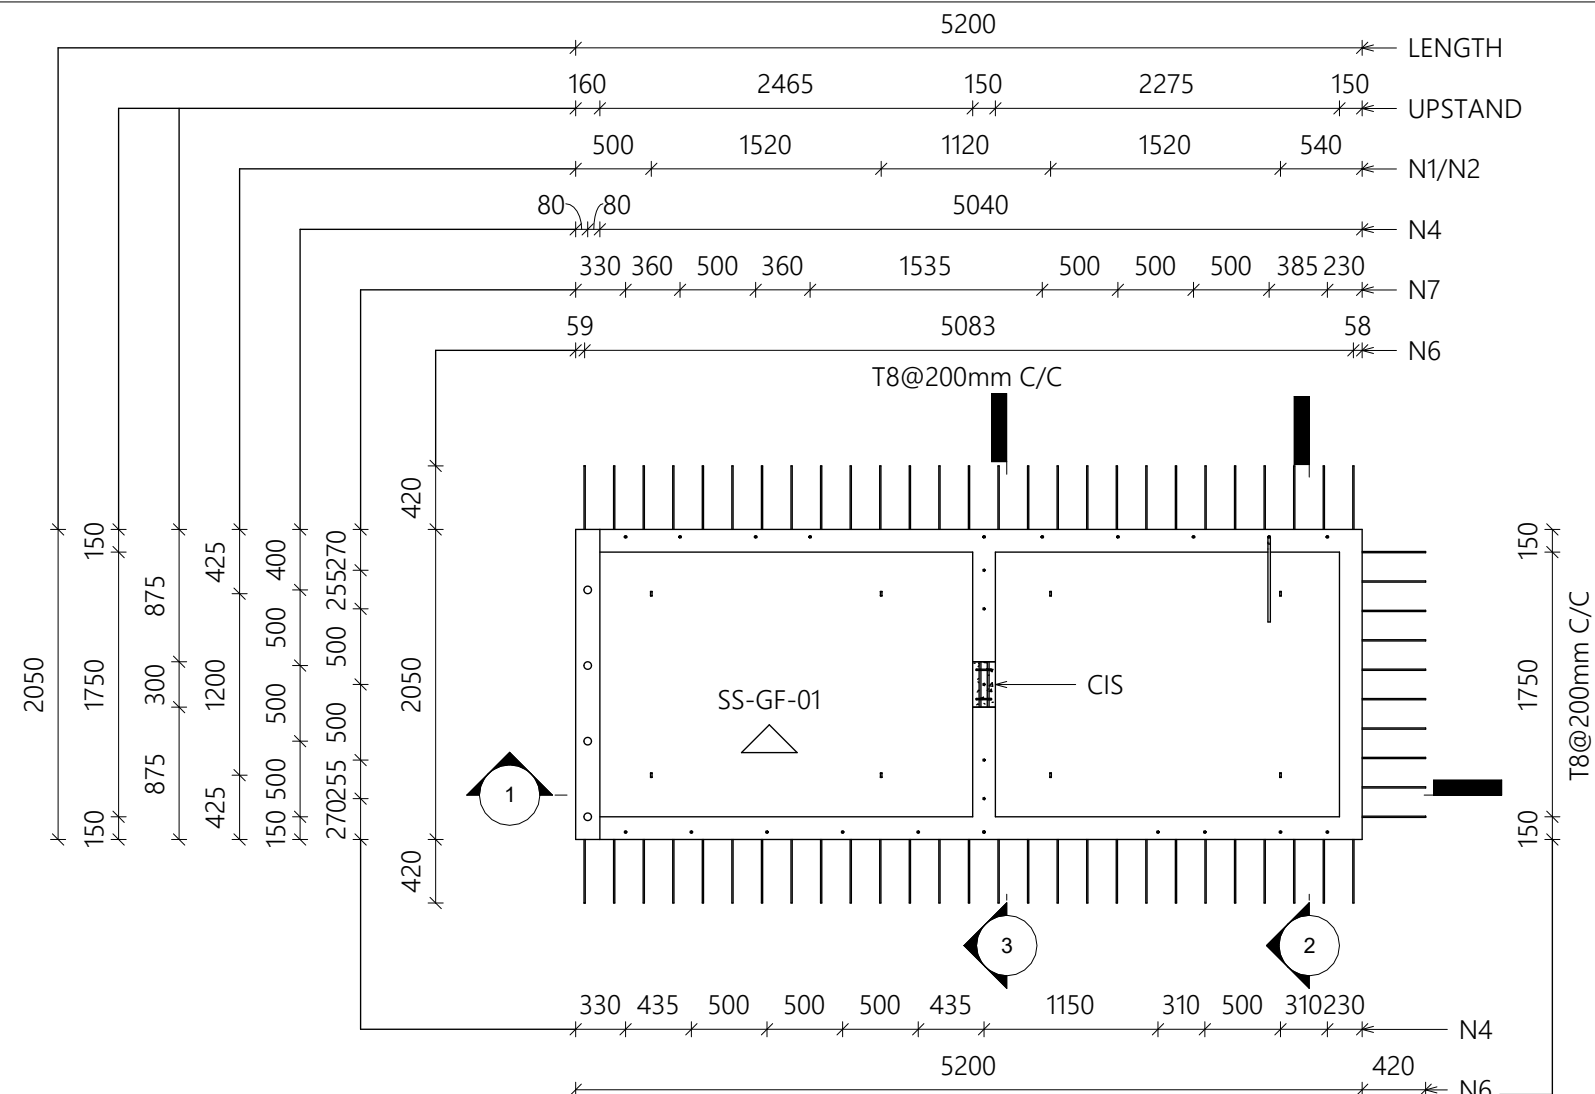

A TOP PLAN
1 : 50

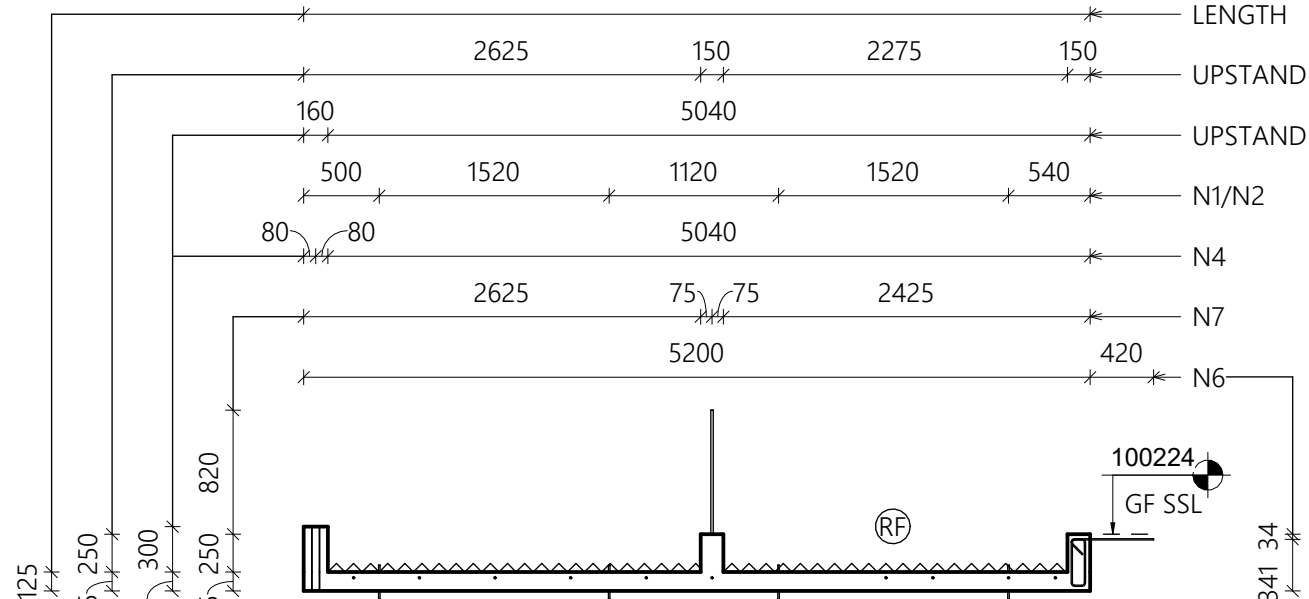


1 SECTION
1 : 50

Weight Schedule	
Volume	Weight
1.93 m ³	4813.91 kg


Projecting Bar Schedule		
Ref No	Bar Diameter	Count
N6	8 mm	64

Dowel Bar Schedule		
Ref No	Bar Diameter	Count
N7	16 mm	25


Insert Schedule		
Ref No	Type	Count
N1	RR-SA-2.5-150	8
N2	RR-SA-2.5-150	8
N4	50 Dia Sleeve	4

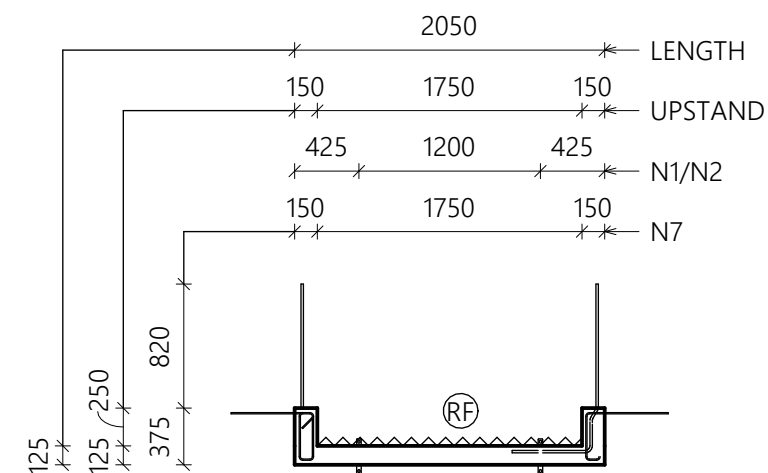

2 SECTION
1 : 50

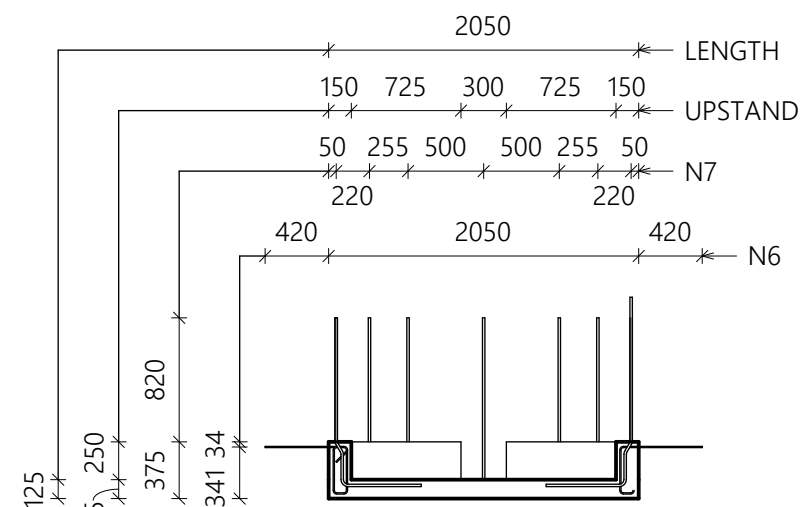

3 SECTION
1 : 50

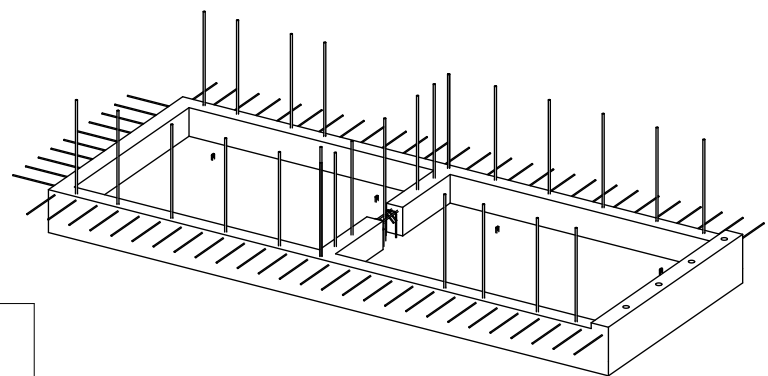

4 3D VIEW

PROJECT -:

APOLLO GIRLS HOSTEL BUILDING
(RIGHT WING)-CHITTOOR

GENERAL NOTES:

GRADE OF CONCRETE - M40
GRADE OF STEEL - Fe550
RELEASE STRENGTH - M20
LIFTING,TRANSPORTATION
AND ERECTION - M35

COVER:

SOLID SLAB - 30mm
ALL DIMENSIONS ARE IN MM

LEGENDS:

ERECTION MARK -

CONTRACTOR -:

VME PRECAST PRODUCTS
 124,Eraiur Road,Vallam (A) Village,
Sriperumbudur,Kanchipuram-602105,
Tamil Nadu,India Chennai-600 037,India

STRUCTURAL CONSULTANT -:

ES STRUCTURAL CONSULTANT
 B167, 12th cross street, Jawahar Nagar,
Palayamkottai, Tirunelveli-627007
Cell No : +91 98658 03764

0	21-05-26	FOR PRODUCTION	ELA	PRC
Rev	Date	Description	Chkd	Appd.

REVISION SCHEDULE

DRAWING TITLE -:

SS-GF-01-MOULD DRAWING

ES JOB NO : ESP25087	DRAWN BY:- GRS
ELEMENT NO : SS-GF-01	SHEET SIZE:- A3
SHEET NO : SS-GF-01(M)	REV.NO:- 0
SCALE : 1 : 50	LEVEL :