




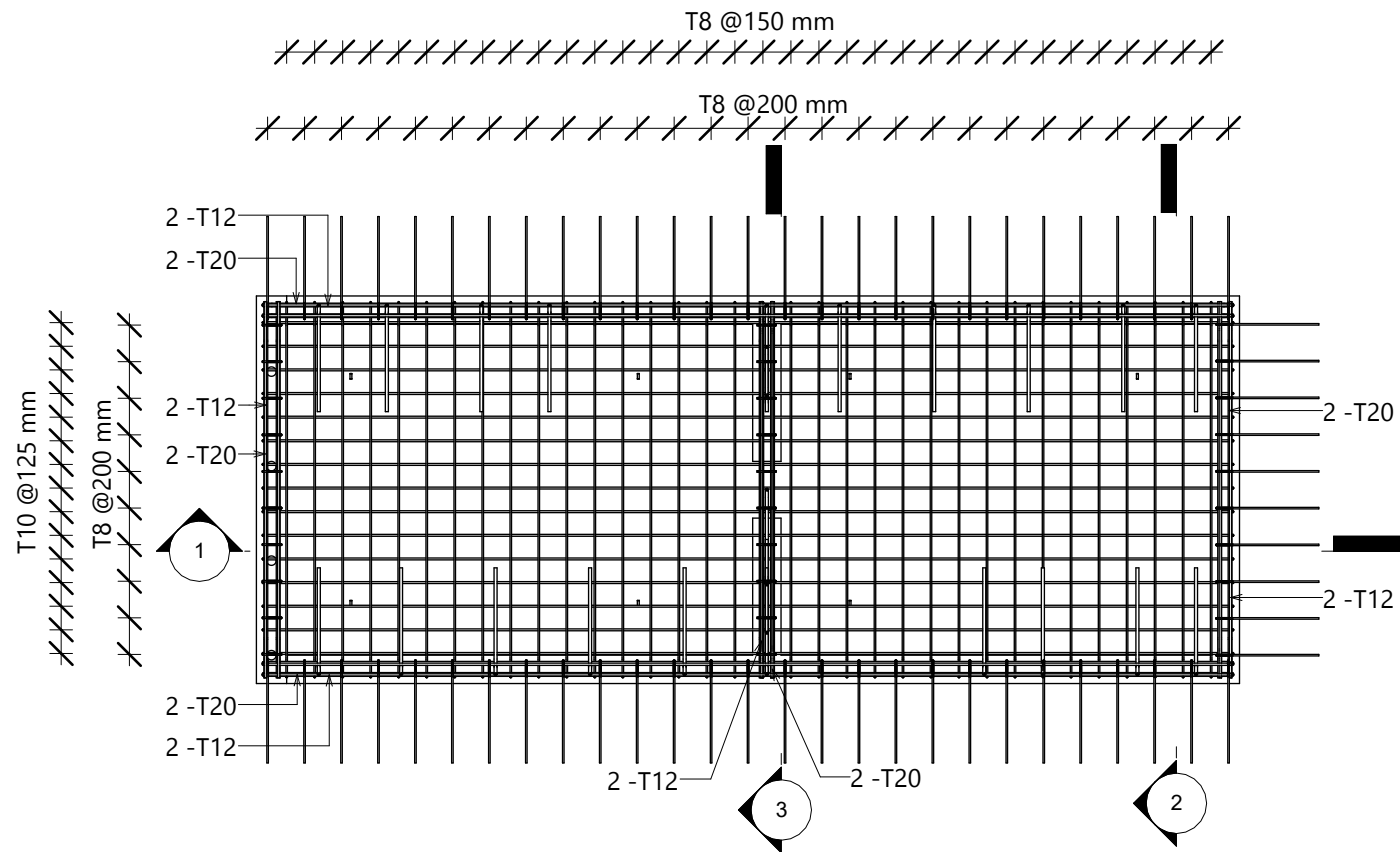


A TOP PLAN(REINF)
1 : 40

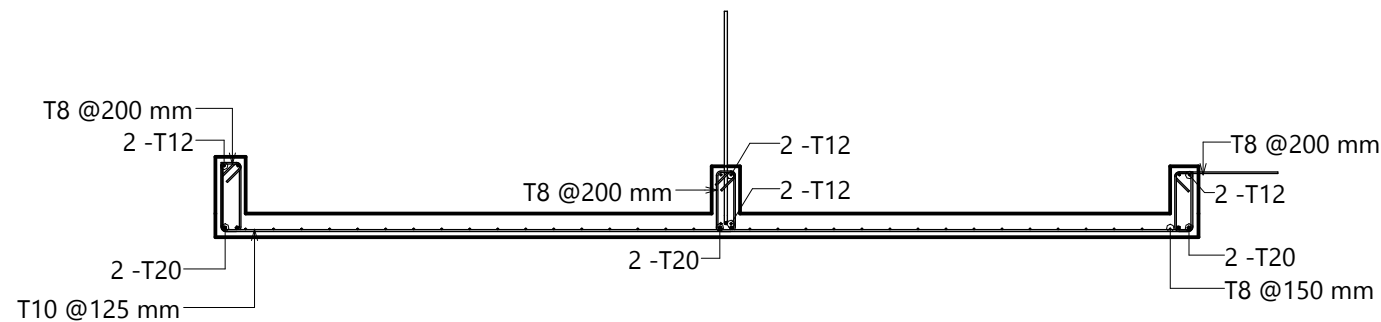

1 SECTION(REINF)
1 : 40

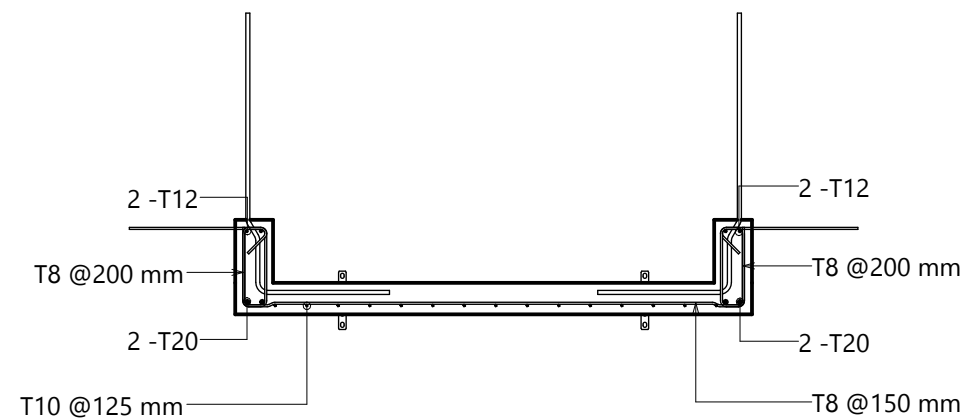

2 SECTION(REINF)
1 : 30

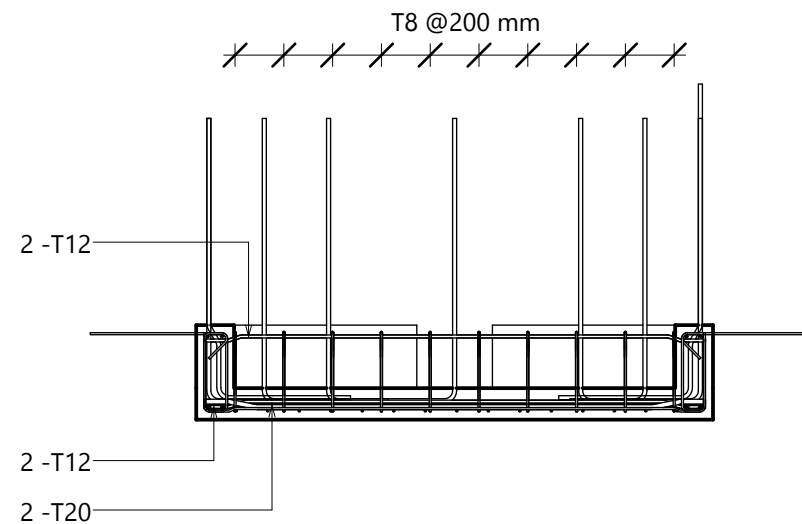

3 SECTION(REINF)
1 : 30

Summary Schedule		
Bar Diameter	Total Bar Length	Weight
8 mm	201100 mm	79.45 kg
10 mm	87000 mm	53.71 kg
12 mm	38700 mm	34.40 kg
16 mm	42700 mm	67.48 kg
20 mm	34800 mm	85.93 kg
	404300 mm	320.97 kg

NOTE:

LENGTH,LIFTING,DEMOULDING,DOWEL TUBE,
DOWEL BAR,PROJECTING BAR,U-BAR
REFER FOR INDIVIDUAL MOULD DRAWING

NOTE:

REINFORCEMENT TYPICAL FOR;
SS-GF-01,SS-GF-06,SS-1F-01,SS-1F-04,SS-1F-07,
SS-1F-09,SS-2F-01,SS-2F-04,SS-2F-07,SS-2F-09,
SS-3F-01,SS-3F-04,SS-3F-07,SS-3F-09

PROJECT -:

APOLLO GIRLS HOSTEL BUILDING
(RIGHT WING)-CHITTOOR

GENERAL NOTES:

GRADE OF CONCRETE - M40
GRADE OF STEEL - Fe550
RELEASE STRENGTH - M20
LIFTING,TRANSPORTATION
AND ERECTION - M35

COVER:

SOLID SLAB - 30mm
ALL DIMENSIONS ARE IN MM

LEGENDS:

ERECTION MARK -

CONTRACTOR -:

VME PRECAST PRODUCTS
 124,Eraiur Road,Vallam (A) Village,
Sriperumbudur,Kanchipuram-602105,
Tamil Nadu,India Chennai-600 037,India

STRUCTURAL CONSULTANT -:

ES STRUCTURAL CONSULTANT
 B167, 12th cross street, Jawahar Nagar,
Palayamkottai, Tirunelveli-627007
Cell No : +91 98658 03764

0	21-05-26	FOR PRODUCTION	ELA	PRC
Rev	Date	Description	Chkd	Appd.

REVISION SCHEDULE

DRAWING TITLE -:

SS-GF-01-REINF DRAWING

ES JOB NO : ESP25087	DRAWN BY:- GRS
ELEMENT NO : SS-GF-01	SHEET SIZE:- A3
SHEET NO : SS-GF-01(R)	REV.NO:- 0
SCALE : As indicated	LEVEL :