




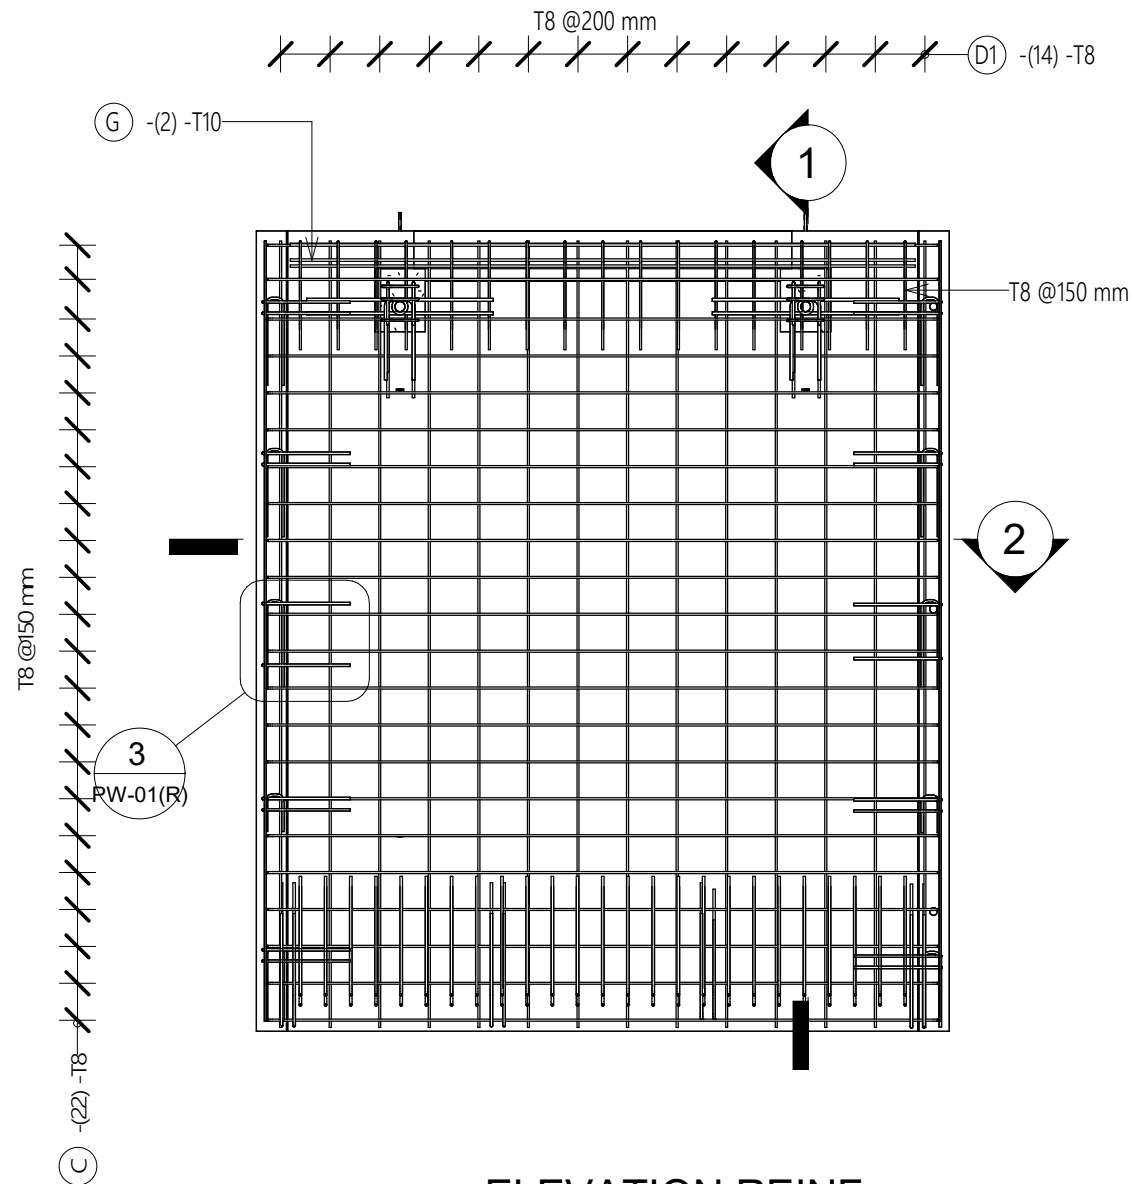


A ELEVATION REINF
1 : 30

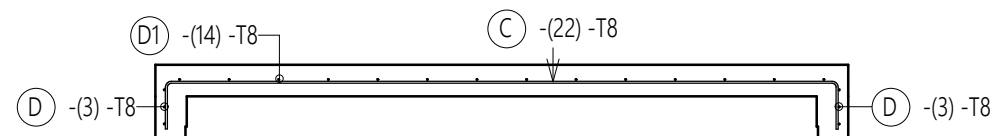

2 SECTION REINF
1 : 30

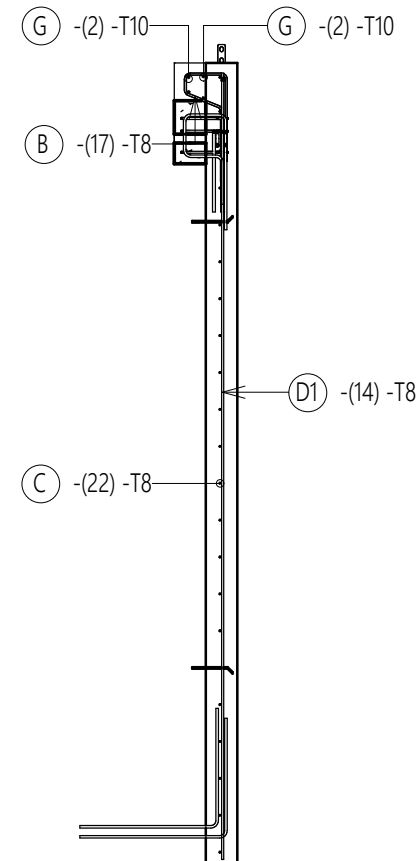

1 SECTION REINF
1 : 30

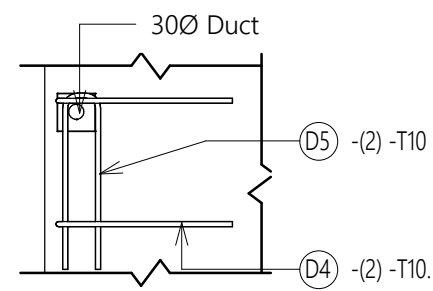

3 U-BAR DETAIL
1 : 15

PROJECT -:
VME PRECAST PRODUCTS

- GENERAL NOTES:**
- COVER = 40mm
 - CONCRETE GRADE = M40
 - STEEL GRADE = Fe500
 - ALL DIMENSIONS ARE IN mm.

CONTRACTOR -:
VME PRECAST PRODUCTS
124, Eraiyur Road, Vallam (A) Village,
Sriperumbudur, Kanchipuram-602105,
Tamil Nadu, India Chennai-600 037, India

STRUCTURAL CONSULTANT -:
ES STRUCTURAL CONSULTANT
B167, 12th cross street, Jawahar Nagar,
Palayamkottai, Tirunelveli-627007
Tel.No:0462 2553764/4950764

0	24-06-24	FOR APPROVAL	MS	PRC
---	----------	--------------	----	-----

Rev	Date	Description	Chkd	Appd.
REVISION SCHEDULE				

DRAWING TITLE -:
PW-01 REINF DRAWING

JOB NO : ESP22077	DRAWN BY:- MK
ELEMENT NO : PW-01	SHEET SIZE:- A3
SHEET NO : PW-01(R)	REV.NO:- 0
SCALE : As indicated	LEVEL :